



OCTOBER UNIVERSITY FOR MODERN SCIENCES & ARTS Architectural Engineering Department Spring 2025

Course Information:

ASE 464

WORKING DRAWINGS III

Student Name: Hadeel Zakaria

ID: 220009

Group: A

Course Instructors:

Dr. Tarek Galal

Eng. Hend

Eng. Nermeen

Eng. Yousra



GENERAL NOTES








- ALL MATERIALS & WORK PRACTICES SHALL COMPLY WITH, BUT NOT LIMITED TO THE BUILDING REGULATION 2019, THE NATIONAL CONSTRUCTION CODE of EGYPT UNLESS OTHERWISE SPECIFIED.

-ALL DIMENSIONS ARE IN METERS. IF IN DOUBT ASK, DO NOT SCALE.

-THESE DRAWINGS SHALL BE READ IN CONJUNCTION WITH ALL RELEVANT STRUCTURAL + ALL OTHER CONSULTANTS DRAWINGS/DETAILS & WITH ANY OTHER WRITTEN INSTRUCTIONS ISSUED IN THE COURSE OF THE CONTRACT.

- THESE DRAWINGS SHALL BE READ IN CONJUNCTION WITH ANY ENERGY RATING REPORT + SHALL BE CONSTRUCTED IN ACCORDANCE WITH THE STAMPED PLANS ENDORSED BY THE ACCREDITED THERMAL PERFORMANCE ASSESSOR WITHOUT ALTERATION

Symbols Legend

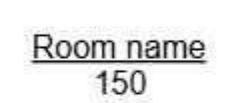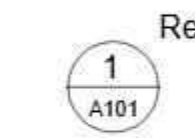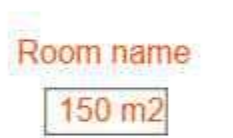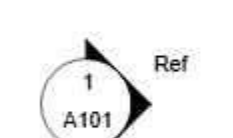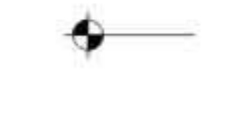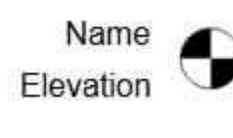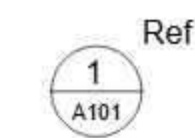Symbol	Descrip tion
	Room Name & Area
	Detail Callout Detail no & Sheet no.
	Centerline
	Door Tag
	Window Tag
	Room Name & Number
	Elevation number & Sheet Number
	Section Number & Sheet Number
	Grid bubble, name and Grid line
	Spot Elevation in Plan
	Level in Elevation or Section
	Section Spot Elevation in Plan
	Level name & Elevation in Elevation or Section
	Detail Callout - Number & Sheet name

	Reinforced Concrete
	Masonry or Brick
	Plain Concrete
	Sand
	Plaster
	Marble
	Wood
	Compacted Earth
	Thermal Insulation
	Membrane Water Proofing
	Carpet
	Mortar
	Metal (Iron/Steel/Aluminium)

Material Description

Room	FLOORING (1)	WALLS (2)	CEILING (3)	SKIRTING (4)
Bedroom	Polyvinyl Wood Tiles	Persian Khaki 1623 wall paint	Acrylic Paint	Ceramic Tiles 10cm x 20cm
Kitchen	Ceramic Tiles	Ceramic Beige Tiles	Acrylic Paint	Ceramic Tiles 10cm x 20cm
Living Room	Polyvinyl Wood Tiles	Persian Khaki 1623 wall paint	Acrylic Paint	Ceramic Tiles 10cm x 20cm
Bathroom	Ceramic Tiles	Ceramic Beige Tiles	Acrylic Paint	Ceramic Tiles 10cm x 20cm
Entrance	Marble	Travertine Stone	Acrylic Paint	Ceramic Tiles 10cm x 20cm
Roof	Ceramic Tiles	Gypsum Board	Acrylic Paint	Ceramic Tiles 10cm x 20cm
Basement	Cement Tiles	Ceramic Beige Tiles	Acrylic Paint	Cement Tiles 10cm x 20cm

Door Schedule						
Mark	Description	Opera tion	Height	Width	Coun t	Family
D1			2.00	2.70	1	DI_2CG_2VB_OTS_A
D2	2 Panel Door		2.03	0.80	24	Doors-Supa_Doors-250
D3	TruStile (TMIR) Series		2.13	0.81	9	Door-TruStile_Doors-TMIR6000
D4			2.10	0.91	6	Door-Exterior-Single-Entry-Half Arch Glass-Wood_Clad
D5			2.13	2.50	2	Door-Double-Sliding
D6			2.13	1.83	1	Door-Exterior-Double
D7	TruStile (TS) Series		2.03	0.72	34	Door-TruStile_Doors-TS3220
D8			2.13	2.50	11	Door-Double-Sliding
D9			2.10	0.91	1	Door-Exterior-Single-Entry-Half Arch Glass-Wood_Clad
D10			2.10	0.81	7	Sliding_Door_Pocket_door_Wood_10126
D11	TruStile (TS) Series		2.03	0.72	1	Door-TruStile_Doors-TS3220
D12	Porte Alu Grand Trafic KL-GT		2.10	1.07	1	K-LINE PORTE GT NEUF KLGT-1VT-ANG
D13	Garage door system BGR/SK 250	Coilin g	2.40	2.60	1	Aluprof_BGR-SK_E_Alu_Garage-Door-Box -250_EN_R-10216_P01
D14			2.03	0.92	1	M_Single-Flush

Window Schedule						
Mark	Description	Operation	Height	Width	Count	Family
W1	Structural corner window with four panels	StructuralC ornerWindo wTiltAndSli de	2.24	2.46	4	Aluprof_MB-79N-SI E_Alu_Window-St ructural-Corner-sa h-T&S-FIX-FIX-T& S_ENG_R-00463
W2	Double fixed window	DoublePan elFix	2.50	2.48	4	Aluprof_MB-45_Alu _Window-2sash-FI X_EN_R-00662
W3			0.50	0.40	9	M_Window-Awning- Single
W4			0.60	0.60	24	M_Window-Awning- Single
W5			1.20	1.20	4	M_Window-Sliding- Double
W6	Double fixed window	DoublePan elFix	2.12	2.48	15	Aluprof_MB-45_Alu _Window-2sash-FI X_EN_R-00662
W7			1.20	0.90	2	M_Window-Sliding- Double
W8			0.45	0.90	1	M_Fixed
W9			0.70	0.50	3	M_Window-Awning- Single
W10	Single sash tilt and turn window	SinglePane lTiltAndTur n	2.00	1.23	6	Aluprof_MB-86-SI E_Alu_Window-1sa sh-Tilt-and-turn_EN G_R-00044
W11			1.20	0.69	1	M_Window-Sliding- Double
W12			1.20	1.80	1	M_Window-Sliding- Double

LIST OF DRAWINGS: NON- ARCHITECTURAL DRAWINGS:

A000	SHEET NAME	SCALE
A001	COVER	-
A002	DRAWING LIST	-
A003	GENERAL NOTES	-
A004	SCHEDULES	-

ARCHITECTURAL DRAWINGS:

A100	SHEET NAME	SCALE
A101	SITE PLAN	1:100
A102	SITE PLAN WITH LANDSCAPE	1:100
A103	BASEMENT PLAN	1:50
A104	GROUND FLOOR	1:50
A105	TYPICAL FLOOR	1:50
A106	ROOF FLOOR	1:50
A107	UPPER FLOOR	1:50

ELEVATIONS DRAWINGS:

A200	SHEET NAME	SCALE
A201	MAIN ELEVATION (SOUTH)	1:50
A202	SIDE ELEVATION (WEST)	1:50
A203	SIDE ELEVATION (EAST)	1:50
A204	BACK ELEVATION (NORTH)	1:50

SECTIONS DRAWINGS:

A300	SHEET NAME	SCALE
A301	LONGITUDINAL SECTION	1:50
A302	CROSS SECTION	1:50
A303	WALL SECTION	1:20
A304	WALL SECTION	1:20
A305	INTERIOR ELEVATIONS	1:10

DETAILS:

A400	SHEET NAME	SCALE
A40-	DETIALS	-

ELECTRICAL DRAWINGS:

E100	SHEET NAME	SCALE
E101	BASMENT PLAN	1:50
E102	GROUND FLOOR PLAN	1:50
E103	TYPICAL FLOOR PLAN	1:50
E104	ROOF FLOOR PLAN	1:50

PLUMBING DRAWINGS:

P100	SHEET NAME	SCALE
P101	BASEMENT PLAN	1:50
P102	GROUND FLOOR PLAN	1:50
P103	TYPICAL FLOOR PLAN	1:50
P104	ROOF FLOOR PLAN	1:50
P105	UPPER FLOOR PLAN	1:50



Course Info:

ASE 464

Working Drawings III

GENERAL NOTES:

- ALL MATERIALS & WORK PRACTICES SHALL COMPLY WITH, BUT NOT LIMITED TO THE BUILDING REGULATION 2019, THE NATIONAL CONSTRUCTION CODE of EGYPT UNLESS OTHERWISE SPECIFIED.

-ALL DIMENSIONS ARE IN METERS. IF IN DOUBT ASK, DO NOT SCALE.

-THESE DRAWINGS SHALL BE READ IN CONJUNCTION WITH ALL RELEVANT STRUCTURAL + ALL OTHER CONSULTANTS DRAWINGS/DETAILS & WITH ANY OTHER WRITTEN INSTRUCTIONS ISSUED IN THE COURSE OF THE CONTRACT.

- THESE DRAWINGS SHALL BE READ IN CONJUNCTION WITH ANY ENERGY RATING REPORT + SHALL BE CONSTRUCTED IN ACCORDANCE WITH THE STAMPED PLANS ENDORSED BY THE ACCREDITED THERMAL PERFORMANCE ASSESSOR WITHOUT ALTERATION



OWNER:



OCTOBER UNIVERSITY
FOR MODERN SCIENCES & ARTS
Architectural Engineering Department
Spring 2025

CLIENTS NAME:

Dr. Tarek Galal
Eng. Hend
Eng. Nermeen
Eng. Yousra

Student Name: Hadeel Zakaria
ID: 220009

PROJECT NAME:
APARTMENT BUILDING

SHEET NAME:

SHEET NO:

SCALE:

DATE: 13-5-2025

Legend 1

1 : 25





MSA UNIVERSITY
IN EGYPT SINCE 1996
Established by Dr. Nassef El Deghry
جامعة أكتوبر للعلوم الحديثة والآداب

Course Info:

ASE 464

Working Drawings III

GENERAL NOTES:

- ALL MATERIALS & WORK PRACTICES SHALL COMPLY WITH, BUT NOT LIMITED TO THE BUILDING REGULATION 2019, THE NATIONAL CONSTRUCTION CODE OF EGYPT UNLESS OTHERWISE SPECIFIED.

- ALL DIMENSIONS ARE IN METERS. IF IN DOUBT ASK, DO NOT SCALE.

- THESE DRAWINGS SHALL BE READ IN CONJUNCTION WITH ALL RELEVANT STRUCTURAL + ALL OTHER CONSULTANTS DRAWINGS/DETAILS & WITH ANY OTHER WRITTEN INSTRUCTIONS ISSUED IN THE COURSE OF THE CONTRACT.

- THESE DRAWINGS SHALL BE READ IN CONJUNCTION WITH ANY ENERGY RATING REPORT + SHALL BE CONSTRUCTED IN ACCORDANCE WITH THE STAMPED PLANS ENDORSED BY THE ACCREDITED THERMAL PERFORMANCE ASSESSOR WITHOUT ALTERATION



OWNER:



MSA UNIVERSITY
جامعة أكتوبر للعلوم الحديثة والآداب



UNIVERSITY of GREENWICH

**OCTOBER UNIVERSITY
FOR MODERN SCIENCES & ARTS
Architectural Engineering Department
Spring 2025**

CLIENTS NAME:

Dr. Tarek Galal

Eng. Hend

Eng. Nermeen

Eng. Yousra

Student Name: Hadeel Zakaria

ID: 220009

PROJECT NAME:

APARTMENT BUILDING

SHEET NAME:

SITE PLAN

SHEET NO:	SCALE:
A101	1:200 1:100

DATE: 13-5-2025



OWNER:

CLIENTS NAME:
Dr. Tarek Galal
Eng. Hend
Eng. Nermeen
Eng. Yousra

Student Name: Hadeel Zakaria
ID: 220009

PROJECT NAME:
APARTMENT BUILDING

SHEET NAME:
SITE PLAN WITH LANDSCAPE

SHEET NO: A102
SCALE: 1:100

DATE: 13-5-2025

SIDE STREET

NEIGHBOURS

MAIN STREET

Schedule of Trees

No.	Shapes	Name	Height
1		American Beech (Deciduous tree)	6.00m
2		Acacia (Shrub)	1.07 m
3		Green Buffer	-

Schedule of Materials

No.	Shapes	Name	Dimension
1		Interlock Herringbone tile	60cm*30cm
2		Plain concrete Curb	10 cm

1 Site Plan with Landscape
1 : 100

Course Info:
ASE 464
Working Drawings III

GENERAL NOTES:

- ALL MATERIALS & WORK PRACTICES SHALL COMPLY WITH, BUT NOT LIMITED TO THE BUILDING REGULATION 2019, THE NATIONAL CONSTRUCTION CODE OF EGYPT UNLESS OTHERWISE SPECIFIED.

- ALL DIMENSIONS ARE IN METERS. IF IN DOUBT ASK, DO NOT SCALE.

Basement Plan
IN CONJUNCTION WITH ALL RELEVANT STRUCTURAL + ALL OTHER CONSULTANTS DRAWINGS/DETAILS & WITH ANY OTHER WRITTEN INSTRUCTIONS ISSUED IN THE COURSE OF THE CONTRACT.

- THESE DRAWINGS SHALL BE READ IN CONJUNCTION WITH ANY ENERGY RATING REPORT + SHALL BE CONSTRUCTED IN ACCORDANCE WITH THE STAMPED PLANS ENDORSED BY THE ACCREDITED THERMAL PERFORMANCE ASSESSOR WITHOUT ALTERATION.



OWNER:



OCTOBER UNIVERSITY
FOR MODERN SCIENCES & ARTS
Architectural Engineering Department
Spring 2025

CLIENTS NAME:

Dr. Tarek Galal
Eng. Hend
Eng. Nermeen
Eng. Yousra


Student Name: Hadeel Zakaria
ID: 220009

PROJECT NAME:
APARTMENT BUILDING

SHEET NAME:
BASEMENT FLOOR PLAN

SHEET NO: A103
SCALE: 1:50

DATE: 13-5-2025

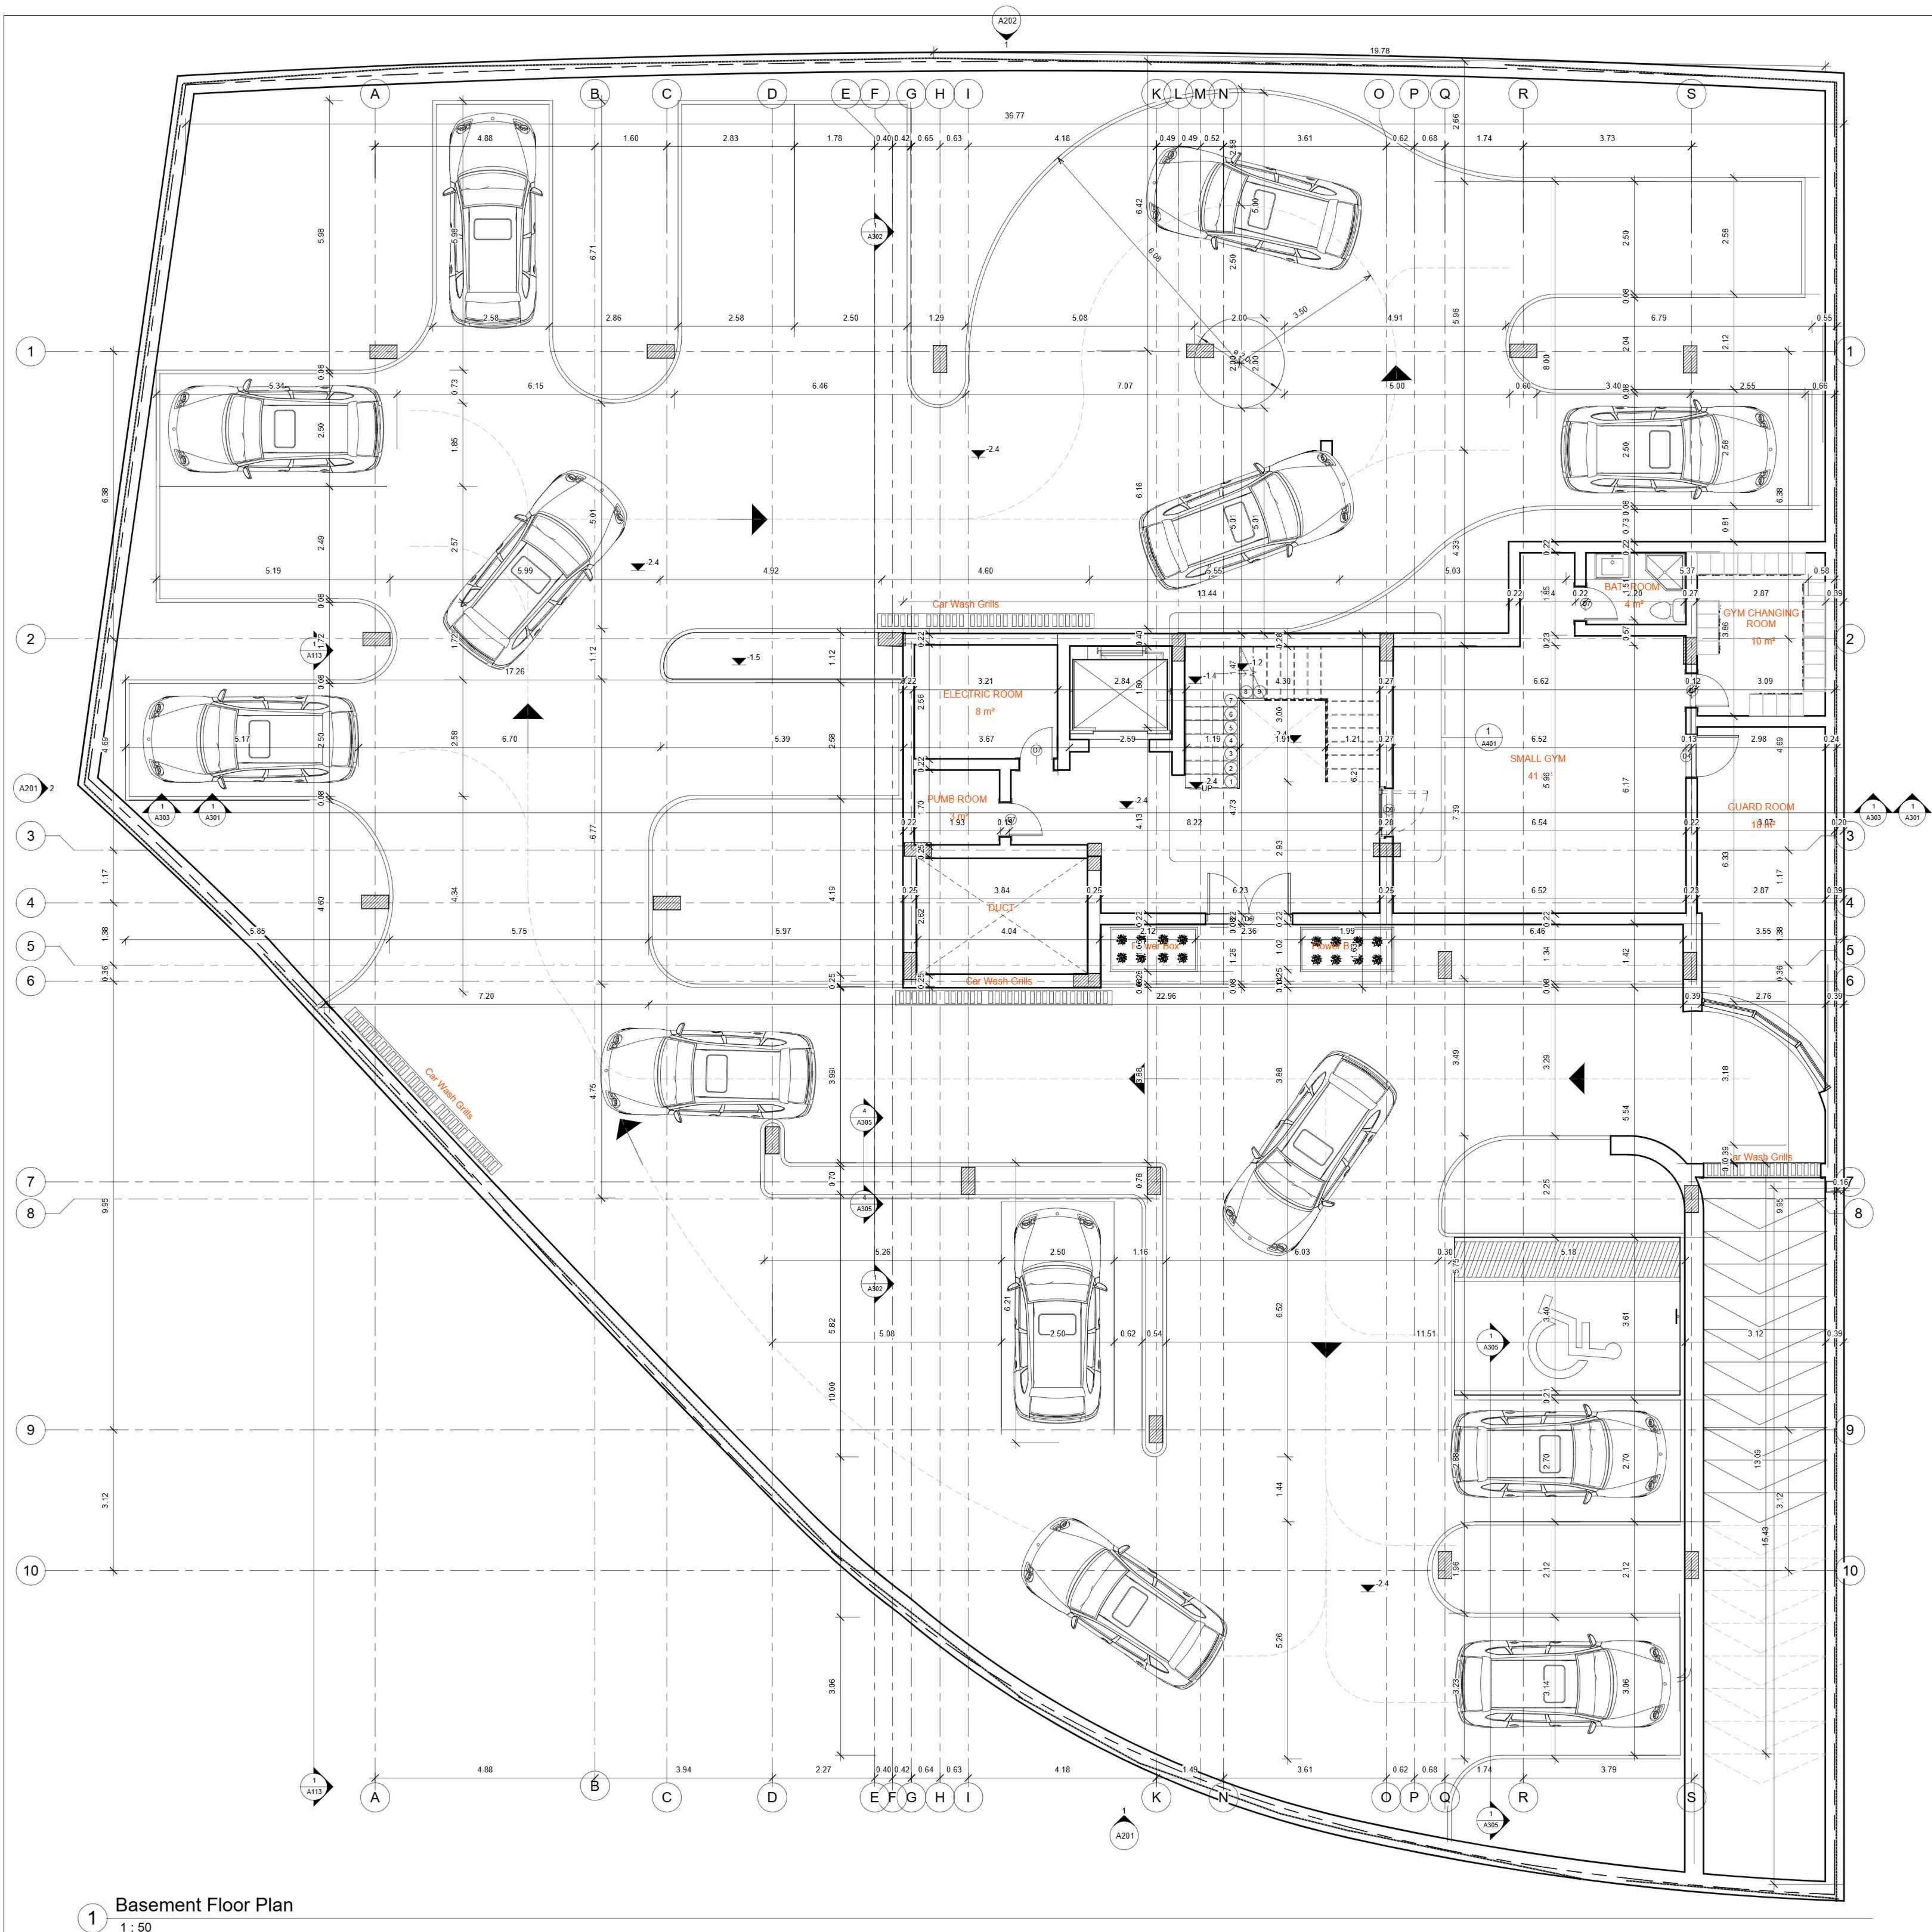

1 Basement Floor Plan
1:50

Course Info:
ASE 464
Working Drawings III

GENERAL NOTES:
- ALL MATERIALS & WORK PRACTICES SHALL COMPLY WITH, BUT NOT LIMITED TO THE BUILDING REGULATION 2019, THE NATIONAL CONSTRUCTION CODE OF EGYPT UNLESS OTHERWISE SPECIFIED.
- ALL DIMENSIONS ARE IN METERS. IF IN DOUBT ASK, DO NOT SCALE.
- THESE DRAWINGS SHALL BE READ IN CONJUNCTION WITH ALL RELEVANT STRUCTURAL + ALL OTHER CONSULTANTS DRAWINGS/DETAILS & WITH ANY OTHER WRITTEN INSTRUCTIONS ISSUED IN THE COURSE OF THE CONTRACT.
- THESE DRAWINGS SHALL BE READ IN CONJUNCTION WITH ANY ENERGY RATING REPORT + SHALL BE CONSTRUCTED IN ACCORDANCE WITH THE STAMPED PLANS ENDORSED BY THE ACCREDITED THERMAL PERFORMANCE ASSESSOR WITHOUT ALTERATION



OWNER:



OCTOBER UNIVERSITY
FOR MODERN SCIENCES & ARTS
Architectural Engineering Department
Spring 2025

CLIENTS NAME:
Dr. Tarek Galal
Eng. Hend
Eng. Nermeen
Eng. Yousra

Student Name: Hadeel Zakaria
ID: 220009

PROJECT NAME:
APARTMENT BUILDING

SHEET NAME:
GROUND FLOOR PLAN

SHEET NO: A104
SCALE: 1:50

DATE: 13-5-2025



1 Ground Floor Plan
1: 50

Course Info:
ASE 464
Working Drawings III

GENERAL NOTES:
- ALL MATERIALS & WORK PRACTICES SHALL COMPLY WITH, BUT NOT LIMITED TO THE BUILDING REGULATION 2019, THE NATIONAL CONSTRUCTION CODE OF EGYPT UNLESS OTHERWISE SPECIFIED.
- ALL DIMENSIONS ARE IN METERS. IF IN DOUBT ASK, DO NOT SCALE.
First Floor Plan
- THESE DRAWINGS SHALL BE READ IN CONJUNCTION WITH ANY ENERGY RATING REPORT + SHALL BE CONSTRUCTED IN ACCORDANCE WITH THE STAMPED PLANS ENDORSED BY THE ACCREDITED THERMAL PERFORMANCE ASSESSOR WITHOUT ALTERATION



OWNER:
MSA UNIVERSITY
جامعة أكتوبر للعلوم الحديثة والآداب
UNIVERSITY of GREENWICH
OCTOBER UNIVERSITY
FOR MODERN SCIENCES & ARTS
Architectural Engineering Department
Spring 2025

CLIENTS NAME:
Dr. Tarek Galal
Eng. Hend
Eng. Nermeen
Eng. Yousra

Student Name: Hadeel Zakaria
ID: 220009

PROJECT NAME:
APARTMENT BUILDING

SHEET NAME:
FIRST FLOOR PLAN

SHEET NO: A105
SCALE: 1:50

DATE: 13-5-2025



1 First Floor Plan
1 : 50

Course Info:

ASE 464

Working Drawings III

GENERAL NOTES:

- ALL MATERIALS & WORK PRACTICES SHALL COMPLY WITH, BUT NOT LIMITED TO THE BUILDING REGULATION 2019, THE NATIONAL CONSTRUCTION CODE OF EGYPT UNLESS OTHERWISE SPECIFIED.

- ALL DIMENSIONS ARE IN METERS. IF IN DOUBT ASK, DO NOT SCALE.

- THESE DRAWINGS SHALL BE READ IN CONJUNCTION WITH ALL RELEVANT STRUCTURAL + ALL OTHER CONSULTANTS DRAWINGS/DETAILS & WITH ANY OTHER WRITTEN INSTRUCTIONS ISSUED IN THE COURSE OF THE CONTRACT.

- THESE DRAWINGS SHALL BE READ IN CONJUNCTION WITH ANY ENERGY RATING REPORT + SHALL BE CONSTRUCTED IN ACCORDANCE WITH THE STAMPED PLANS ENDORSED BY THE ACCREDITED THERMAL PERFORMANCE ASSESSOR WITHOUT ALTERATION

Roof Floor Plan

A106



OWNER:



OCTOBER UNIVERSITY
FOR MODERN SCIENCES & ARTS
Architectural Engineering Department
Spring 2025

CLIENTS NAME:

Dr. Tarek Galal
Eng. Hend
Eng. Nermeen
Eng. Yousra

Student Name: Hadeel Zakaria

ID: 220009

PROJECT NAME:
APARTMENT BUILDING

SHEET NAME:

ROOF FLOOR PLAN


SHEET NO:

A106

SCALE:

1:50


DATE: 13-5-2025

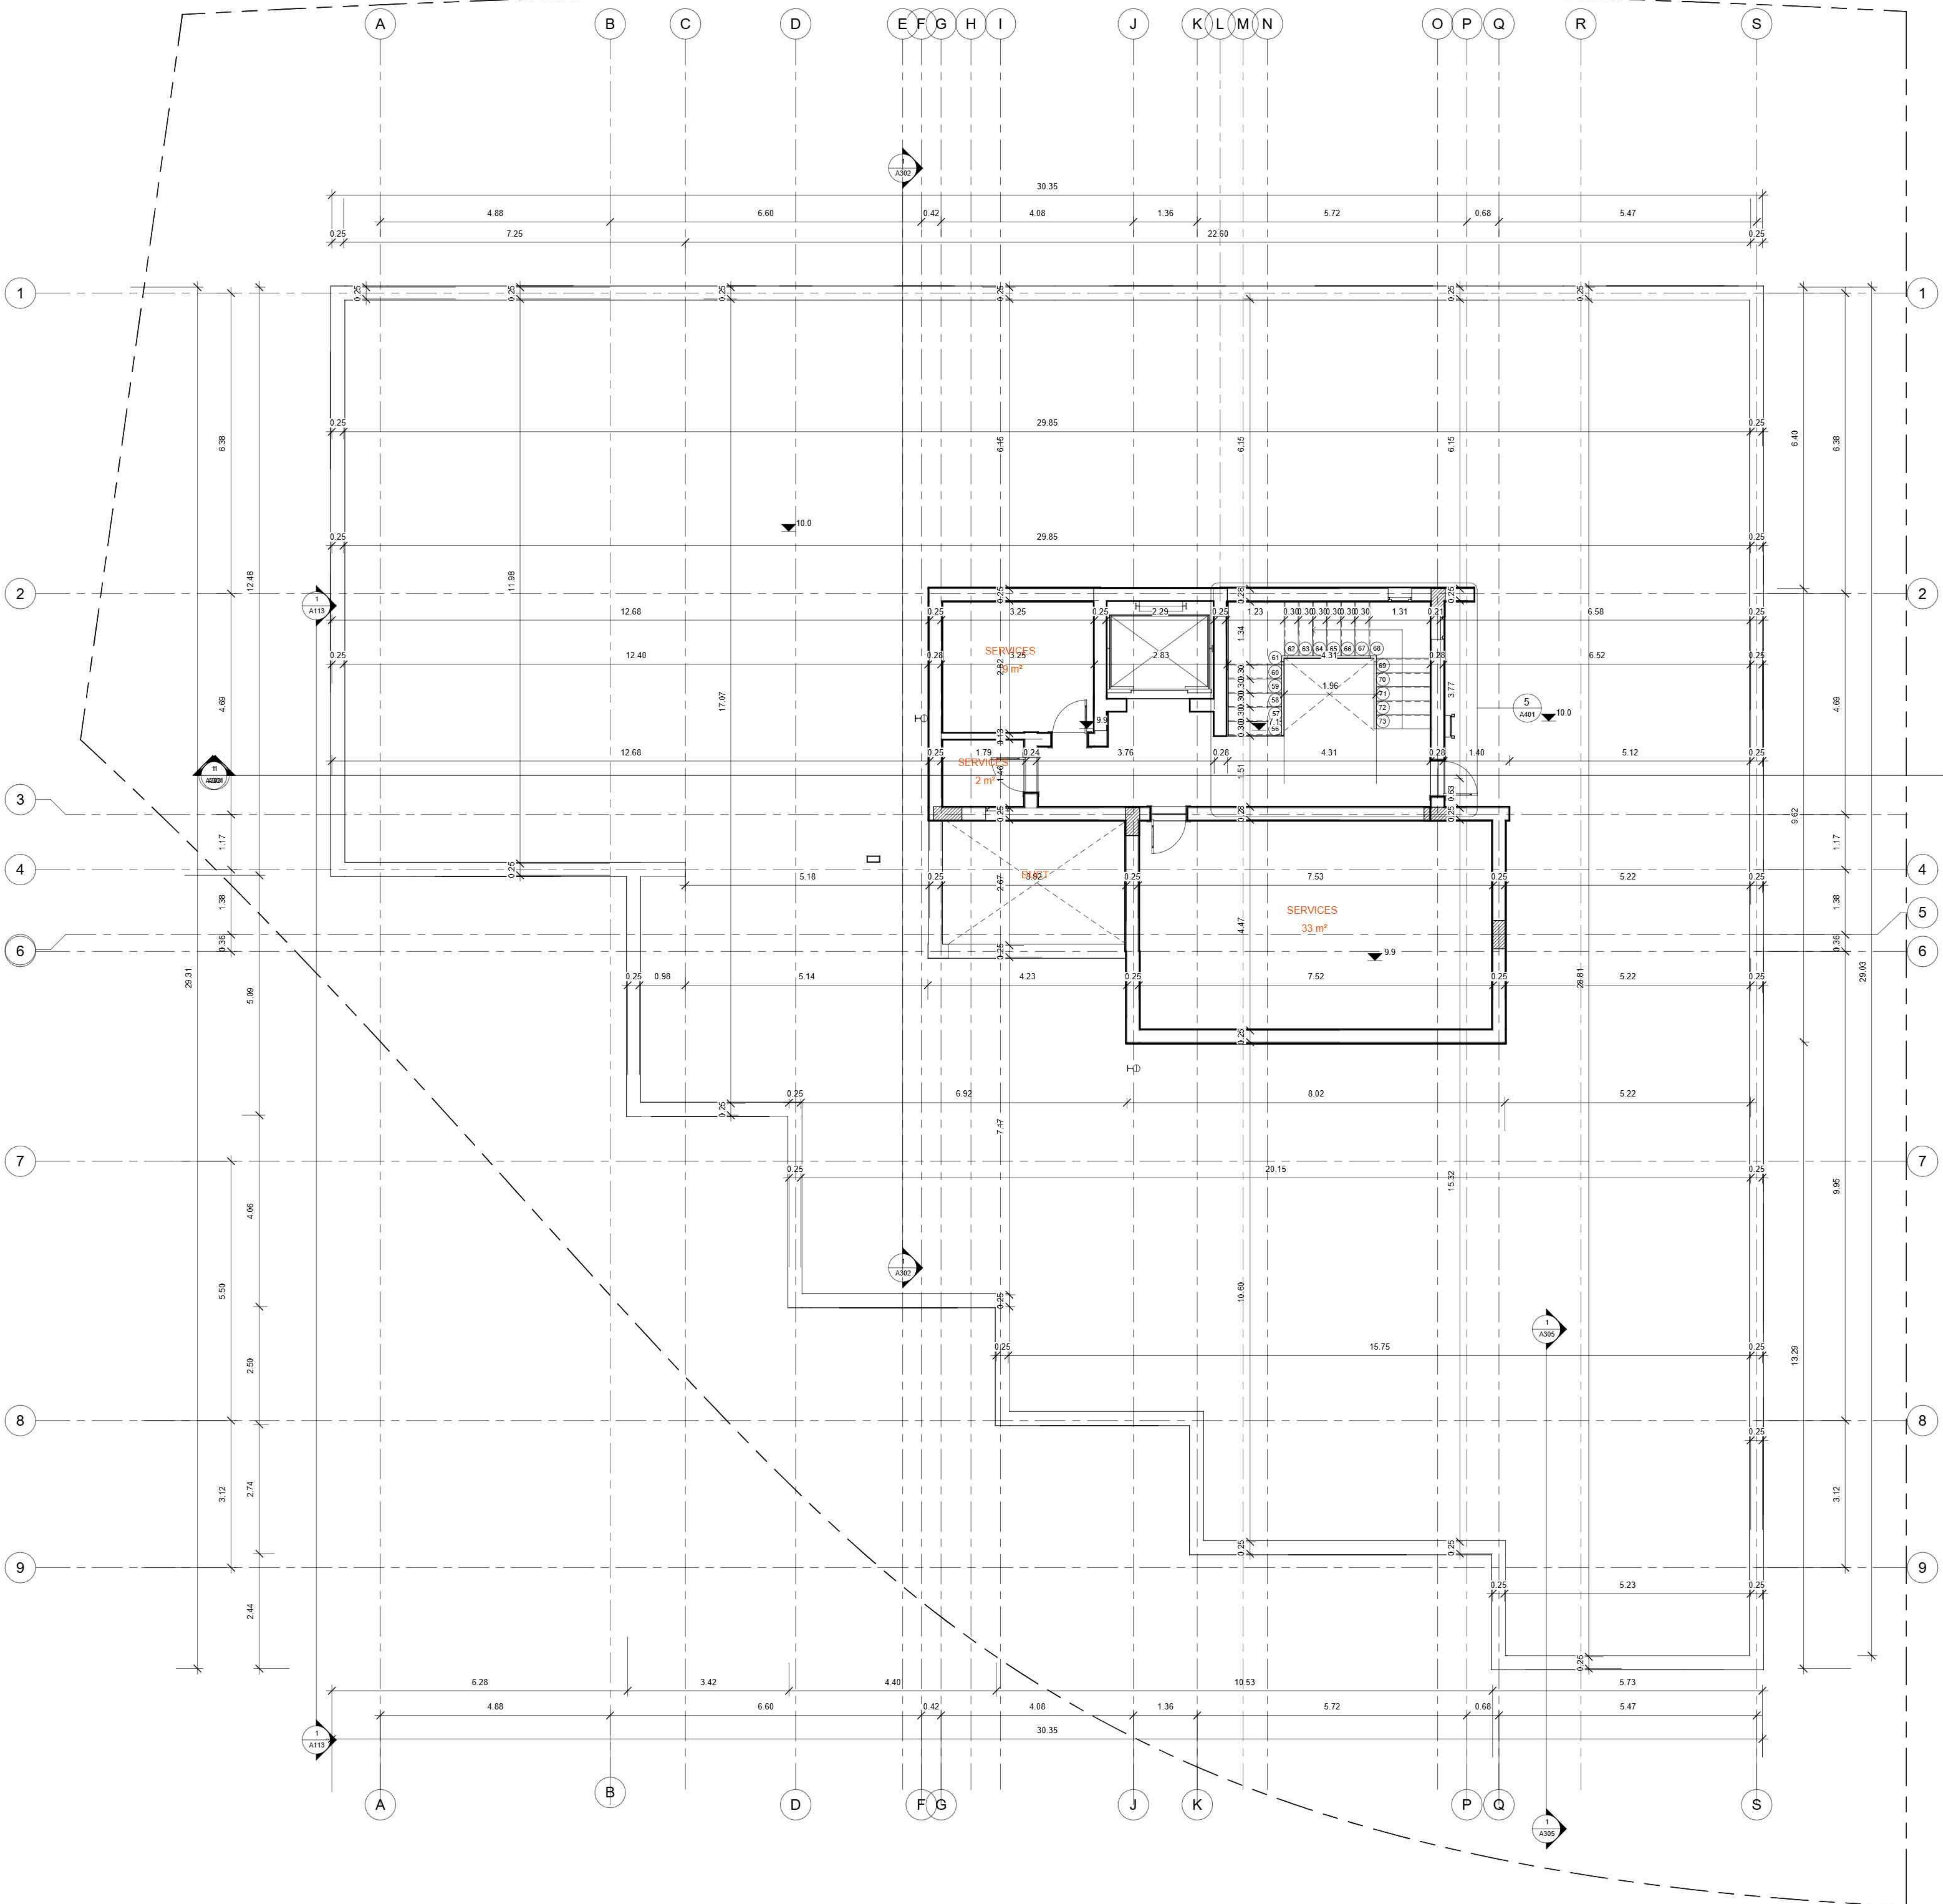


1 Roof Floor Plan
1 : 50

Course Info:
ASE 464
Working Drawings III

GENERAL NOTES:
- ALL MATERIALS & WORK PRACTICES SHALL COMPLY WITH, BUT NOT LIMITED TO THE BUILDING REGULATION 2019, THE NATIONAL CONSTRUCTION CODE of EGYPT UNLESS OTHERWISE SPECIFIED.
- ALL DIMENSIONS ARE IN METERS. IF IN DOUBT ASK, DO NOT SCALE.
- THESE DRAWINGS SHALL BE READ IN CONJUNCTION WITH ALL RELEVANT STRUCTURAL + ALL OTHER CONSULTANTS DRAWINGS/DETAILS & WITH ANY OTHER WRITTEN INSTRUCTIONS ISSUED IN THE COURSE OF THE CONTRACT.
- THESE DRAWINGS SHALL BE READ IN CONJUNCTION WITH ANY ENERGY RATING REPORT + SHALL BE CONSTRUCTED IN ACCORDANCE WITH THE STAMPED PLANS ENDORSED BY THE ACCREDITED THERMAL PERFORMANCE ASSESSOR WITHOUT ALTERATION

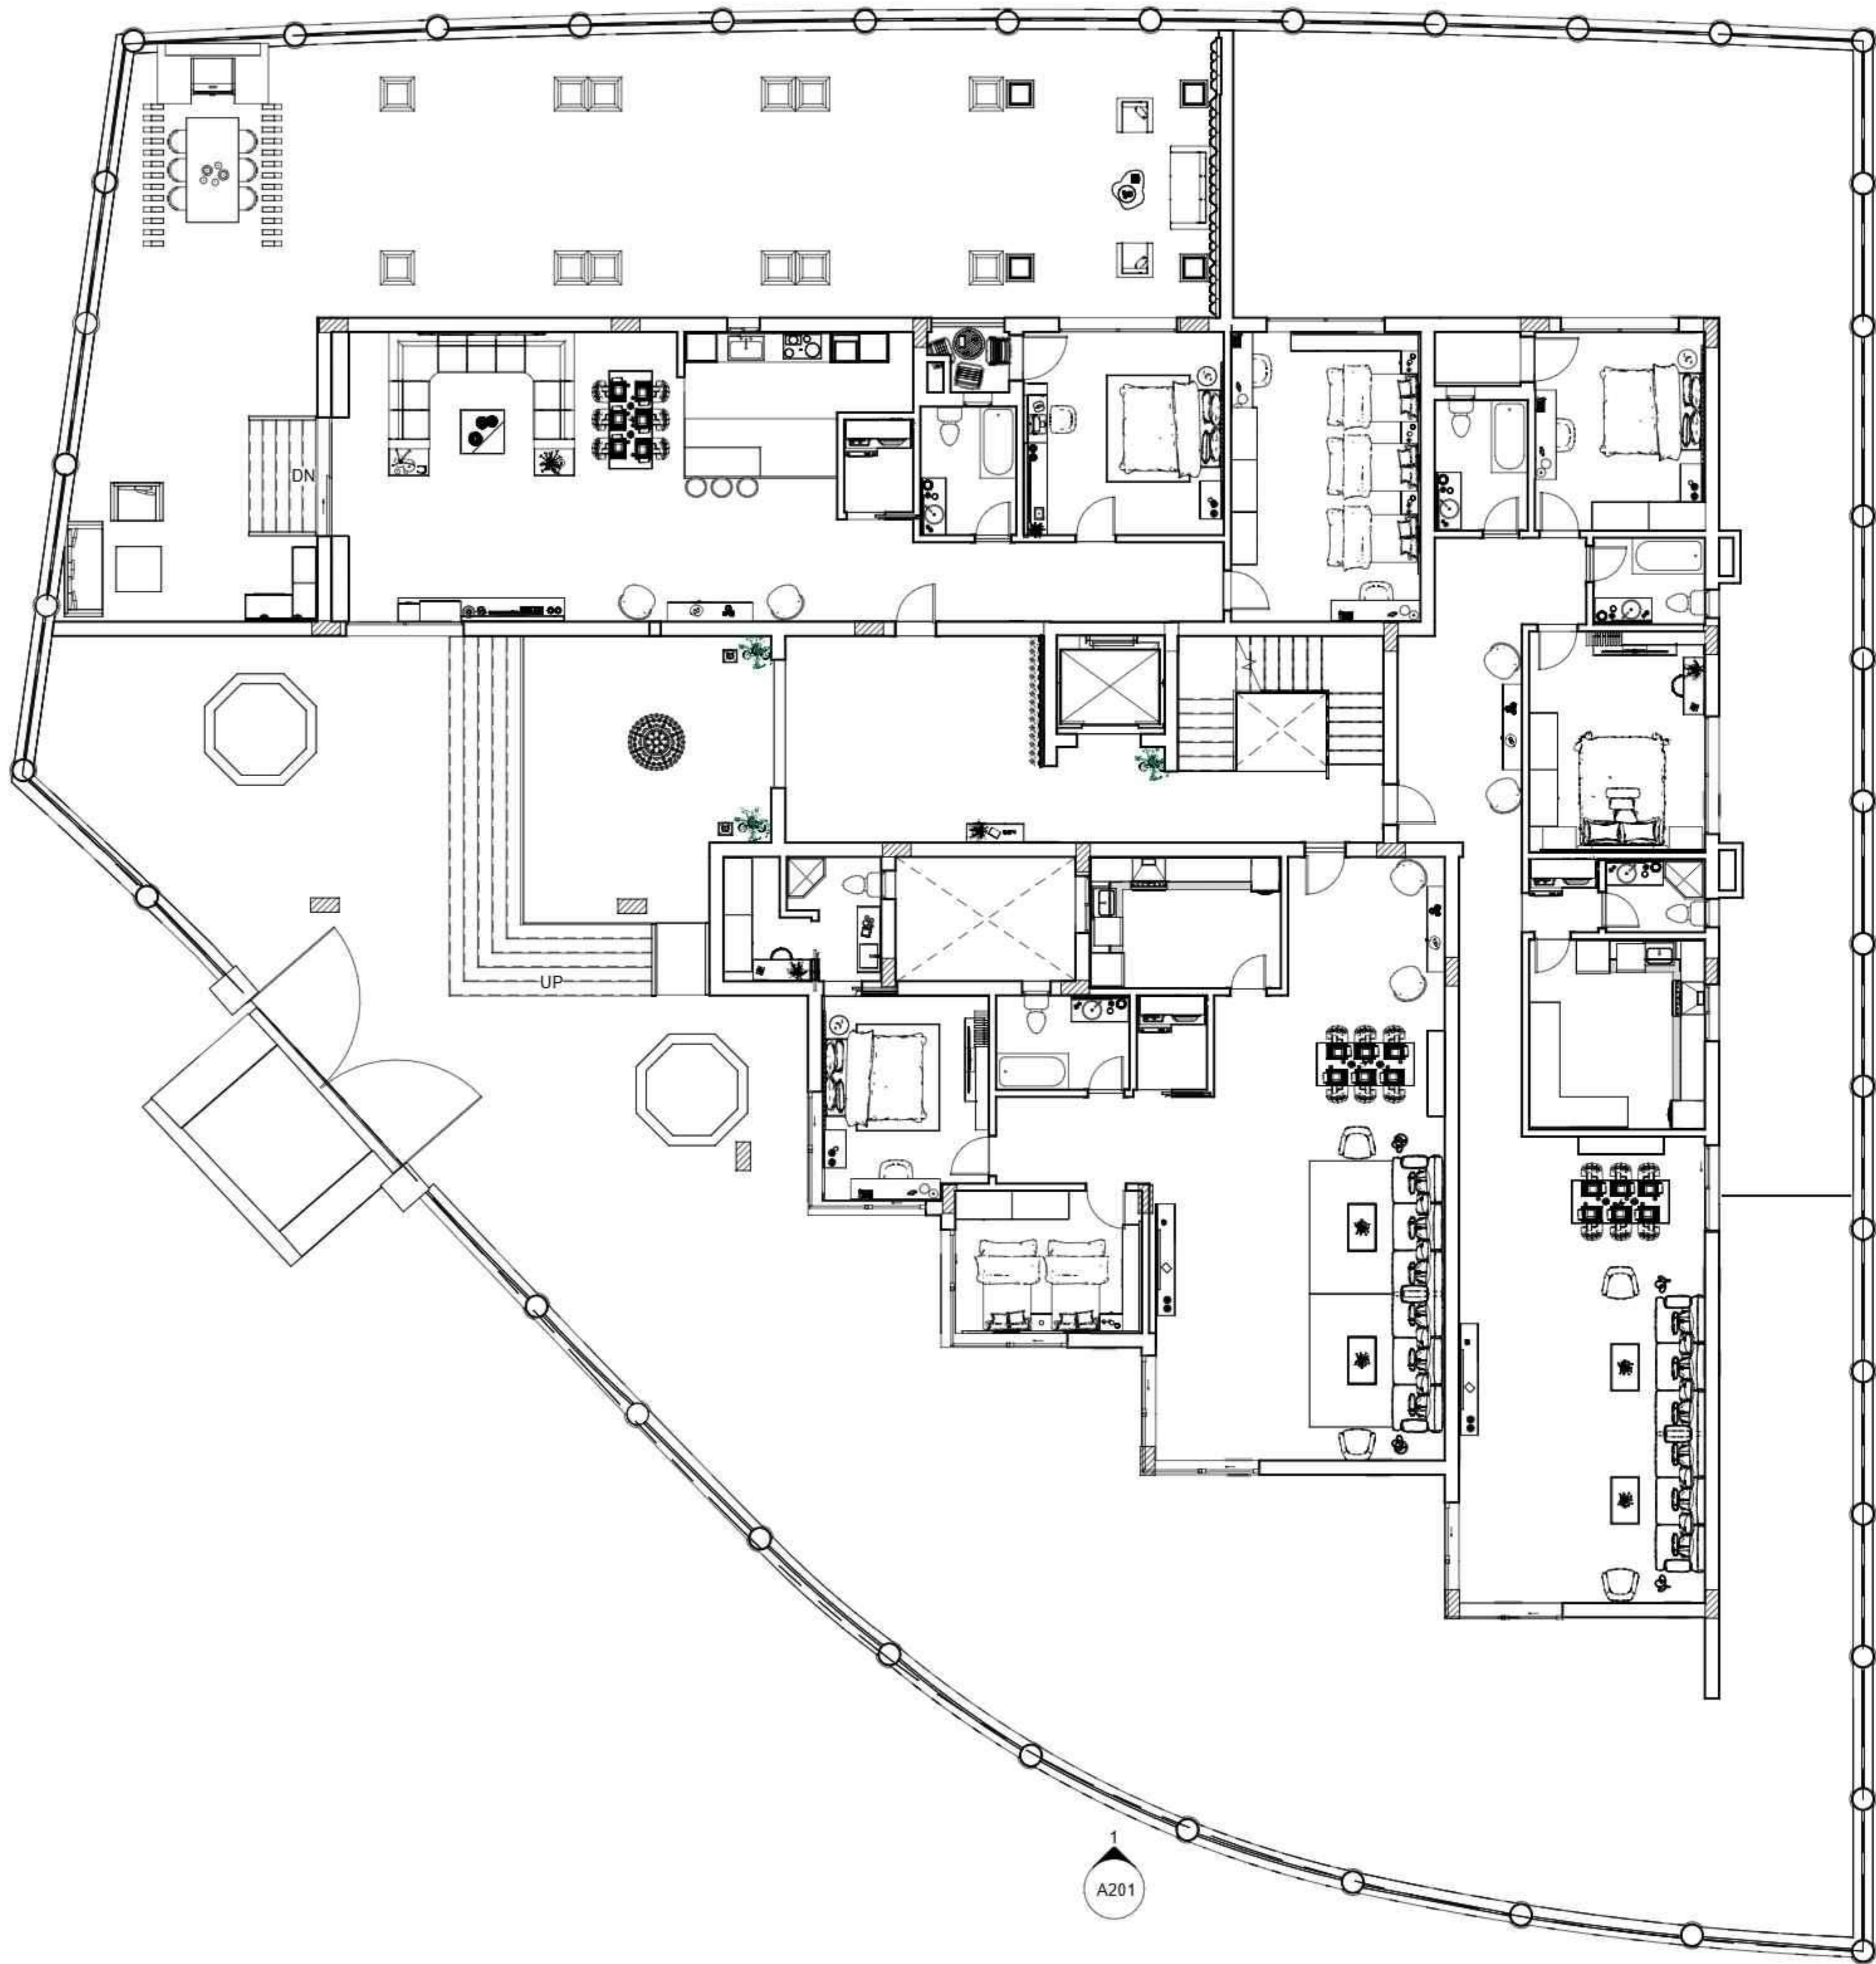

1 Ground Level Furnished
1 : 100

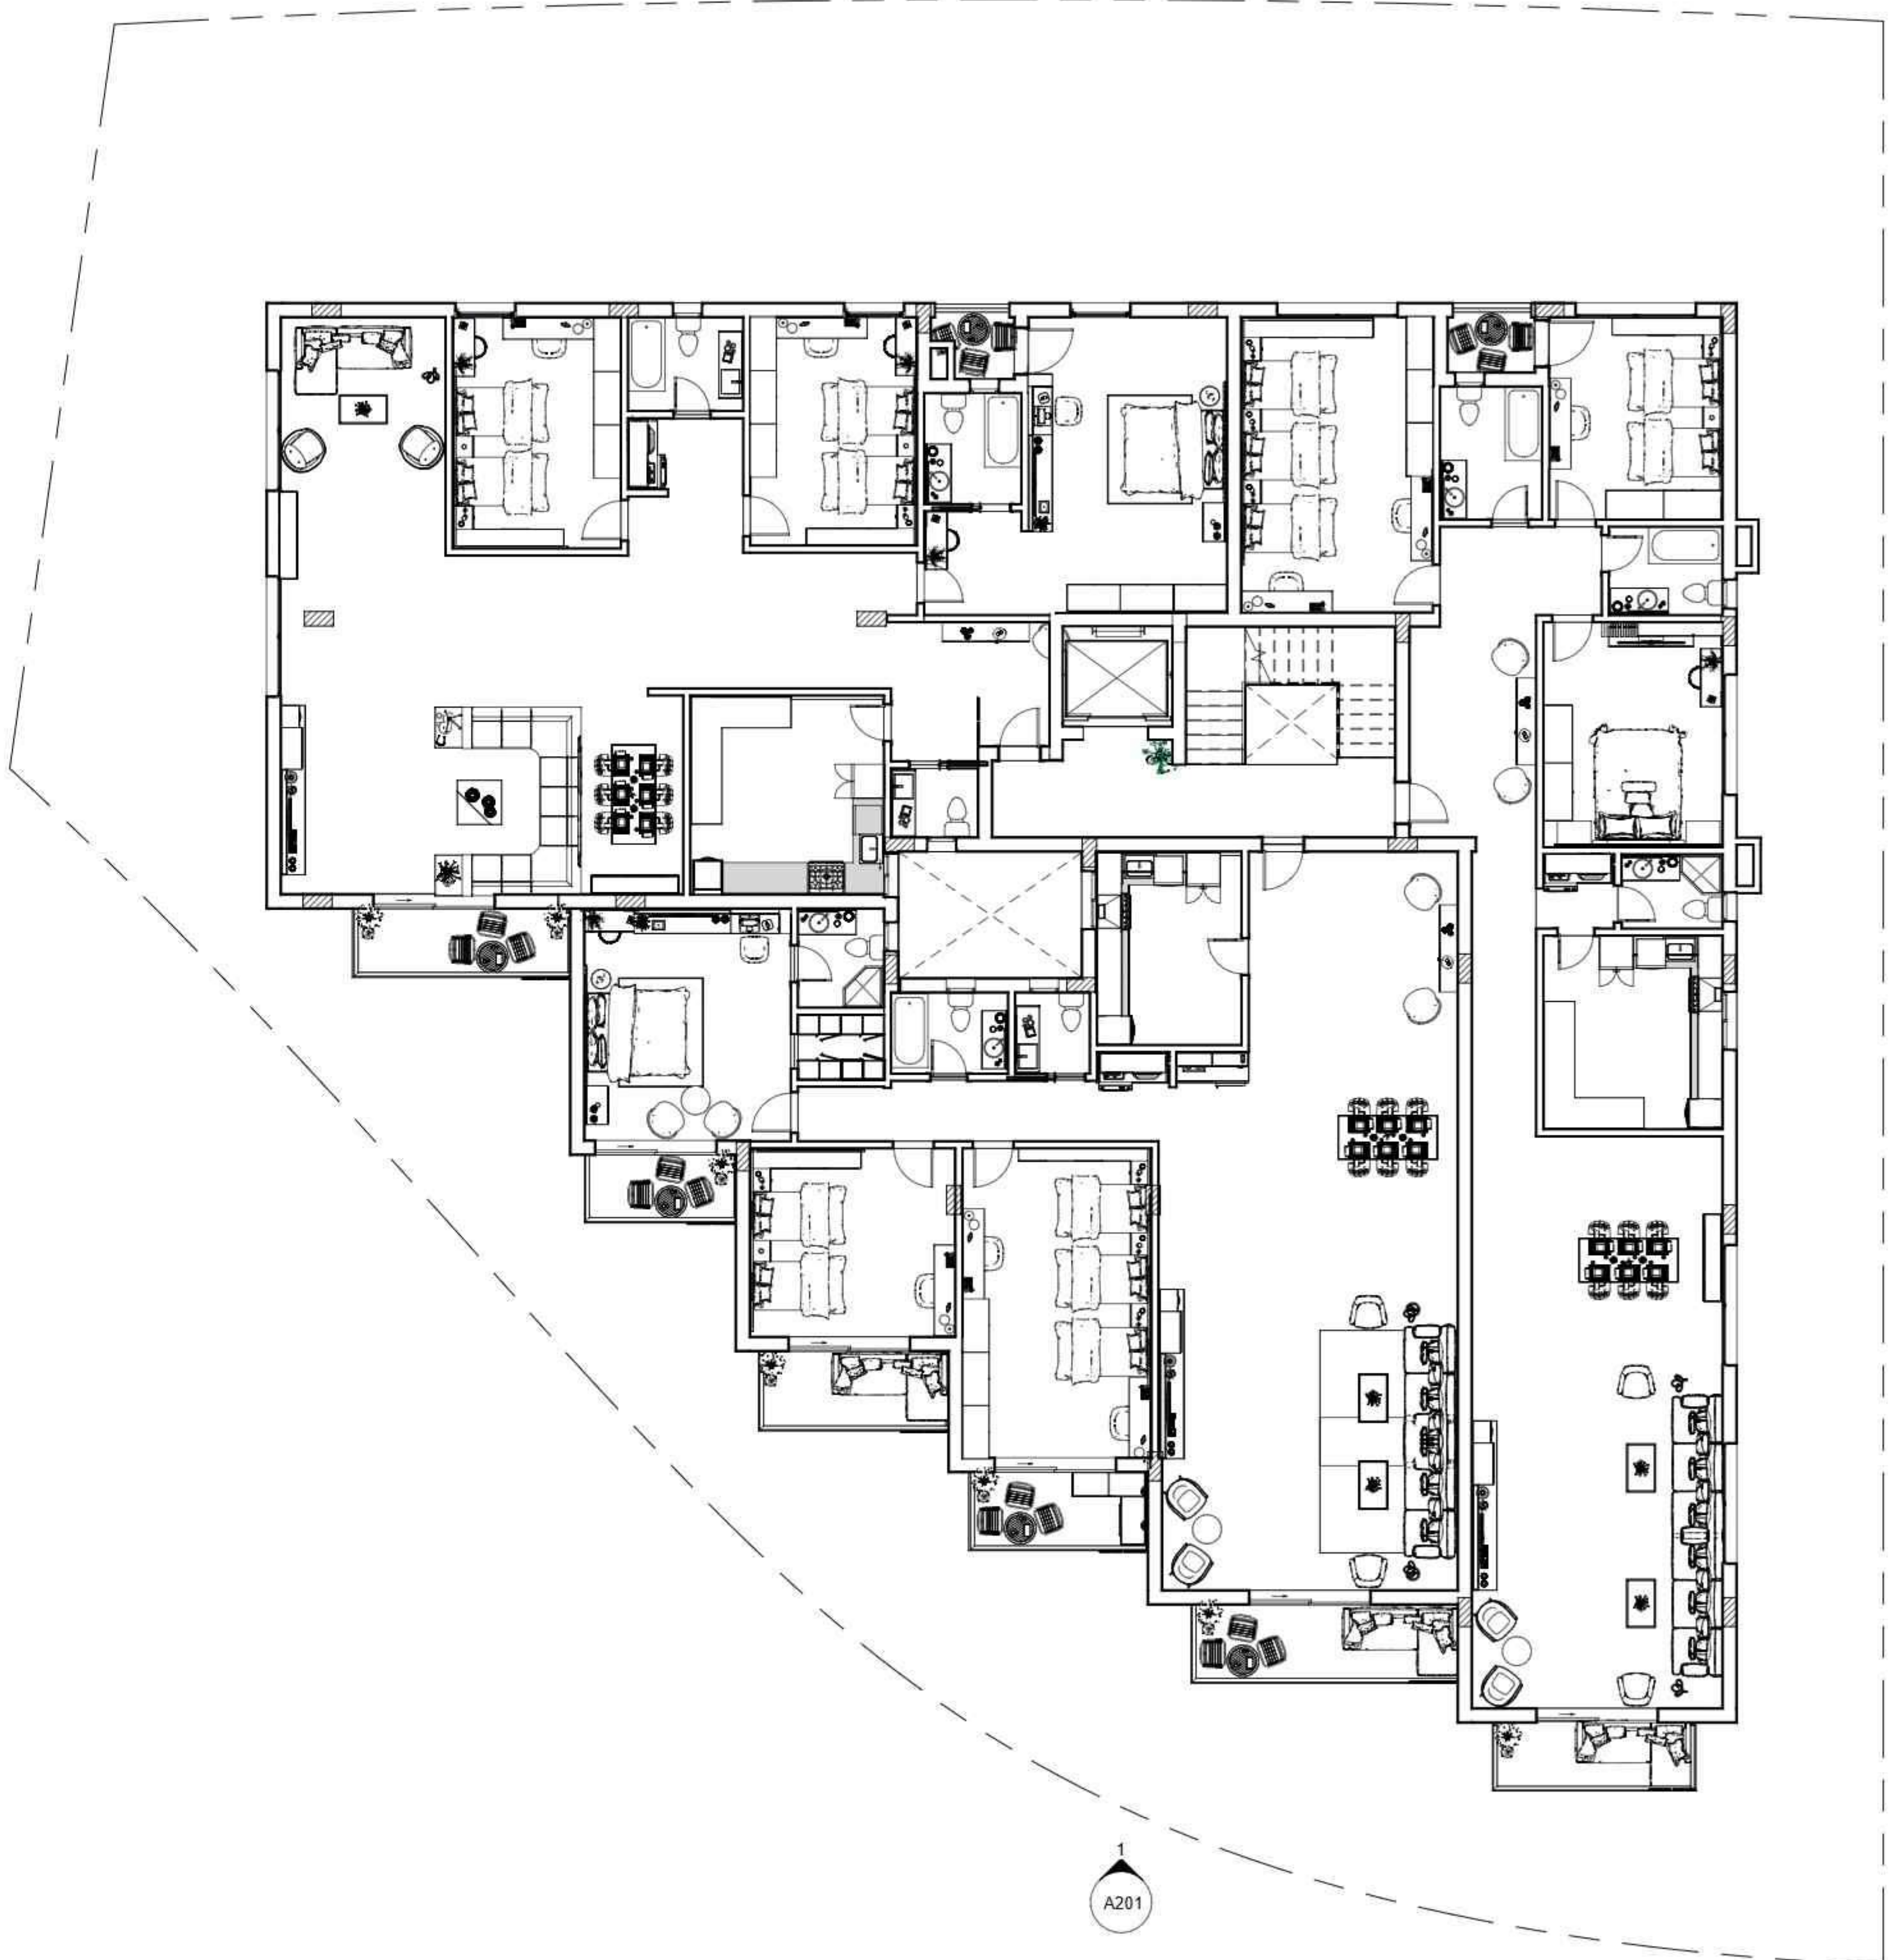

2 First Floor Furnished
1 : 100



OWNER:



OCTOBER UNIVERSITY
FOR MODERN SCIENCES & ARTS
Architectural Engineering Department
Spring 2025

CLIENTS NAME:
Dr. Tarek Galal
Eng. Hend
Eng. Nermeen
Eng. Yousra

Student Name: Hadeel Zakaria
ID: 220009

PROJECT NAME:
APARTMENT BUILDING

SHEET NAME:
ARCHITECTURAL PLANS

SHEET NO:	SCALE:
A108	1:100

DATE: 13-5-2025

GENERAL NOTES:

- ALL MATERIALS & WORK PRACTICES SHALL COMPLY WITH, BUT NOT LIMITED TO THE BUILDING REGULATION 2019, THE NATIONAL CONSTRUCTION CODE OF EGYPT UNLESS OTHERWISE SPECIFIED.

-ALL DIMENSIONS ARE IN METERS. IF IN DOUBT, DO NOT SCALE.

THESE DRAWINGS SHALL BE READ IN CONJUNCTION WITH ALL RELEVANT STRUCTURAL + ALL OTHER CONSULTANTS DRAWINGS/DETAILS & WITH ANY OTHER WRITTEN INSTRUCTIONS ISSUED IN THE COURSE OF THE CONTRACT.

- THESE DRAWINGS SHALL BE READ IN CONJUNCTION WITH ANY ENERGY RATING REPORT + SHALL BE CONSTRUCTED IN ACCORDANCE WITH THE STAMPED PLANS ENDORSED BY THE ACCREDITED THERMAL PERFORMANCE ASSESSOR WITHOUT ALTERATION



OWNER:



OCTOBER UNIVERSITY
FOR MODERN SCIENCES & ARTS
Architectural Engineering Department
Spring 2025

CLIENTS NAME:

Dr. Tarek Galal
Eng. Hend
Eng. Nermeen
Eng. Yousra


Student Name: Hadeel Zakari
ID: 220009

PROJECT NAME:
APARTMENT BUILDING

SHEET NAME:
MAIN & SIDE ELVATIONS:


SHEET NO:	SCALE:
A201	1:50

DATE: 13-5-2025

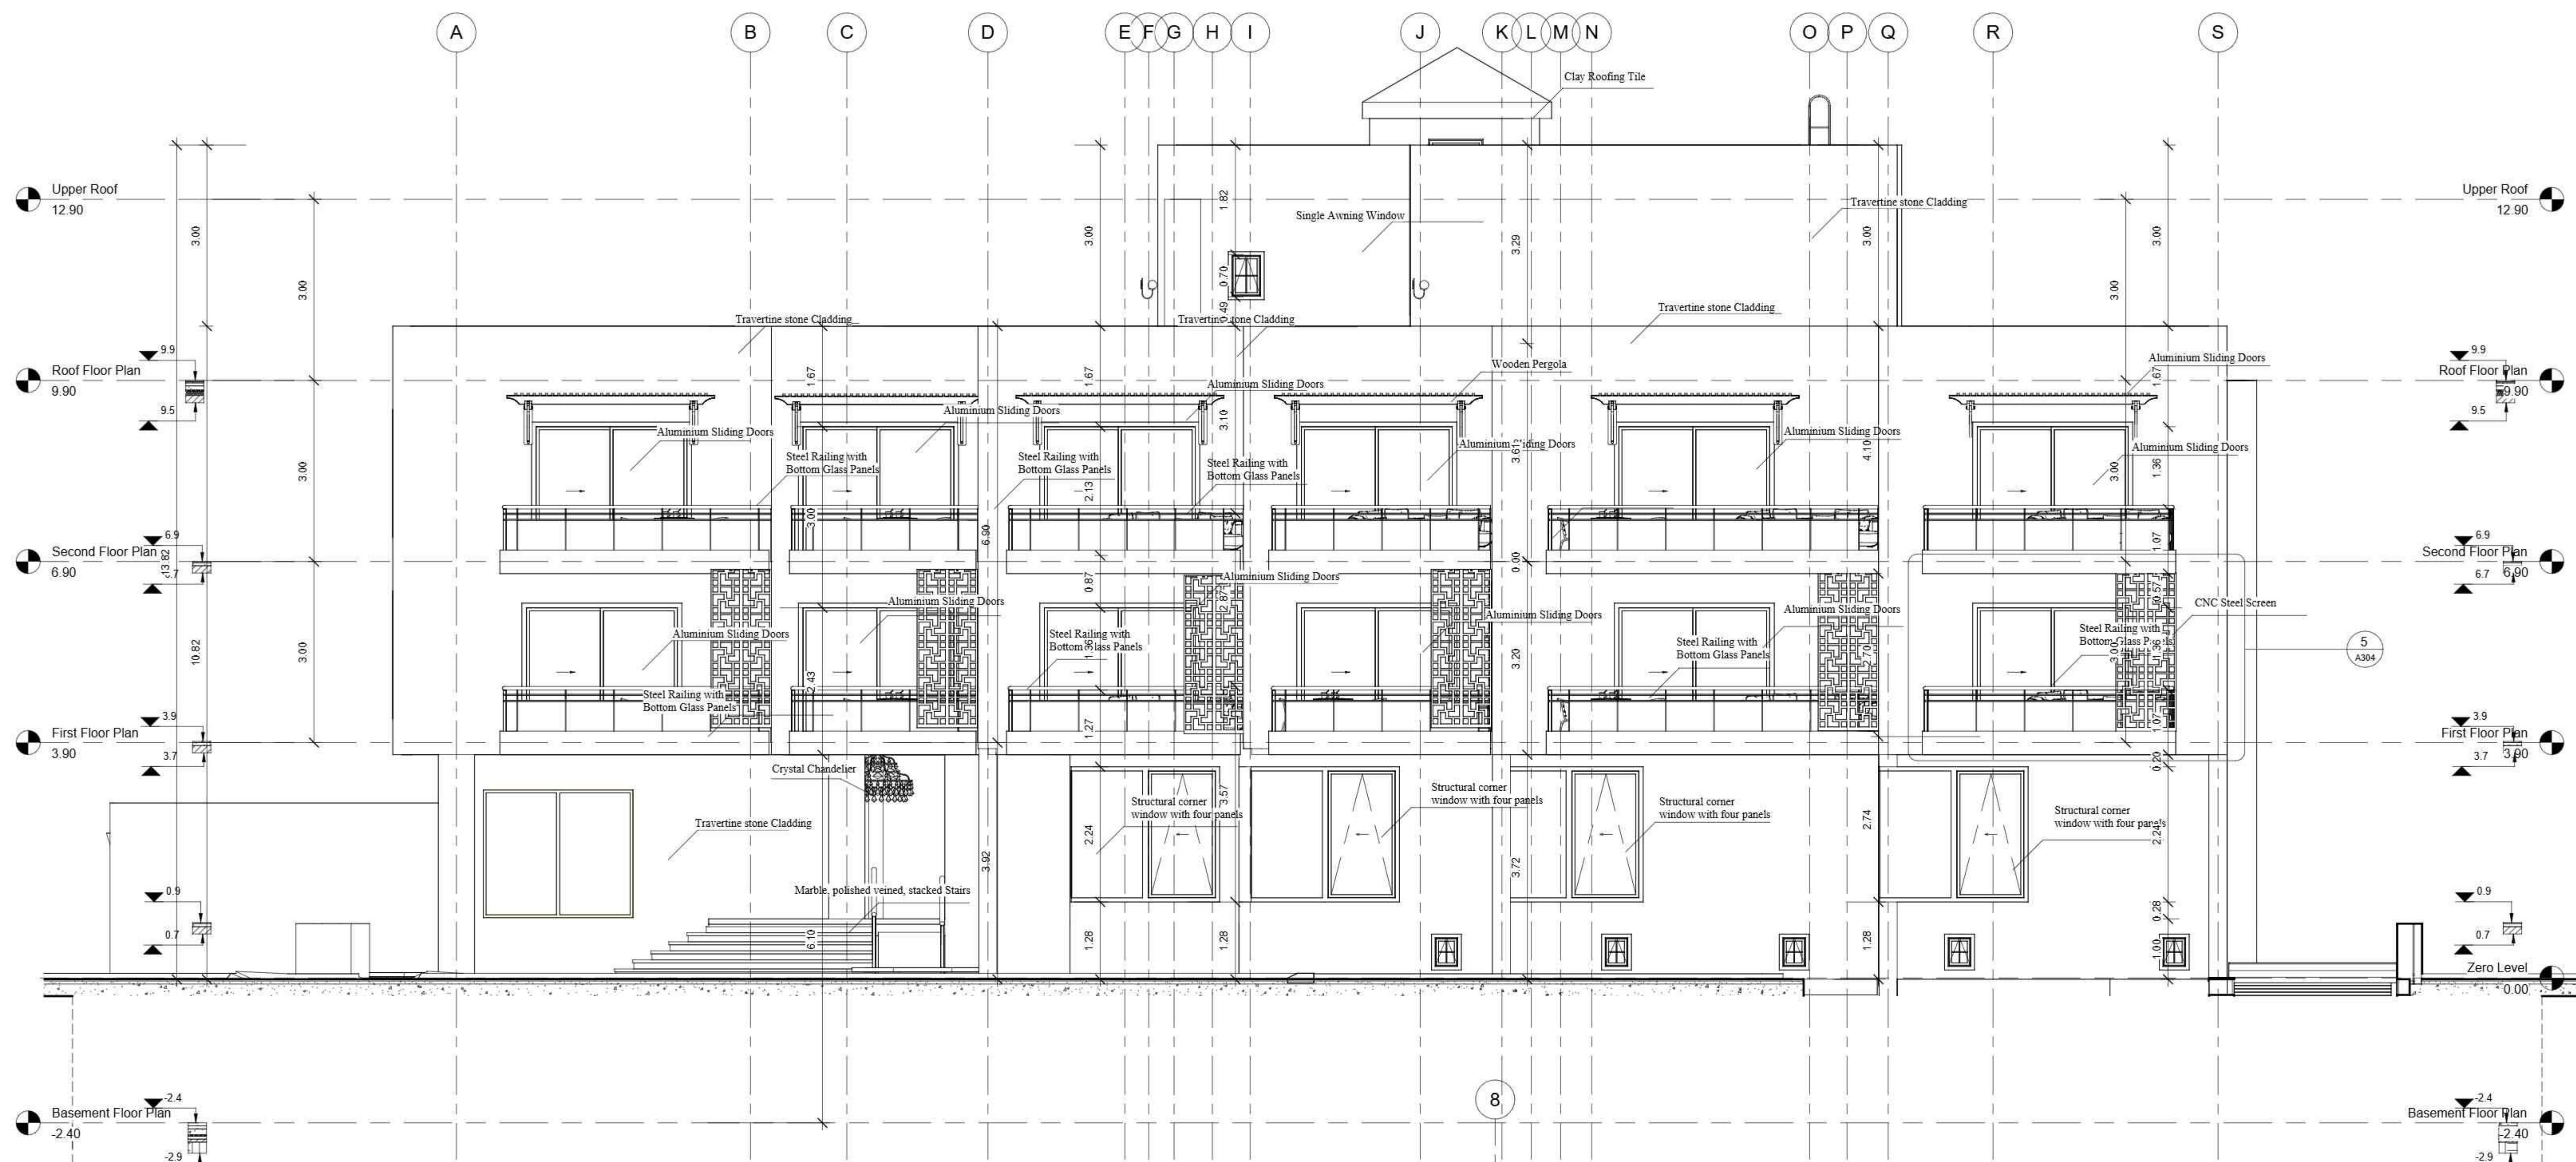


1 Main Elevation (South)

1 : 50

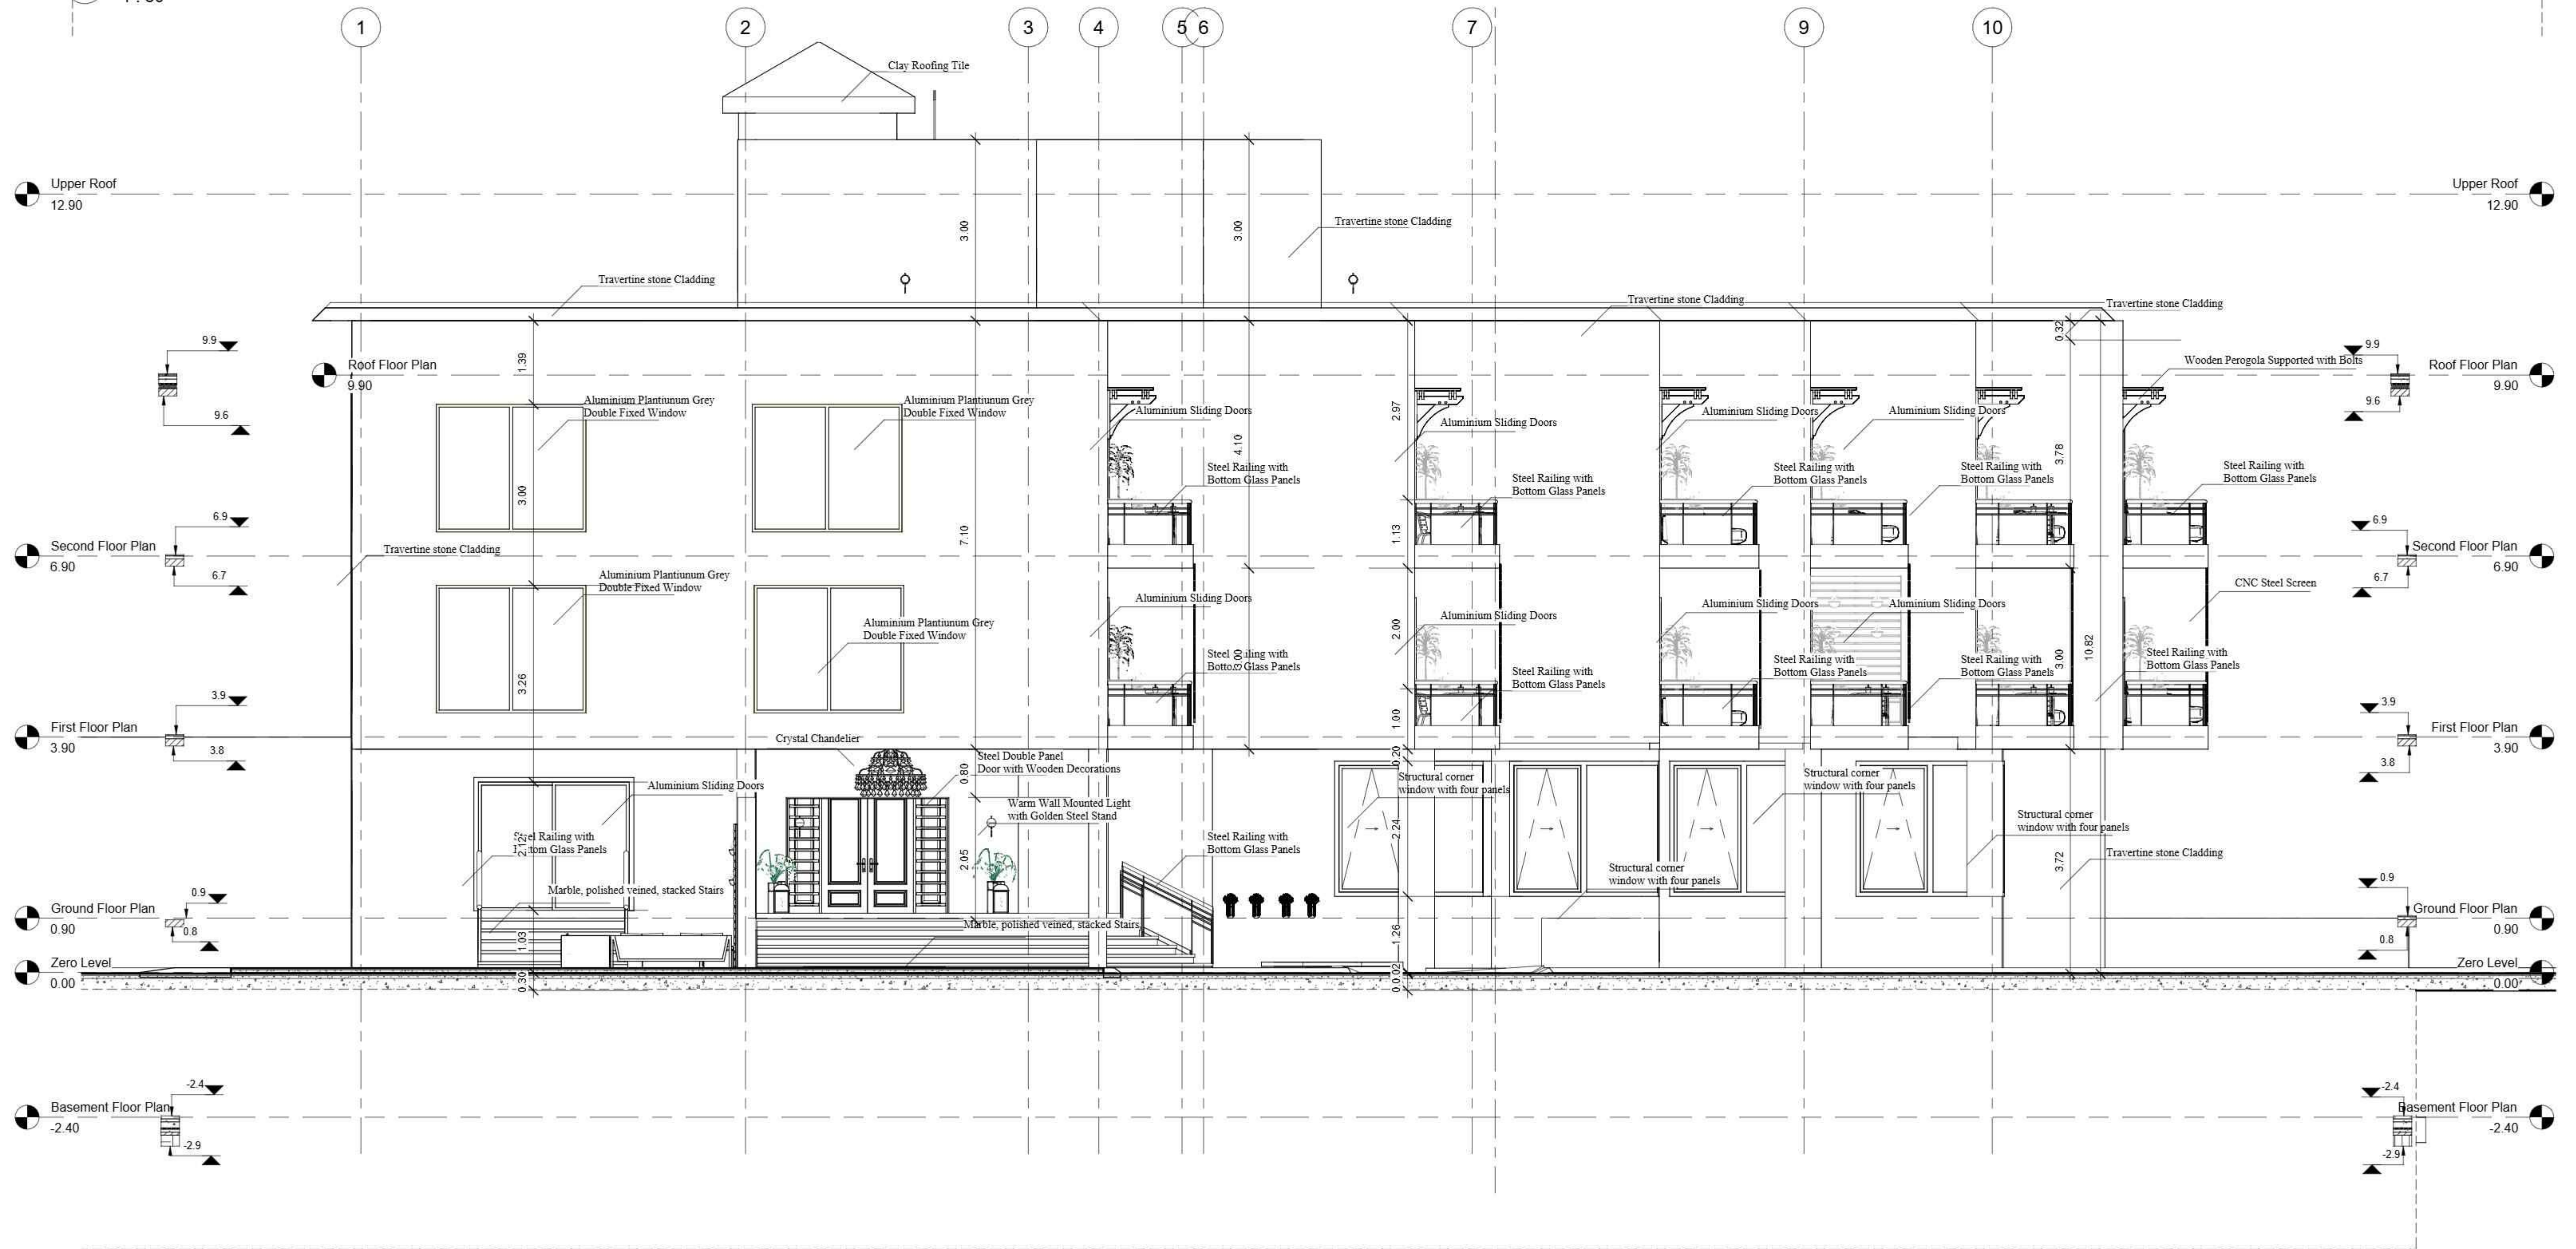

Side Elevation (West)

1 : 50

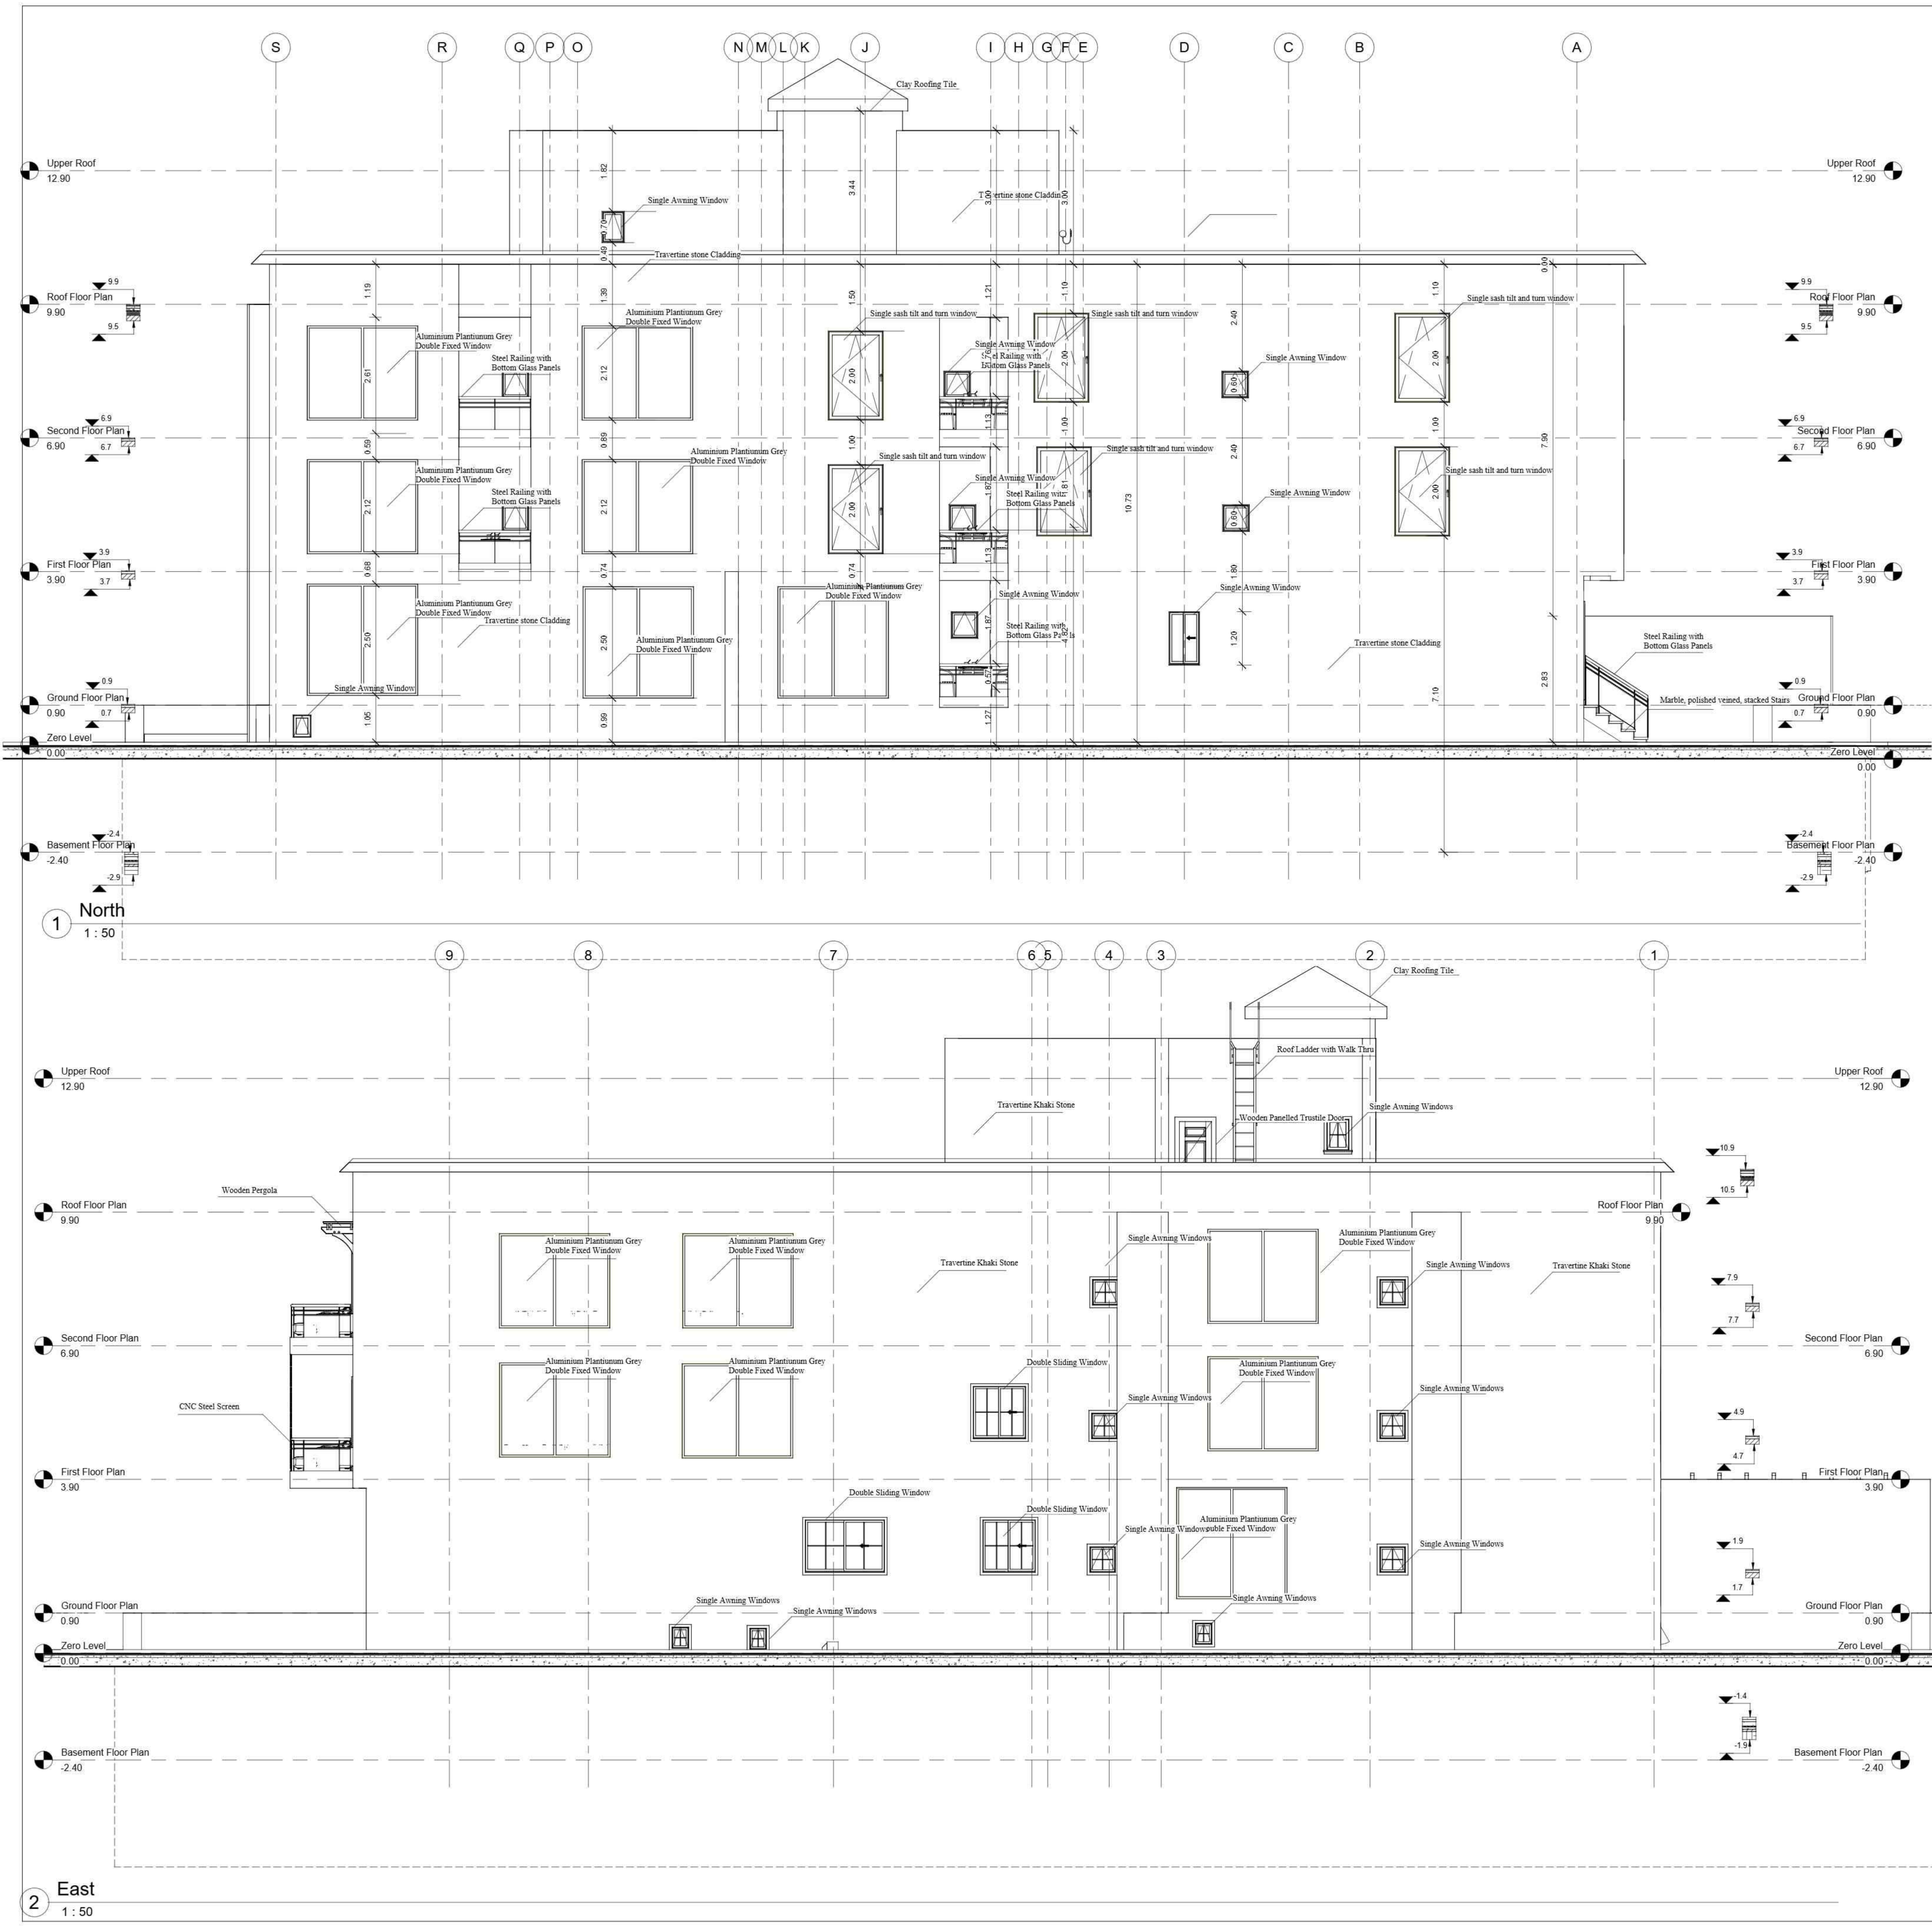

Course Info:
ASE 464
Working Drawings III

GENERAL NOTES:
- ALL MATERIALS & WORK PRACTICES SHALL COMPLY WITH, BUT NOT LIMITED TO THE BUILDING REGULATION 2019, THE NATIONAL CONSTRUCTION CODE OF EGYPT UNLESS OTHERWISE SPECIFIED.
- ALL DIMENSIONS ARE IN METERS. IF IN DOUBT ASK, DO NOT SCALE.
- THESE DRAWINGS SHALL BE READ IN CONJUNCTION WITH ALL RELEVANT STRUCTURAL + ALL OTHER CONSULTANTS DRAWINGS/DETAILS & WITH ANY OTHER WRITTEN INSTRUCTIONS ISSUED IN THE COURSE OF THE CONTRACT.
- THESE DRAWINGS SHALL BE READ IN CONJUNCTION WITH ANY ENERGY RATING REPORT + SHALL BE CONSTRUCTED IN ACCORDANCE WITH THE STAMPED PLANS ENDORSED BY THE ACCREDITED THERMAL PERFORMANCE ASSESSOR WITHOUT ALTERATION



OWNER:



OCTOBER UNIVERSITY
FOR MODERN SCIENCES & ARTS
Architectural Engineering Department
Spring 2025

CLIENTS NAME:
Dr. Tarek Galal
Eng. Hend
Eng. Nermeen
Eng. Yousra

Student Name: Hadeel Zakaria
ID: 220009

PROJECT NAME:
APARTMENT BUILDING

SHEET NAME:
SIDE & BACK ELEVATIONS

SHEET NO: A202
SCALE: 1:50

DATE: 13-5-2025

- ALL MATERIALS & WORK PRACTICES SHALL COMPLY WITH, BUT NOT LIMITED TO THE BUILDING REGULATION 2019, THE NATIONAL CONSTRUCTION CODE of EGYPT UNLESS OTHERWISE SPECIFIED.

-THESE DRAWINGS SHALL BE READ IN CONJUNCTION WITH ALL RELEVANT STRUCTURAL + ALL OTHER CONSULTANTS DRAWINGS/DETAILS + WITH ANY OTHER WRITTEN INSTRUCTIONS ISSUED IN THE COURSE OF THE CONTRACT.

- THESE DRAWINGS SHALL BE READ IN CONJUNCTION WITH ANY ENERGY RATING REPORT + SHALL BE CONSTRUCTED IN ACCORDANCE WITH THE STAMPED PLANS ENDORSED BY THE ACCREDITED THERMAL PERFORMANCE ASSESSOR WITHOUT ALTERATION


UNIVERSITY of
GREENWICH

CLIENTS NAME:
Dr. Tarek Galal
Eng. Hend
Eng. Nermeen
Eng. Yousra

PROJECT NAME:
APARTMENT BUILDING

SHEET NO:	SCALE:
A301	1:50

DATE: 13-5-2025

Main Section
1 : 50

Course Info:
ASE 464
Working Drawings III


GENERAL NOTES:

- ALL MATERIALS & WORK PRACTICES SHALL COMPLY WITH, BUT NOT LIMITED TO THE BUILDING REGULATION 2019, THE NATIONAL CONSTRUCTION CODE of EGYPT UNLESS OTHERWISE SPECIFIED.

- ALL DIMENSIONS ARE IN METERS. IF IN DOUBT ASK, DO NOT SCALE.

- THESE DRAWINGS SHALL BE READ IN CONJUNCTION WITH ALL RELEVANT STRUCTURAL + ALL OTHER CONSULTANTS DRAWINGS/DETAILS & WITH ANY OTHER WRITTEN INSTRUCTIONS ISSUED IN THE COURSE OF THE CONTRACT.

- THESE DRAWINGS SHALL BE READ IN CONJUNCTION WITH ANY ENERGY RATING REPORT + SHALL BE CONSTRUCTED IN ACCORDANCE WITH THE STAMPED PLANS ENDORSED BY THE ACCREDITED THERMAL PERFORMANCE ASSESSOR WITHOUT ALTERATION

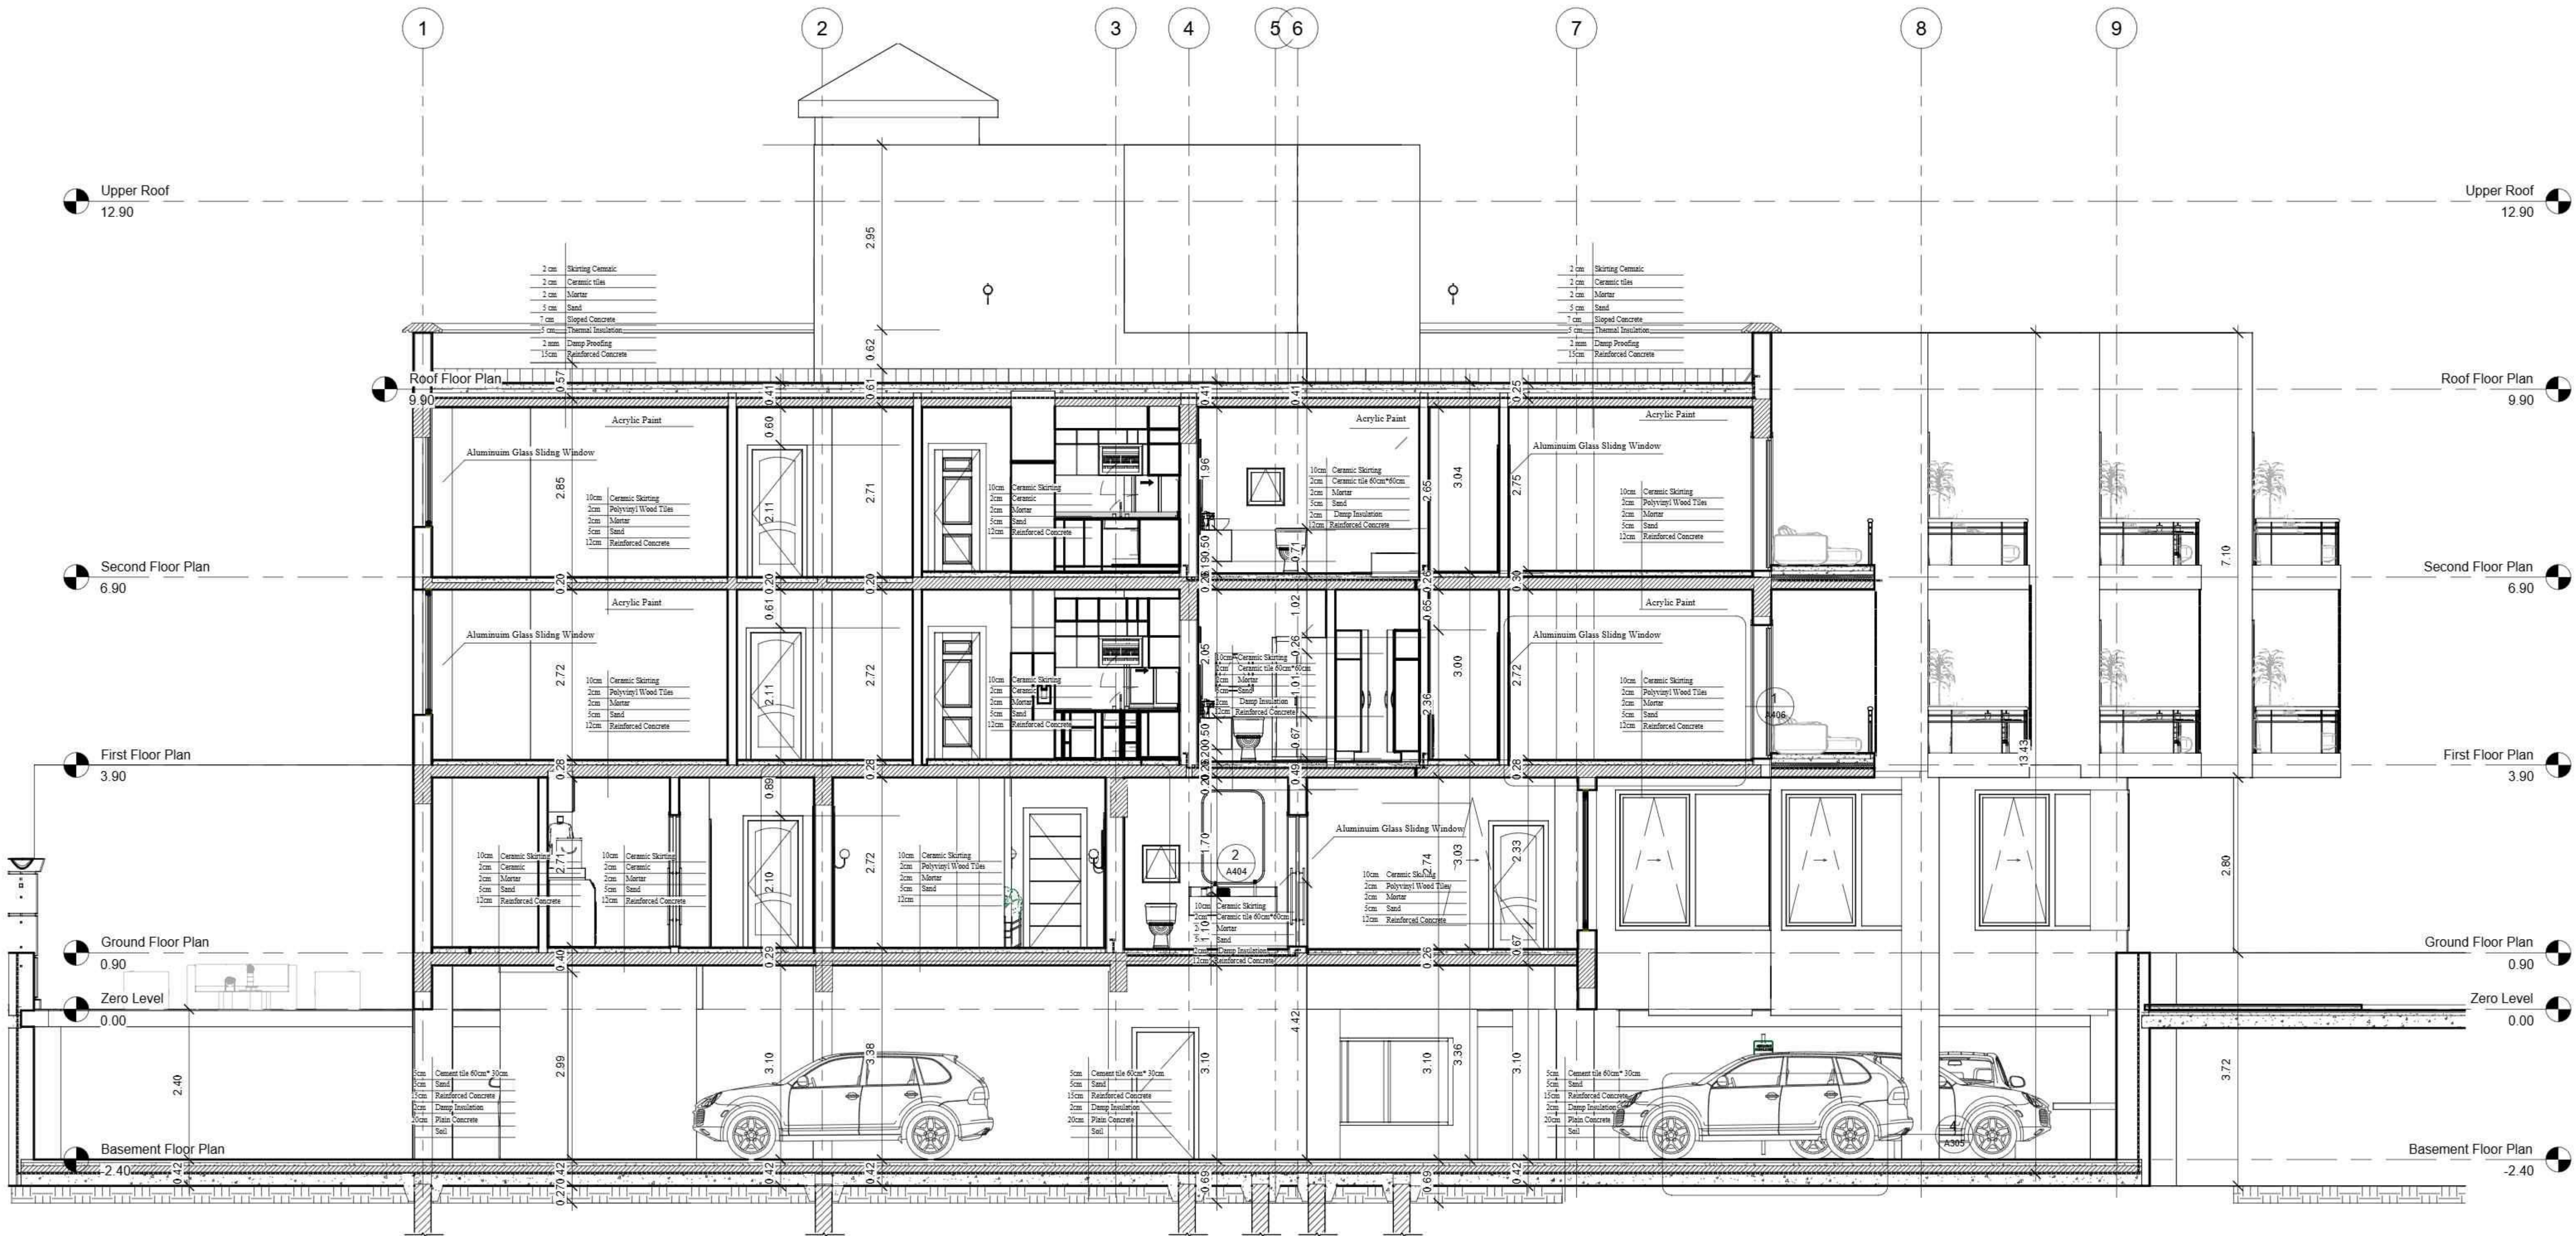

1 Side Section
1 : 50



OWNER:



OCTOBER UNIVERSITY
FOR MODERN SCIENCES & ARTS
Architectural Engineering Department
Spring 2025

CLIENTS NAME:

Dr. Tarek Galal
Eng. Hend
Eng. Nermeen
Eng. Yousra

Student Name: Hadeel Zakaria
ID: 220009

PROJECT NAME:
APARTMENT BUILDING

SHEET NAME:
SIDE SECTION

SHEET NO: A302
SCALE: 1:50

DATE: 13-5-2025

Course Info:
ASE 464
Working Drawings III

GENERAL NOTES:

- ALL MATERIALS & WORK PRACTICES SHALL COMPLY WITH, BUT NOT LIMITED TO THE BUILDING REGULATION 2019, THE NATIONAL CONSTRUCTION CODE OF EGYPT UNLESS OTHERWISE SPECIFIED.

- ALL DIMENSIONS ARE IN METERS. IF IN DOUBT ASK, DO NOT SCALE.

- THESE DRAWINGS SHALL BE READ IN CONJUNCTION WITH ALL RELEVANT STRUCTURAL + ALL OTHER CONSULTANTS DRAWINGS/DETAILS & WITH ANY OTHER WRITTEN INSTRUCTIONS ISSUED IN THE COURSE OF THE CONTRACT.

- THESE DRAWINGS SHALL BE READ IN CONJUNCTION WITH ANY ENERGY RATING REPORT + SHALL BE CONSTRUCTED IN ACCORDANCE WITH THE STAMPED PLANS ENDORSED BY THE ACCREDITED THERMAL PERFORMANCE ASSESSOR WITHOUT ALTERATION.



OWNER:

OCTOBER UNIVERSITY
FOR MODERN SCIENCES & ARTS
Architectural Engineering Department
Spring 2025

CLIENTS NAME:

Dr. Tarek Galal
Eng. Hend
Eng. Nermeen
Eng. Yousra








Student Name: Hadeel Zakaria
ID: 220009

PROJECT NAME:
APARTMENT BUILDING

SHEET NAME:
WALL SECTION 2 &
DETAILS

SHEET NO: A304
SCALE: 1:25

DATE: 13-5-2025

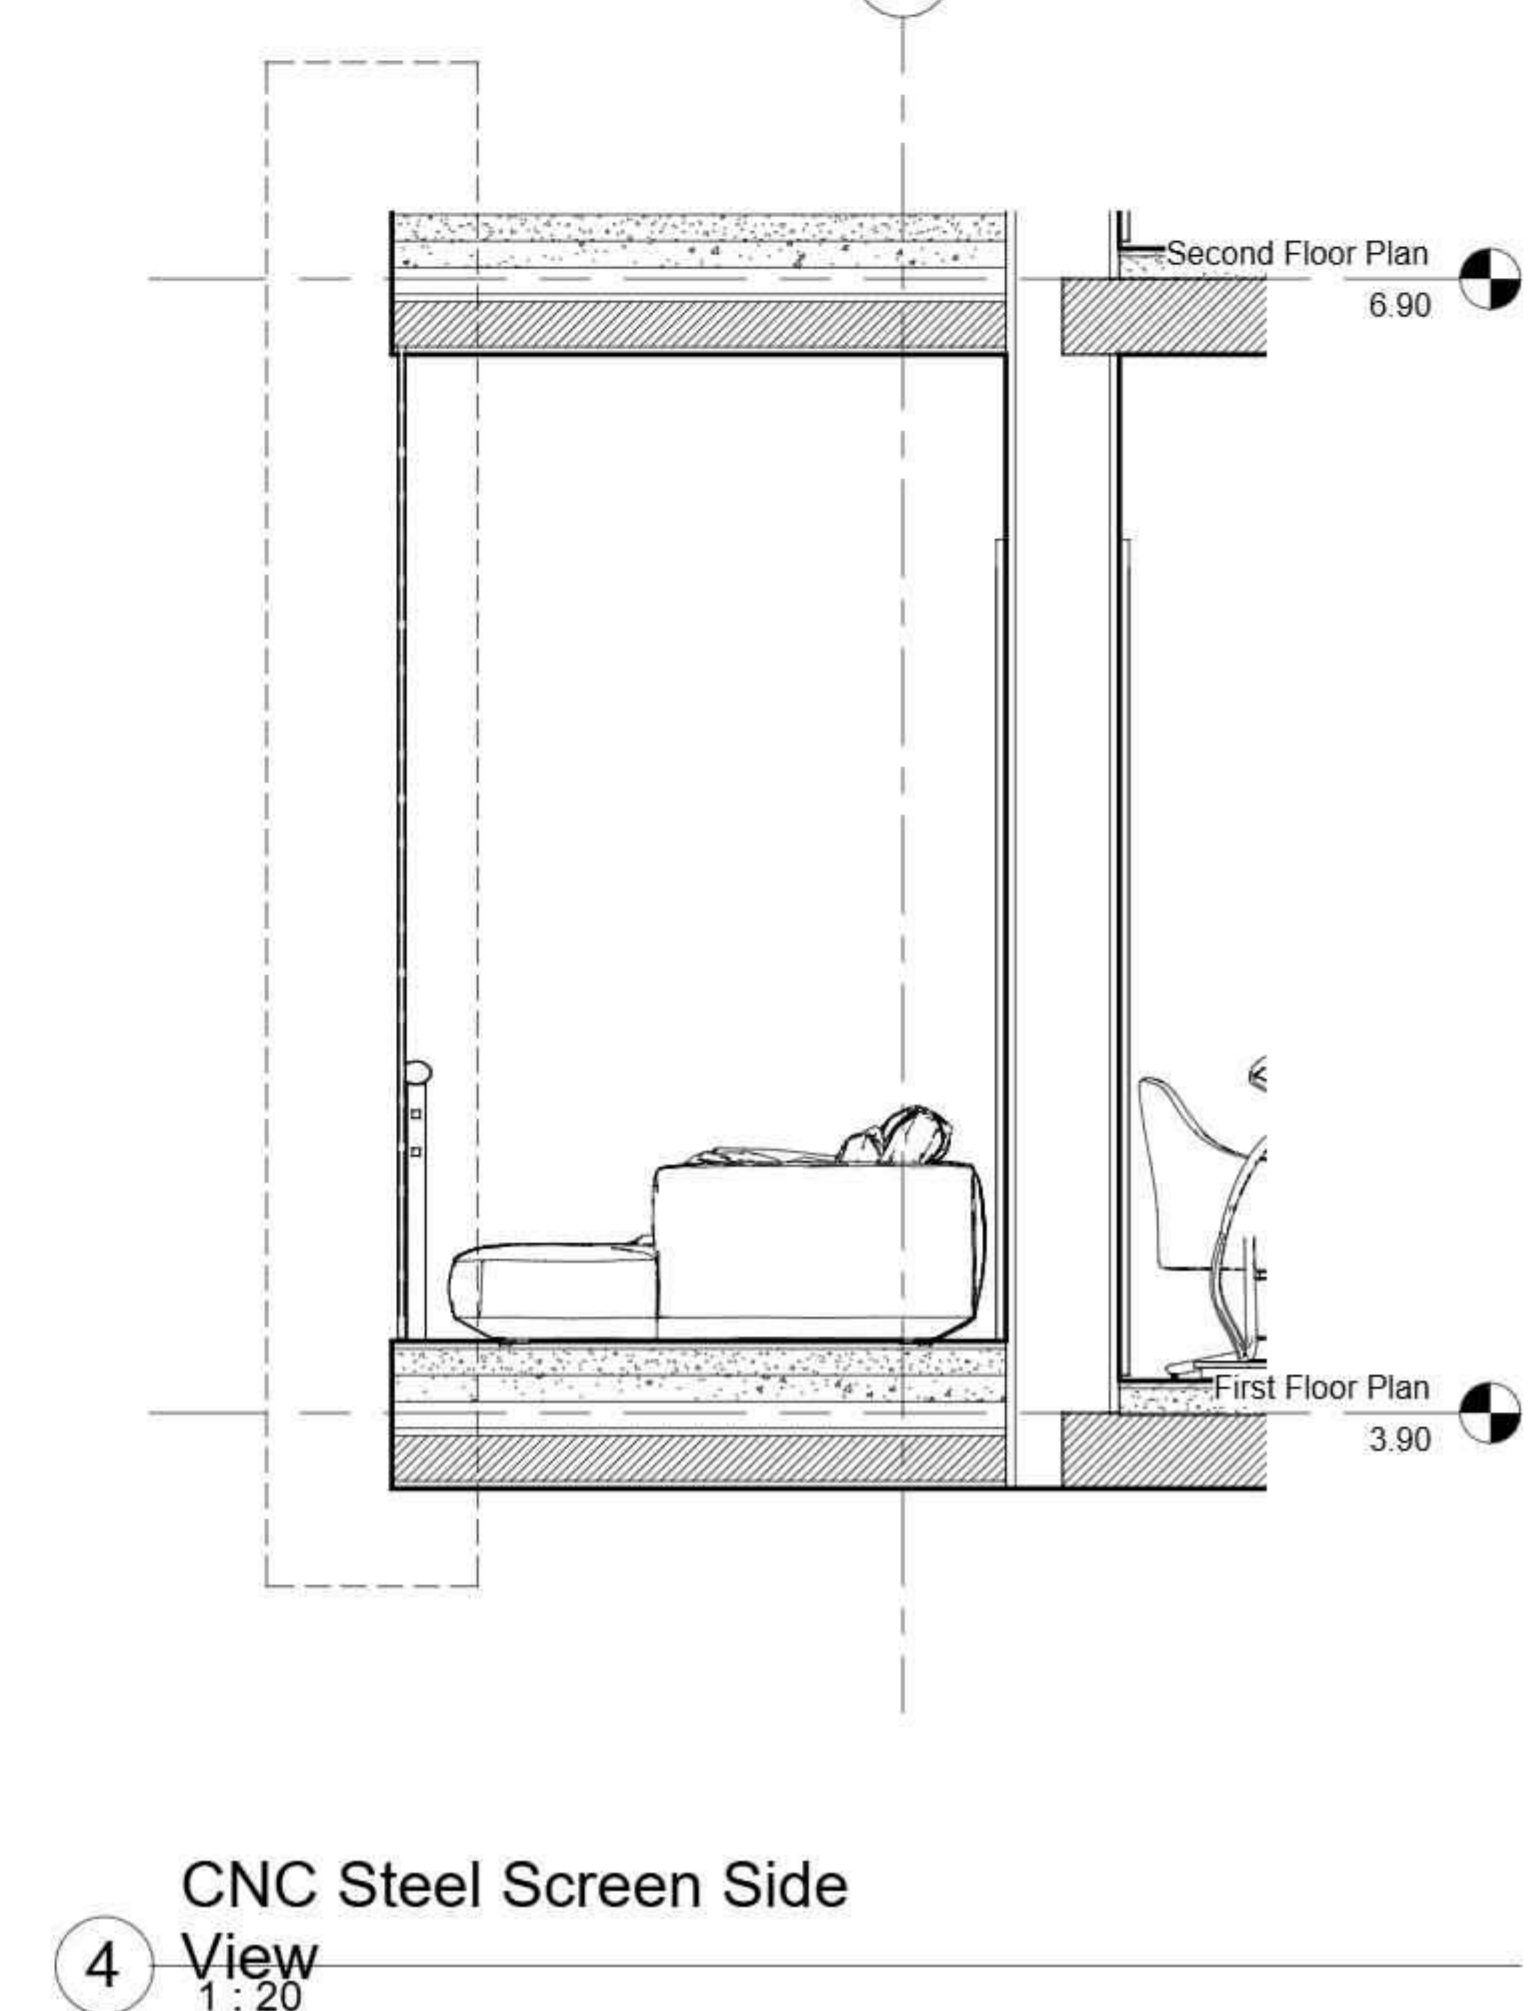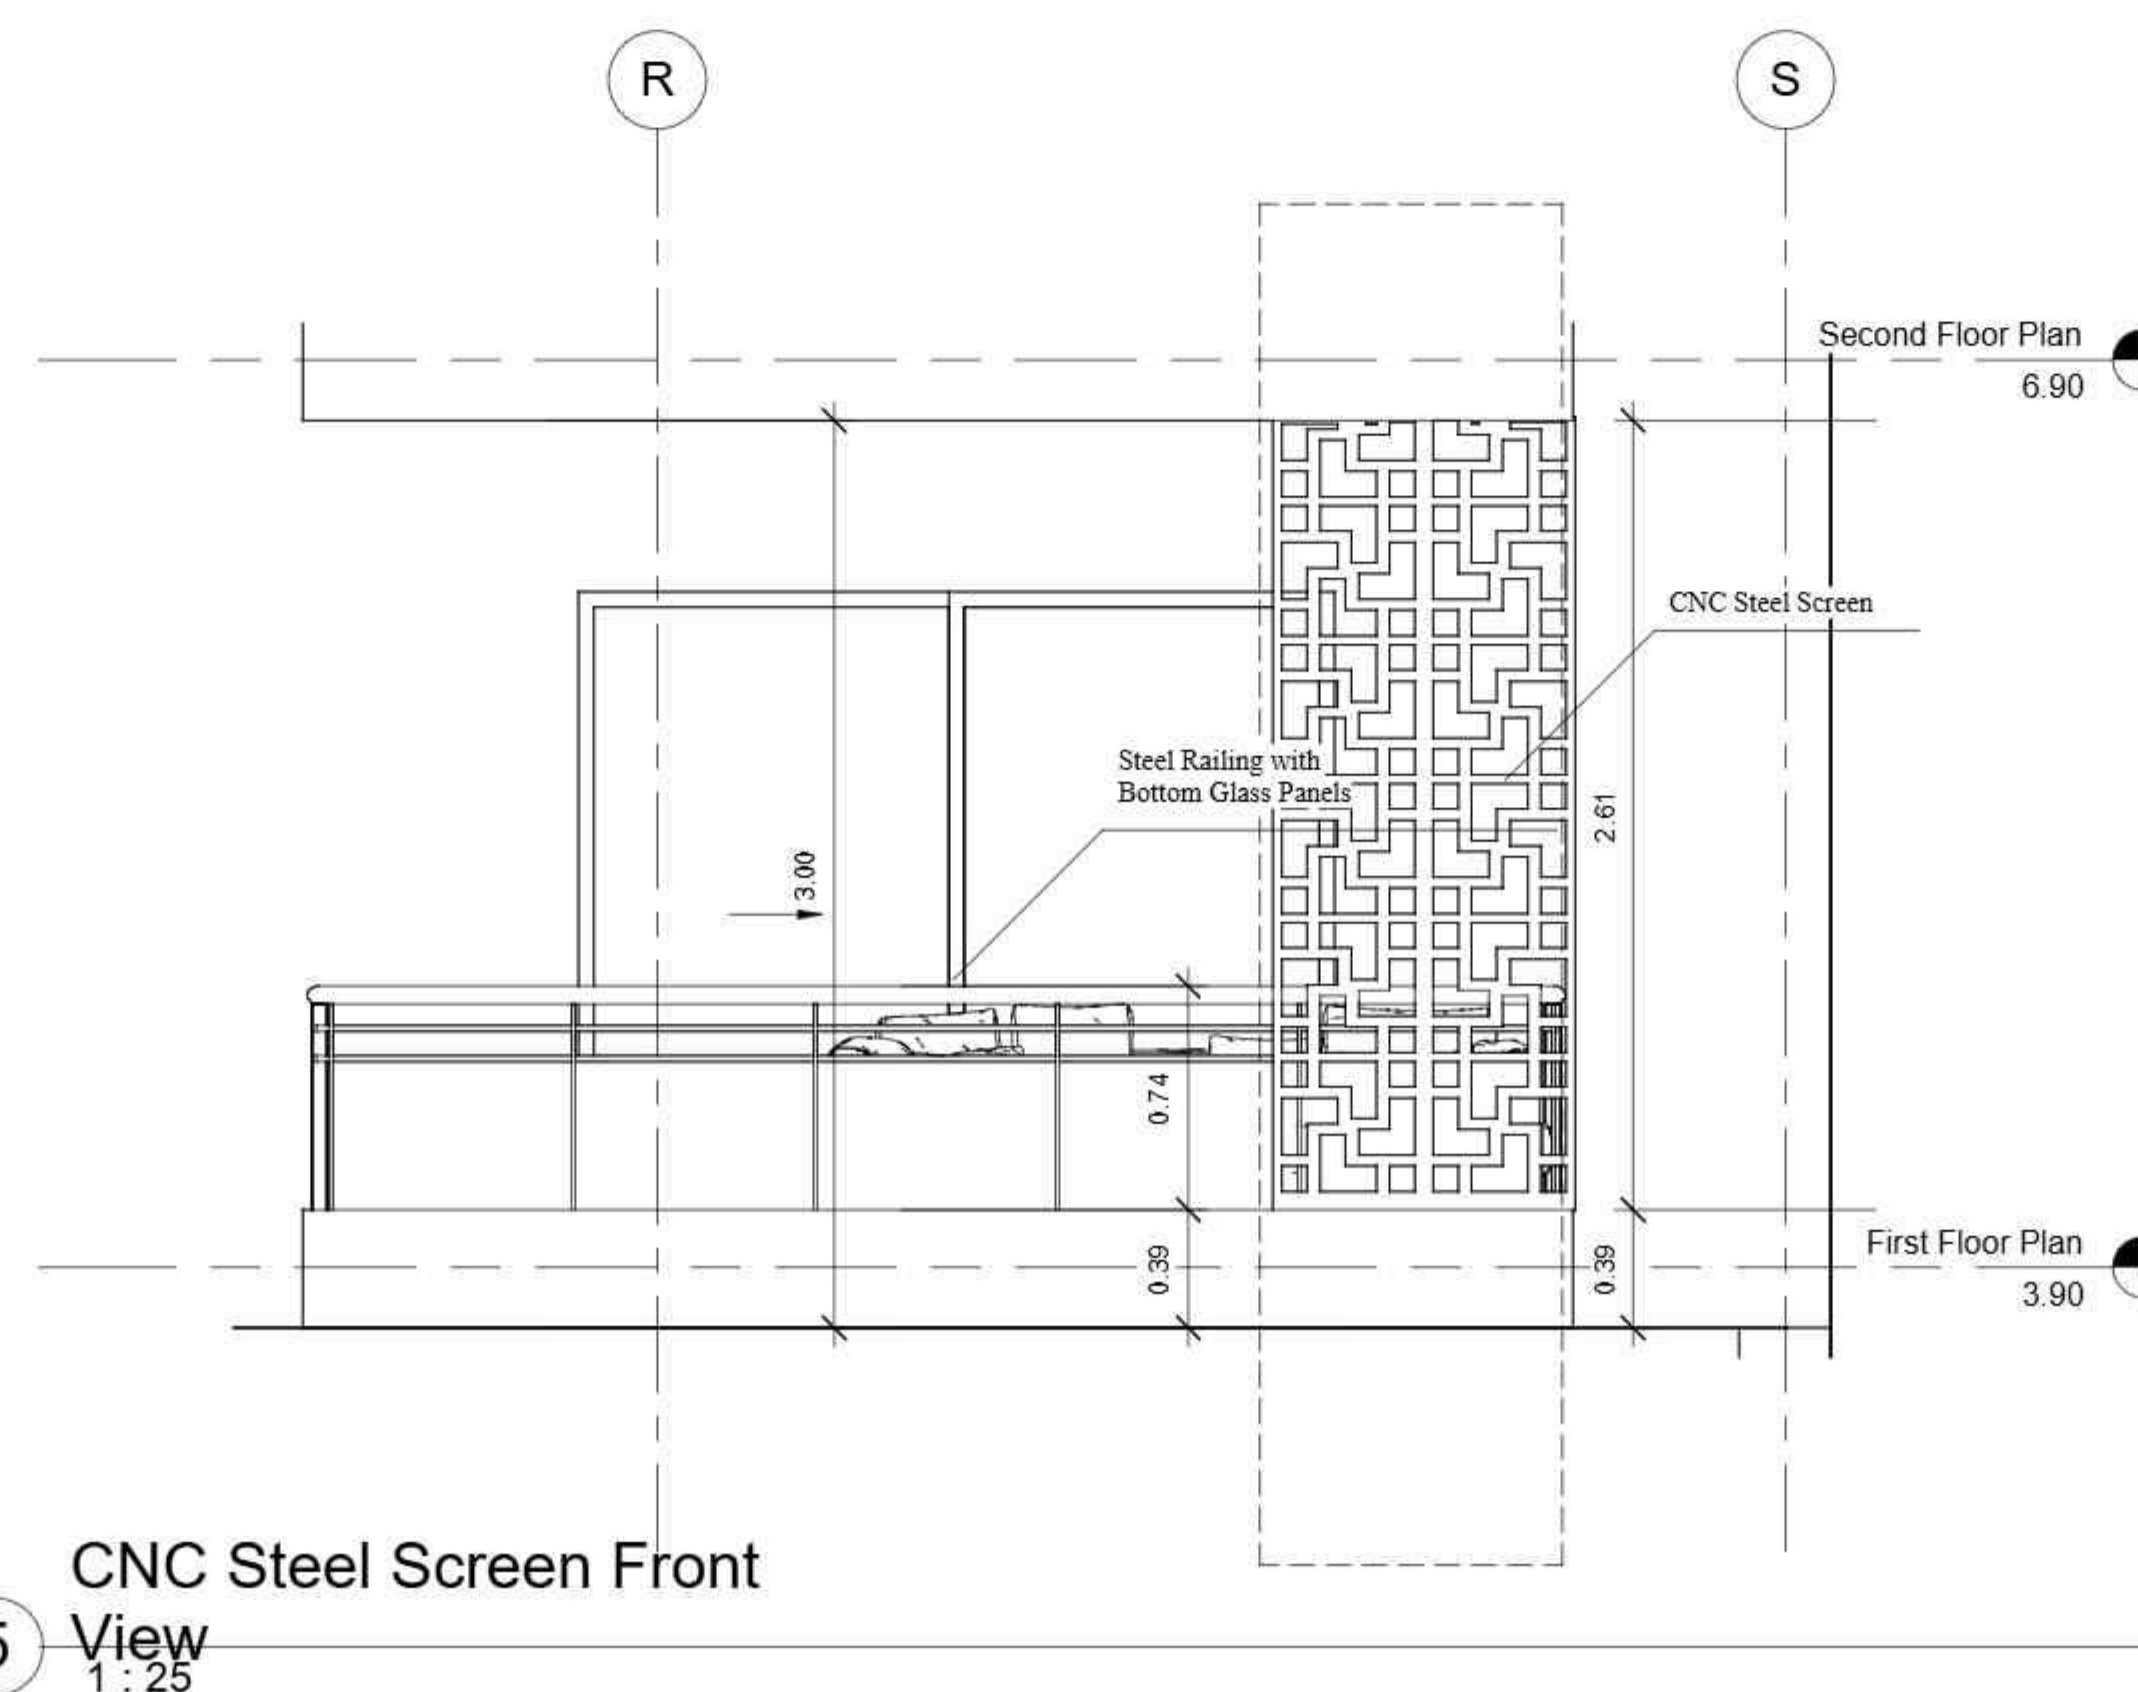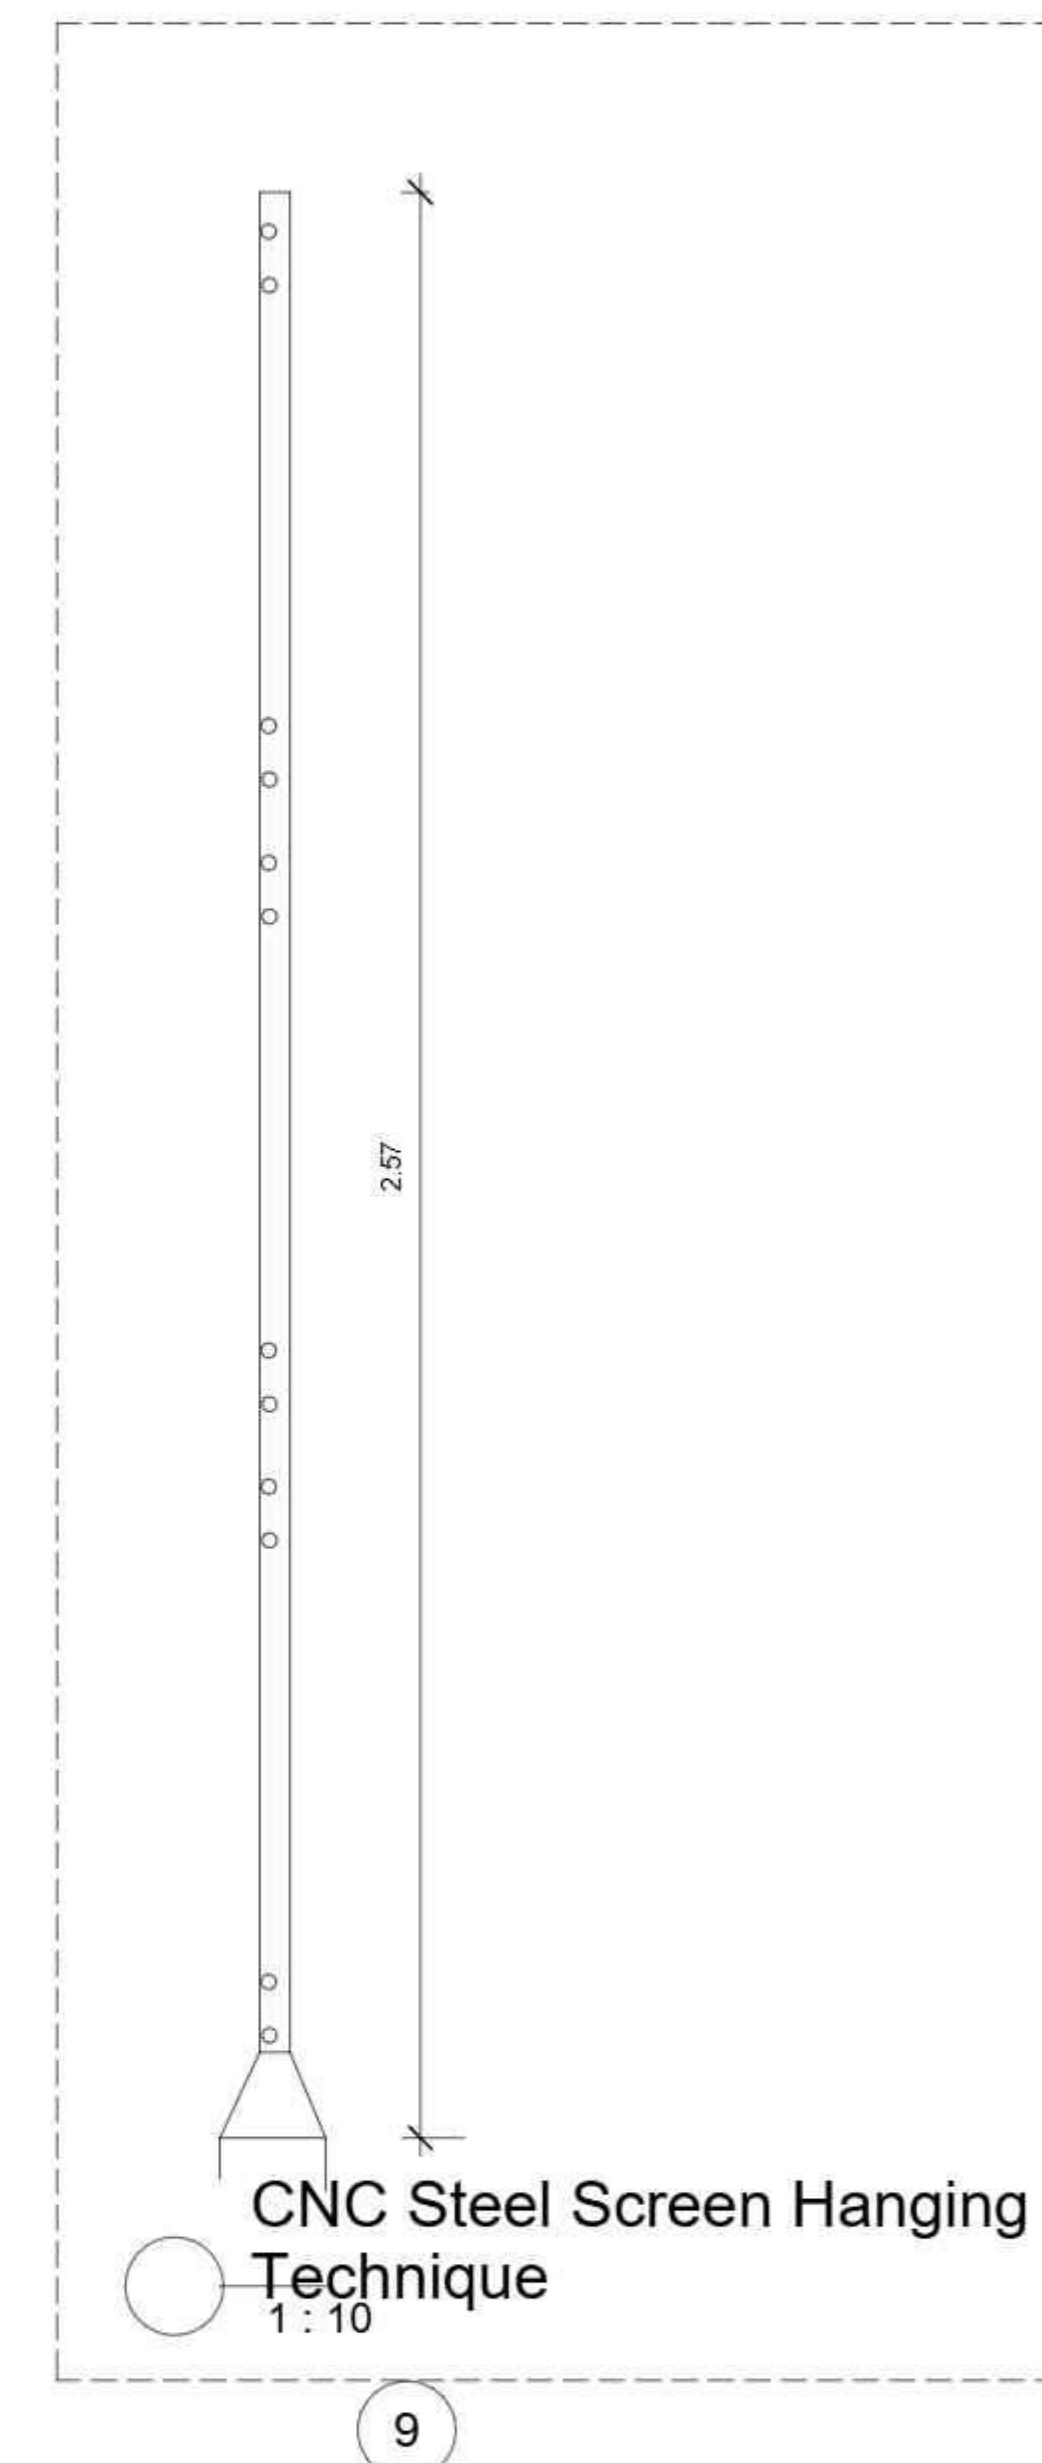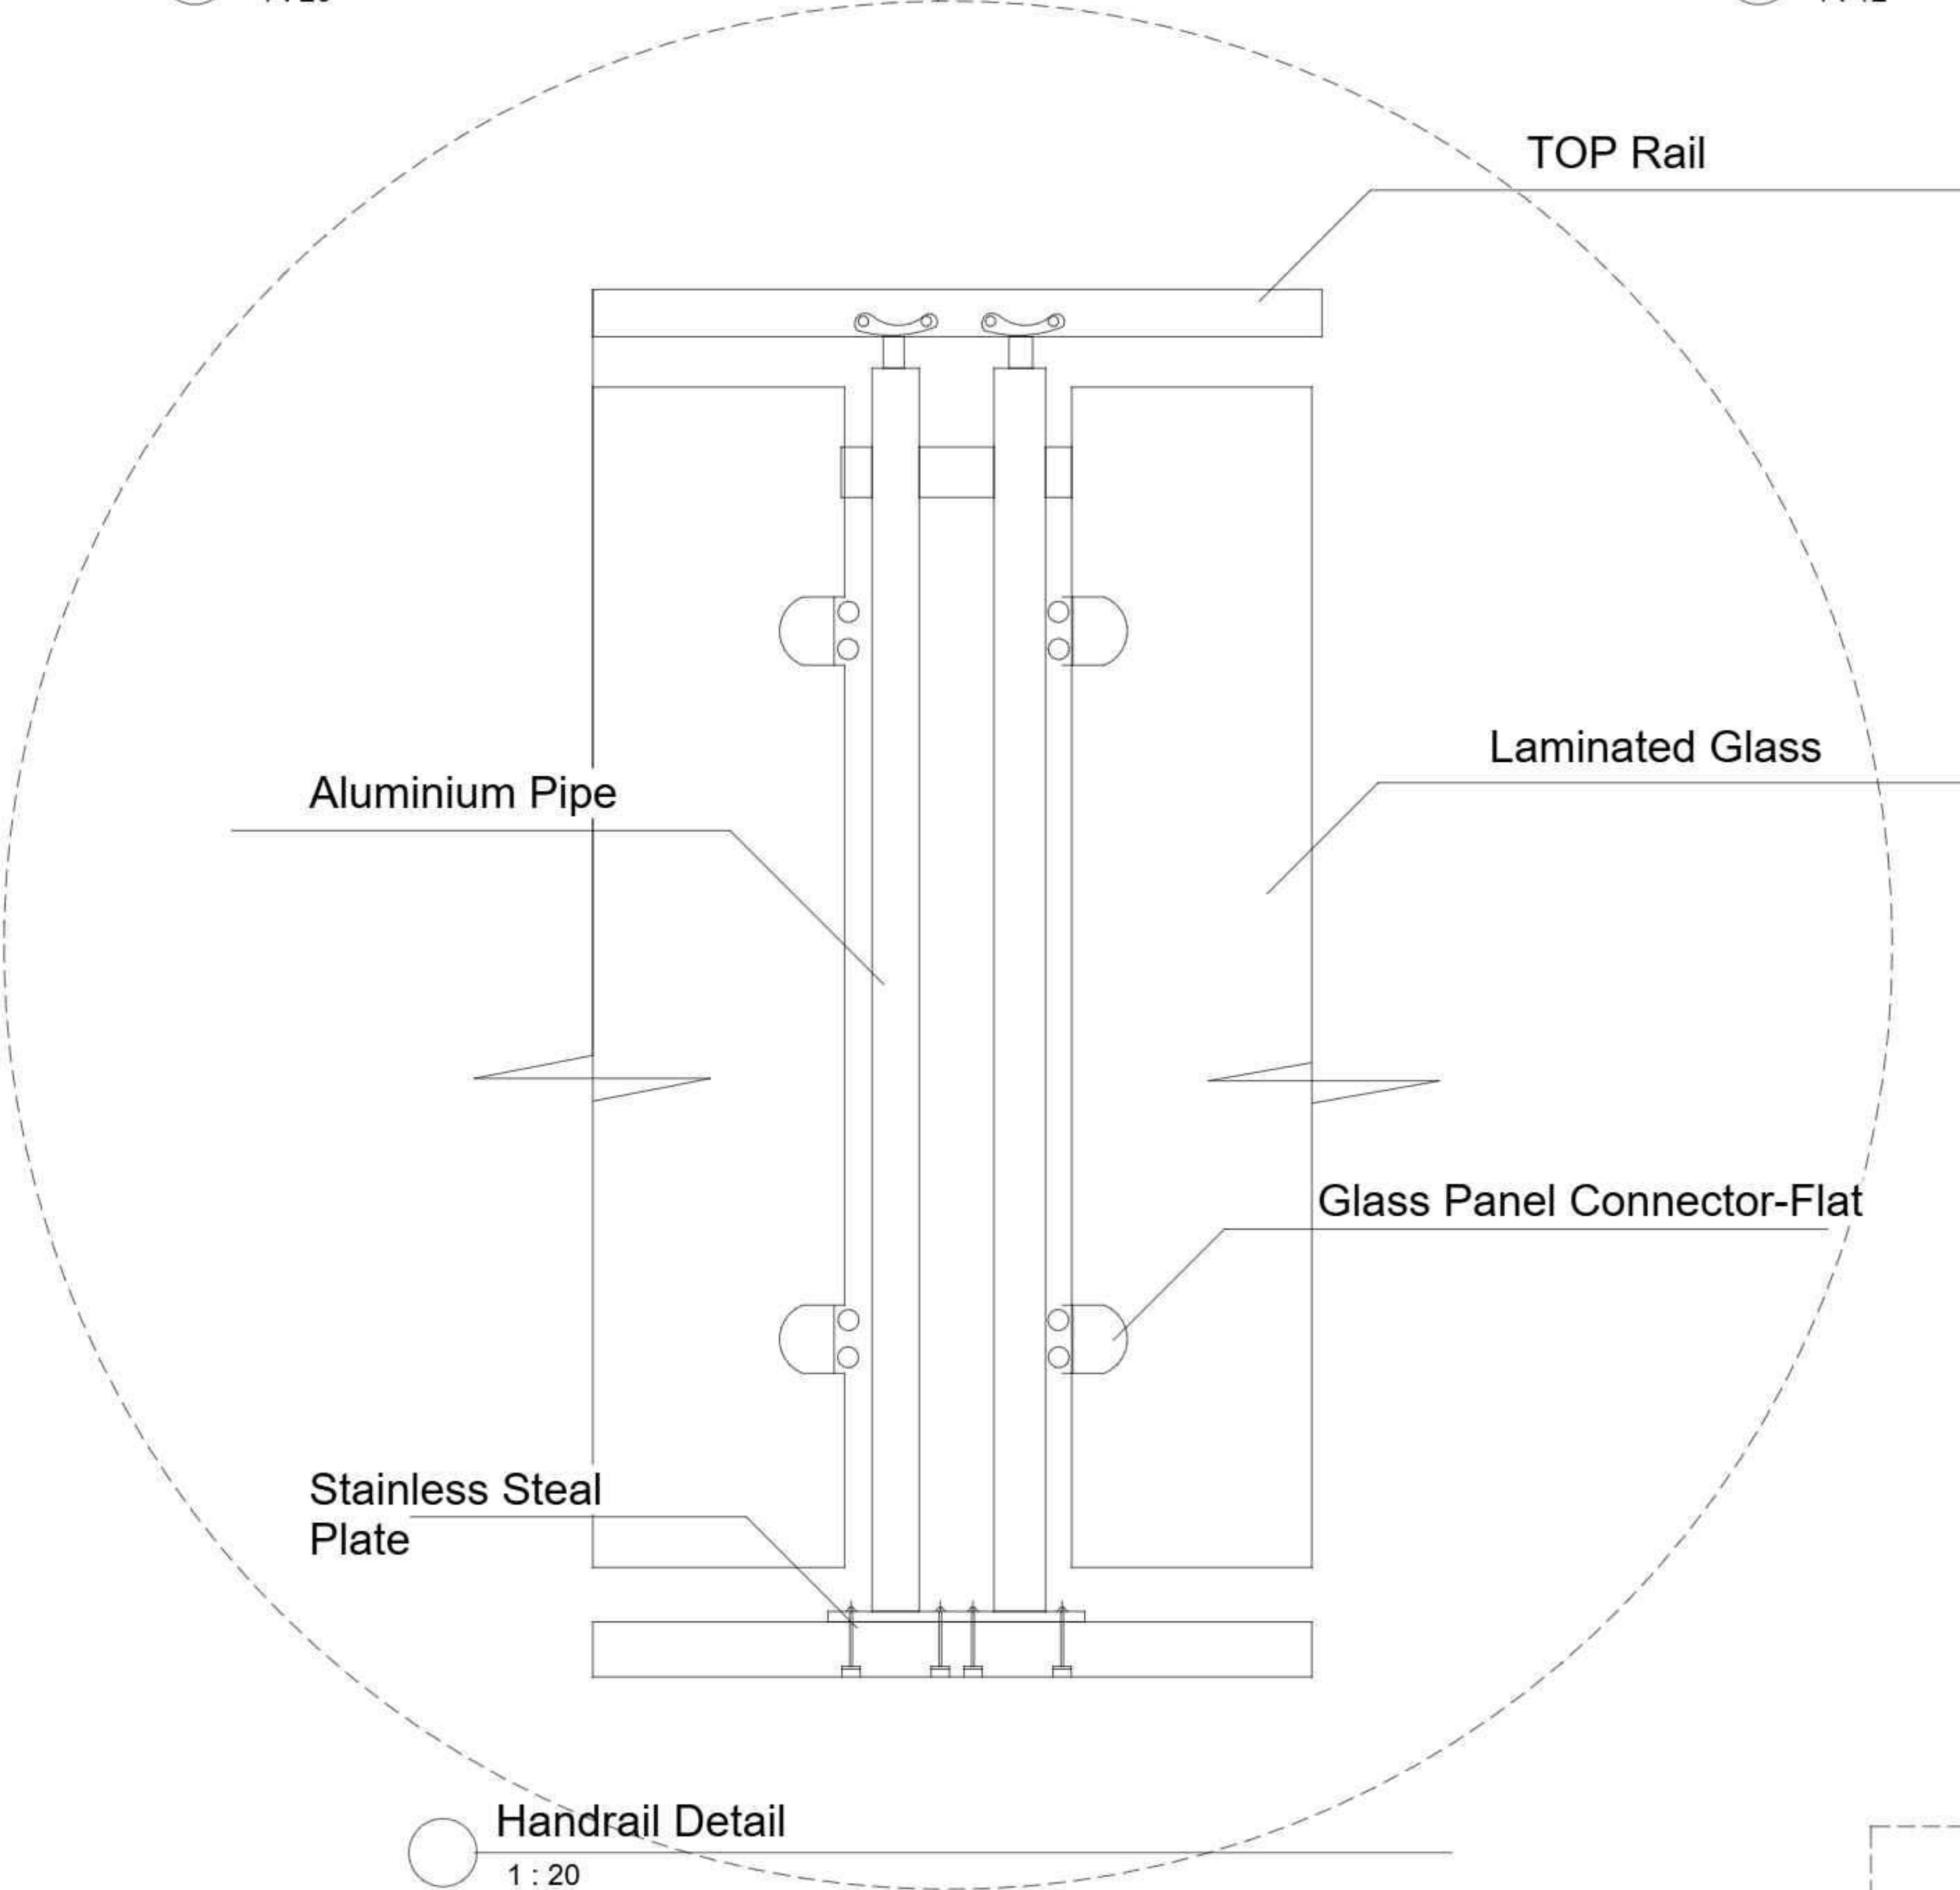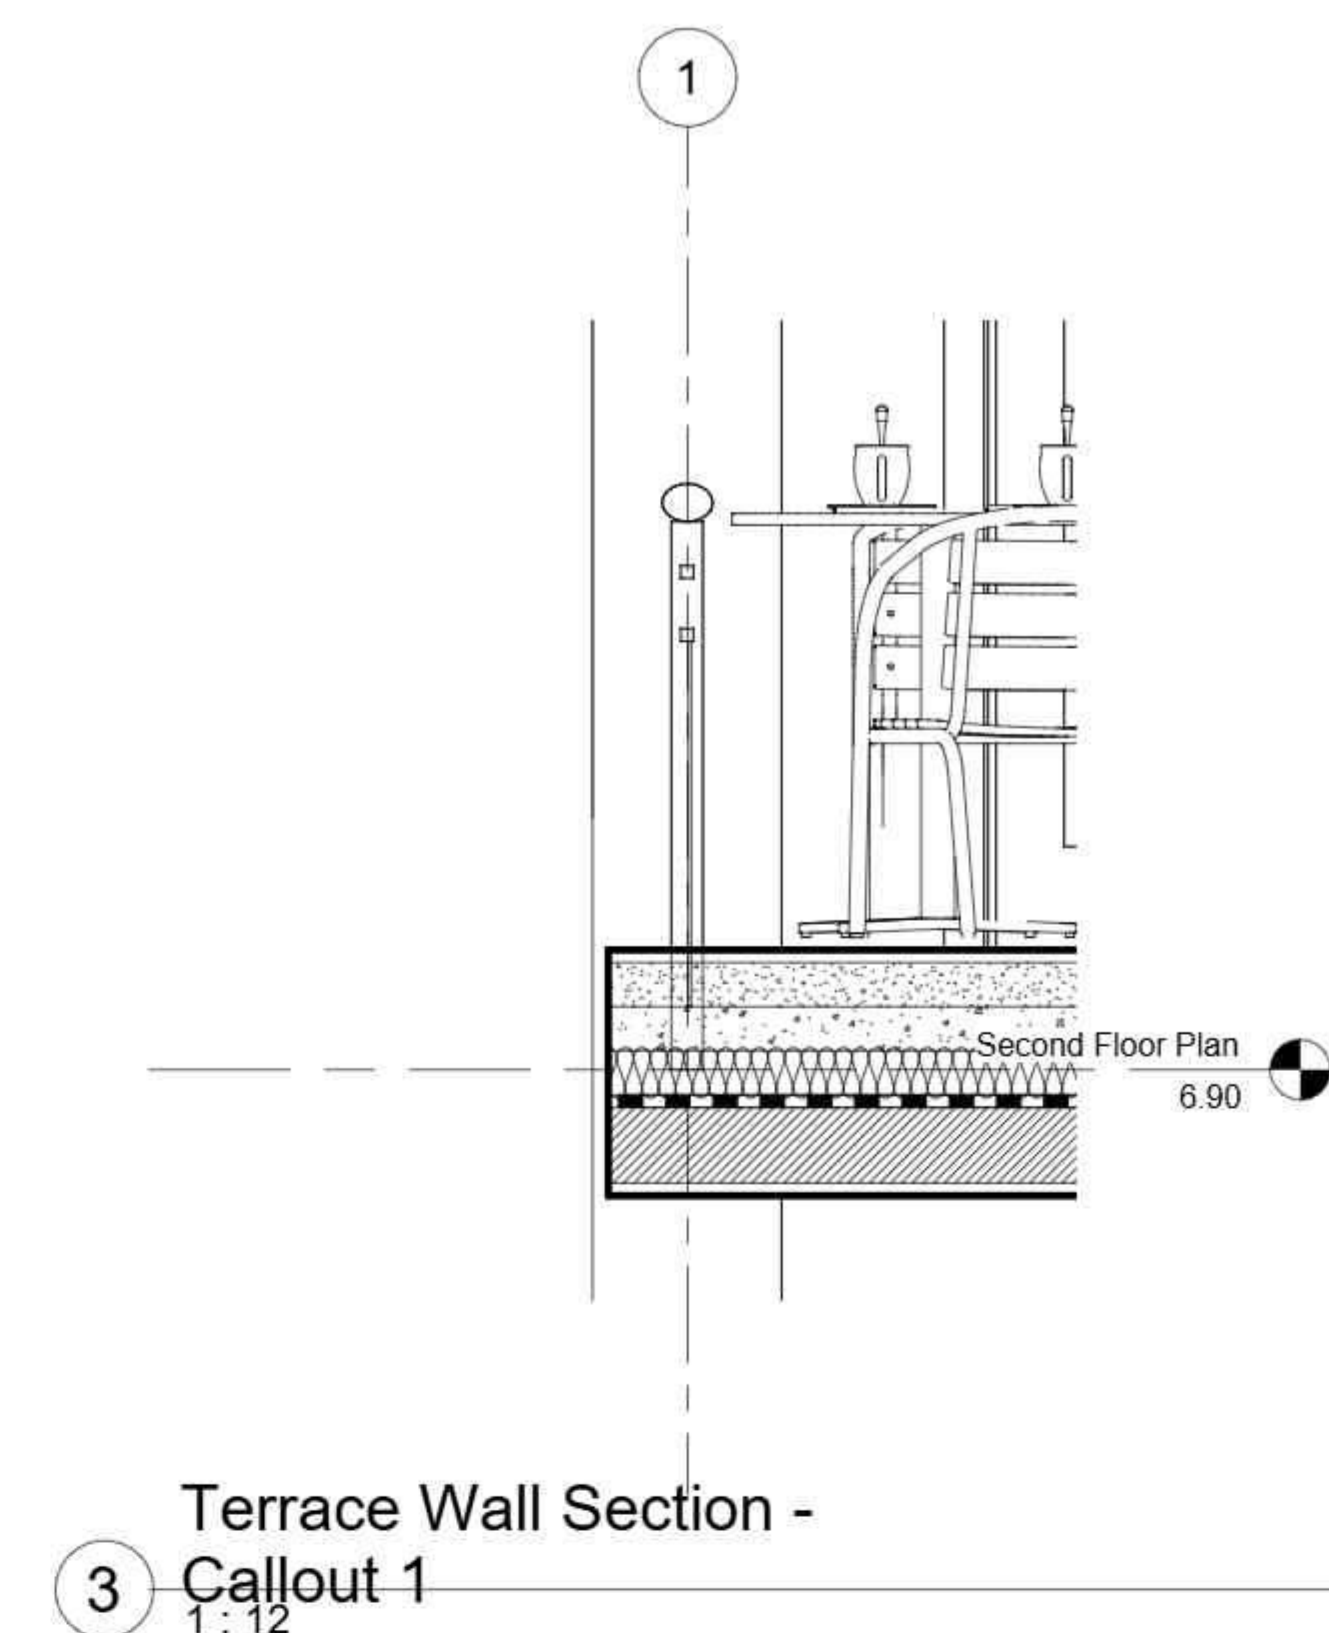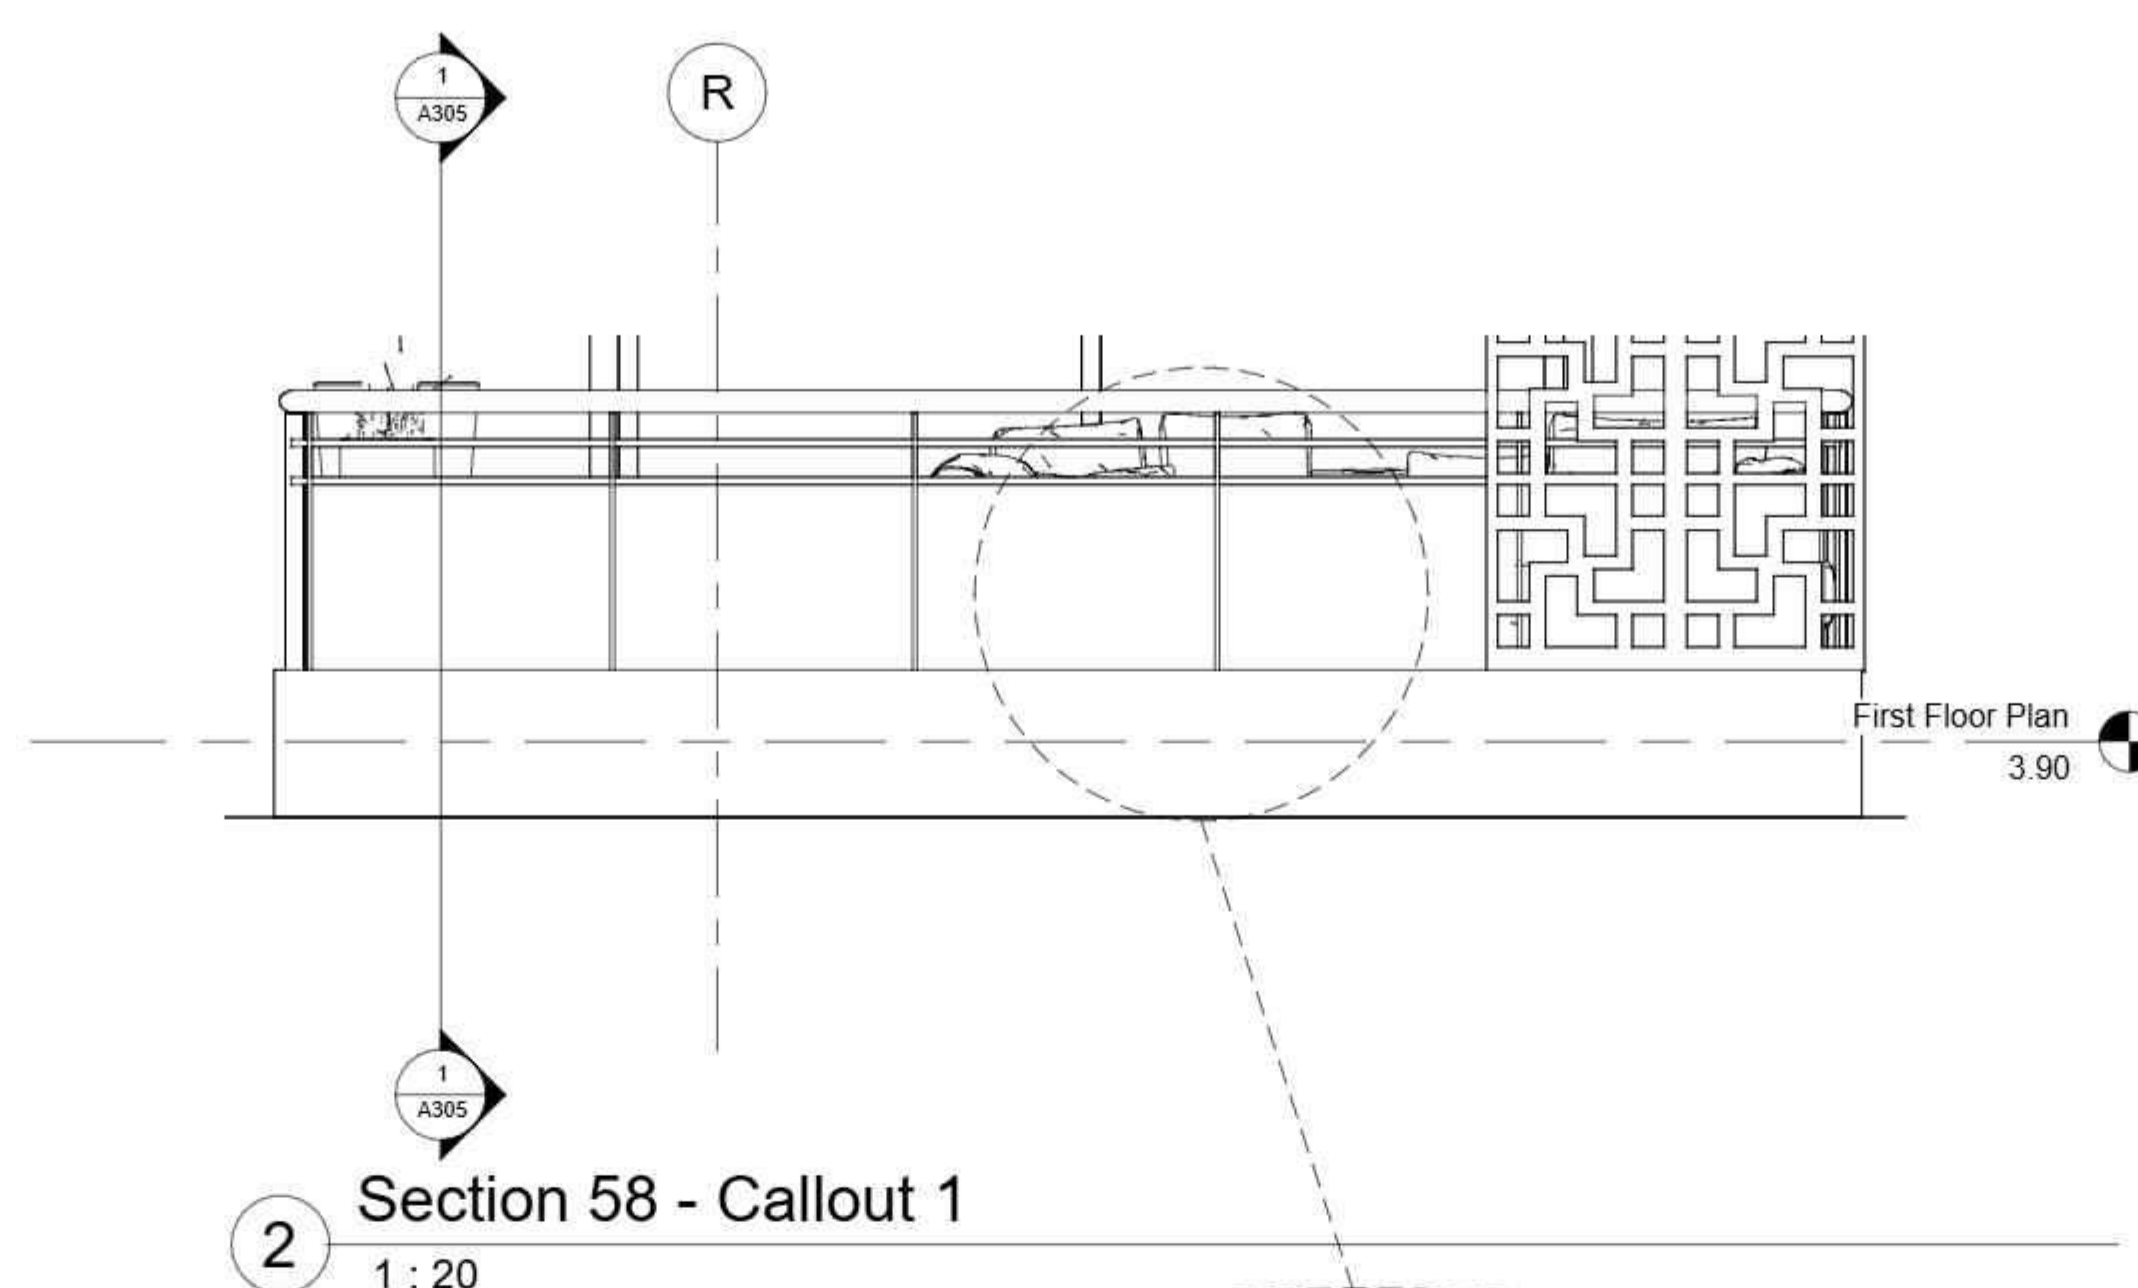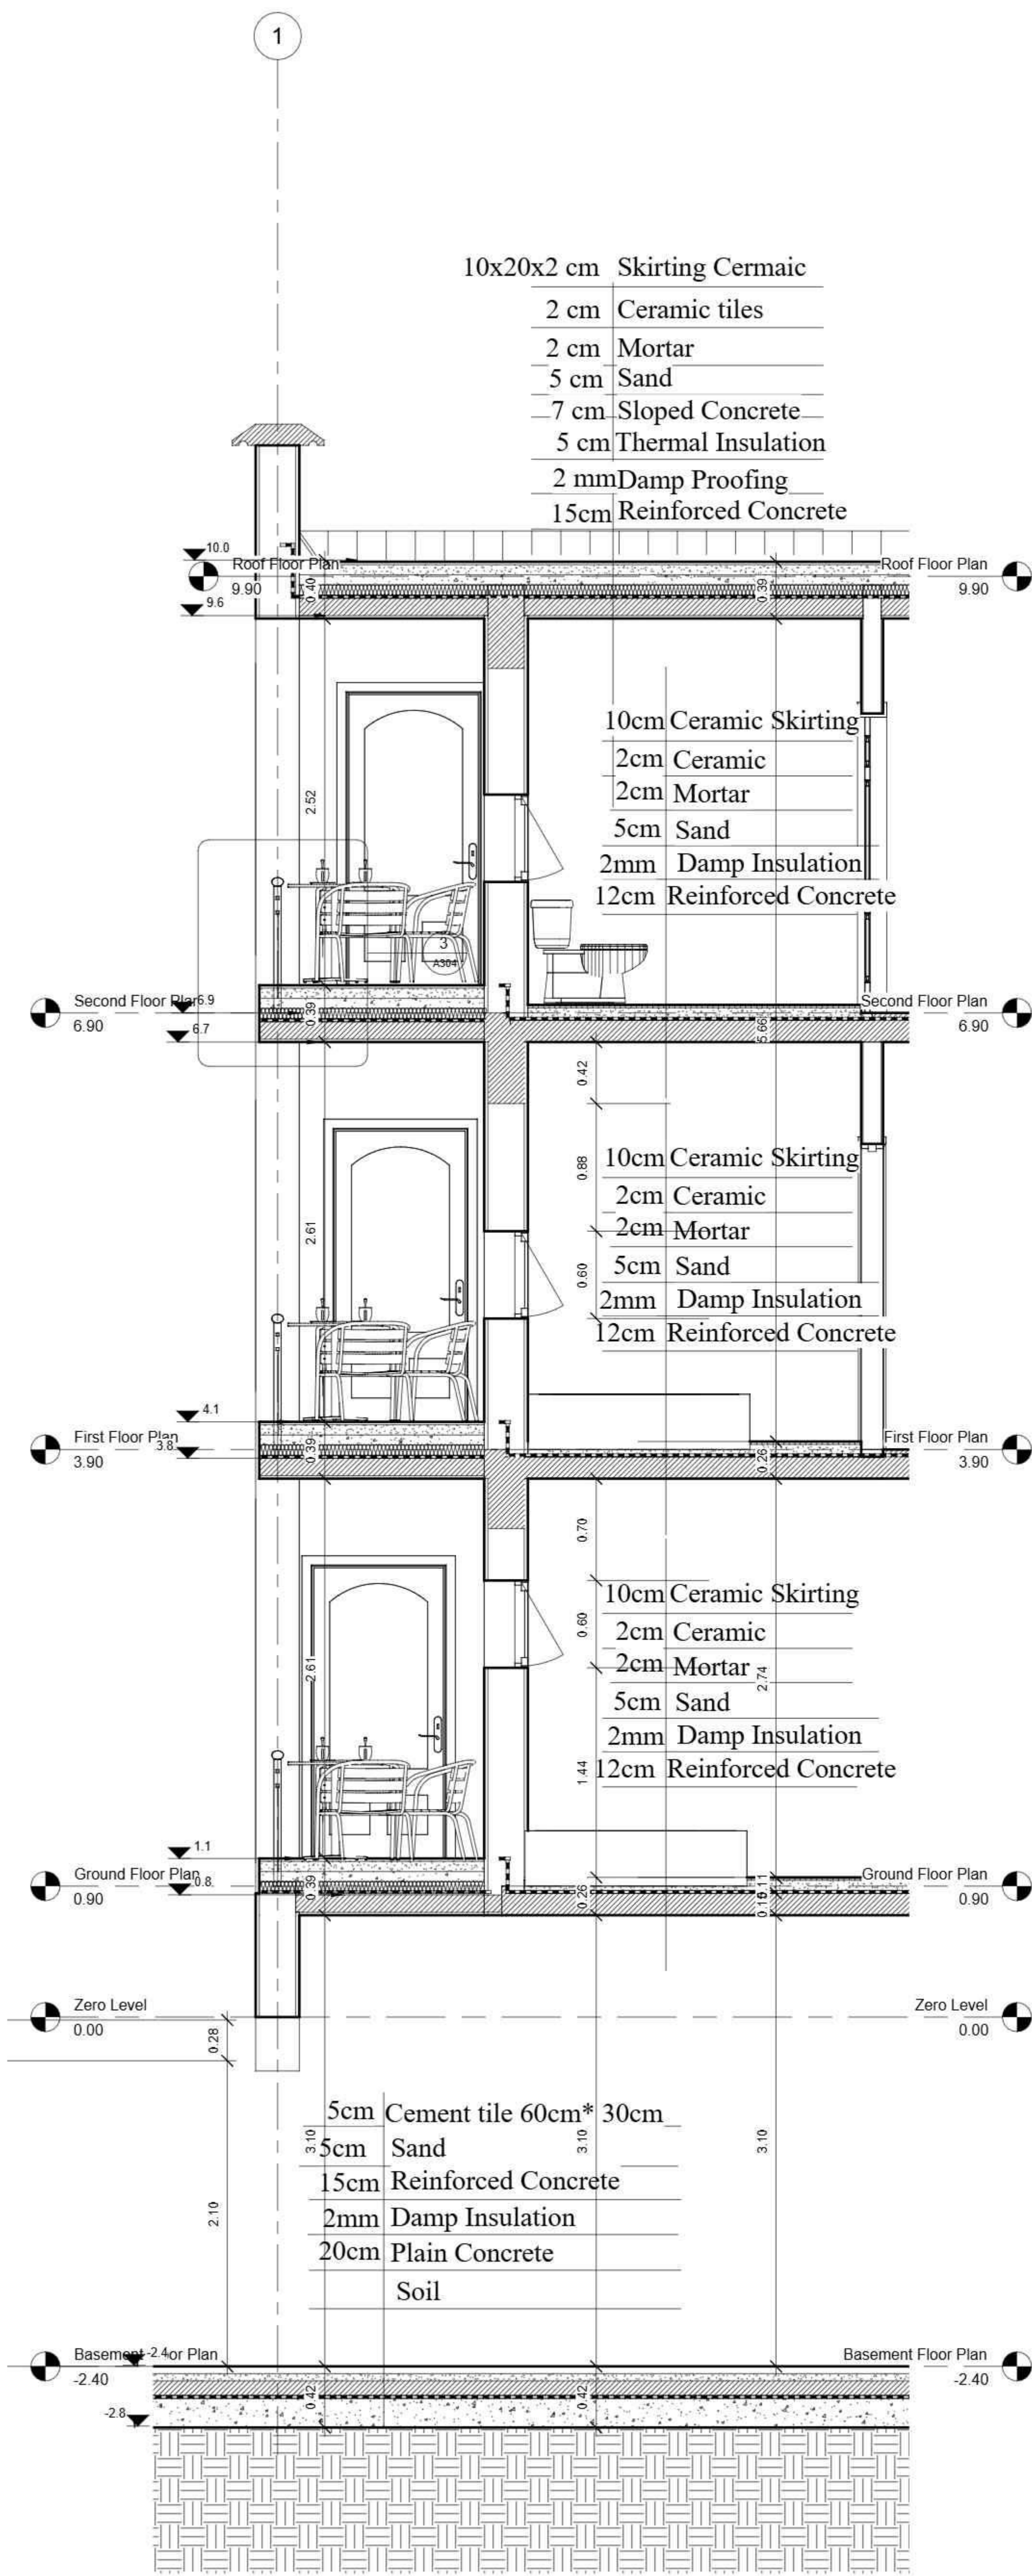

Course Info:
ASE 464
Working Drawings III

GENERAL NOTES:

- ALL MATERIALS & WORK PRACTICES SHALL COMPLY WITH, BUT NOT LIMITED TO THE BUILDING REGULATION 2019, THE NATIONAL CONSTRUCTION CODE OF EGYPT UNLESS OTHERWISE SPECIFIED.

- ALL DIMENSIONS ARE IN METERS. IF IN DOUBT ASK, DO NOT SCALE.

- THESE DRAWINGS SHALL BE READ IN CONJUNCTION WITH ALL RELEVANT STRUCTURAL + ALL OTHER CONSULTANTS DRAWINGS/DETAILS & WITH ANY OTHER WRITTEN INSTRUCTIONS ISSUED IN THE COURSE OF THE CONTRACT.

- THESE DRAWINGS SHALL BE READ IN CONJUNCTION WITH ANY ENERGY RATING REPORT + SHALL BE CONSTRUCTED IN ACCORDANCE WITH THE STAMPED PLANS ENDORSED BY THE ACCREDITED THERMAL PERFORMANCE ASSESSOR WITHOUT ALTERATION



OWNER:



OCTOBER UNIVERSITY
FOR MODERN SCIENCES & ARTS
Architectural Engineering Department
Spring 2025

CLIENTS NAME:

Dr. Tarek Galal
Eng. Hend
Eng. Nermeen
Eng. Yousra

Student Name: Hadeel Zakaria
ID: 220009

PROJECT NAME:
APARTMENT BUILDING

SHEET NAME:

DETAILS


SHEET NO:

A401


SCALE:

1:-


DATE: 13-5-2025

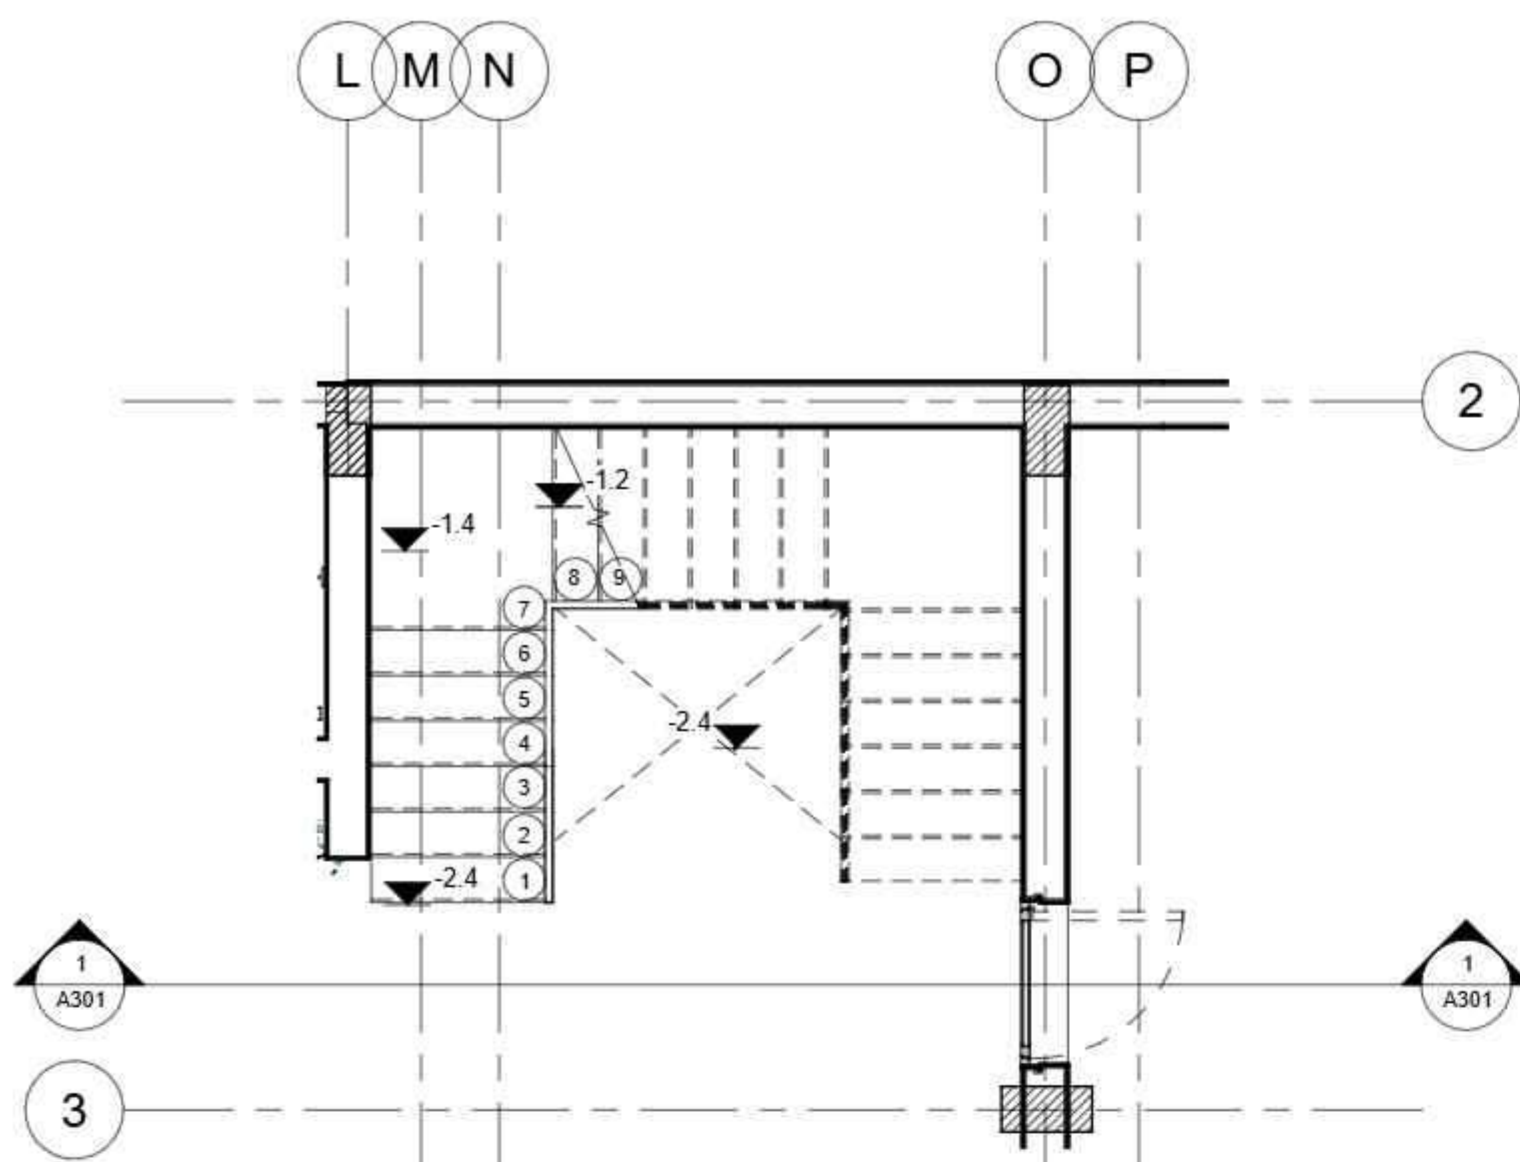


Basement Floor Plan -
Callout 1
1 : 50

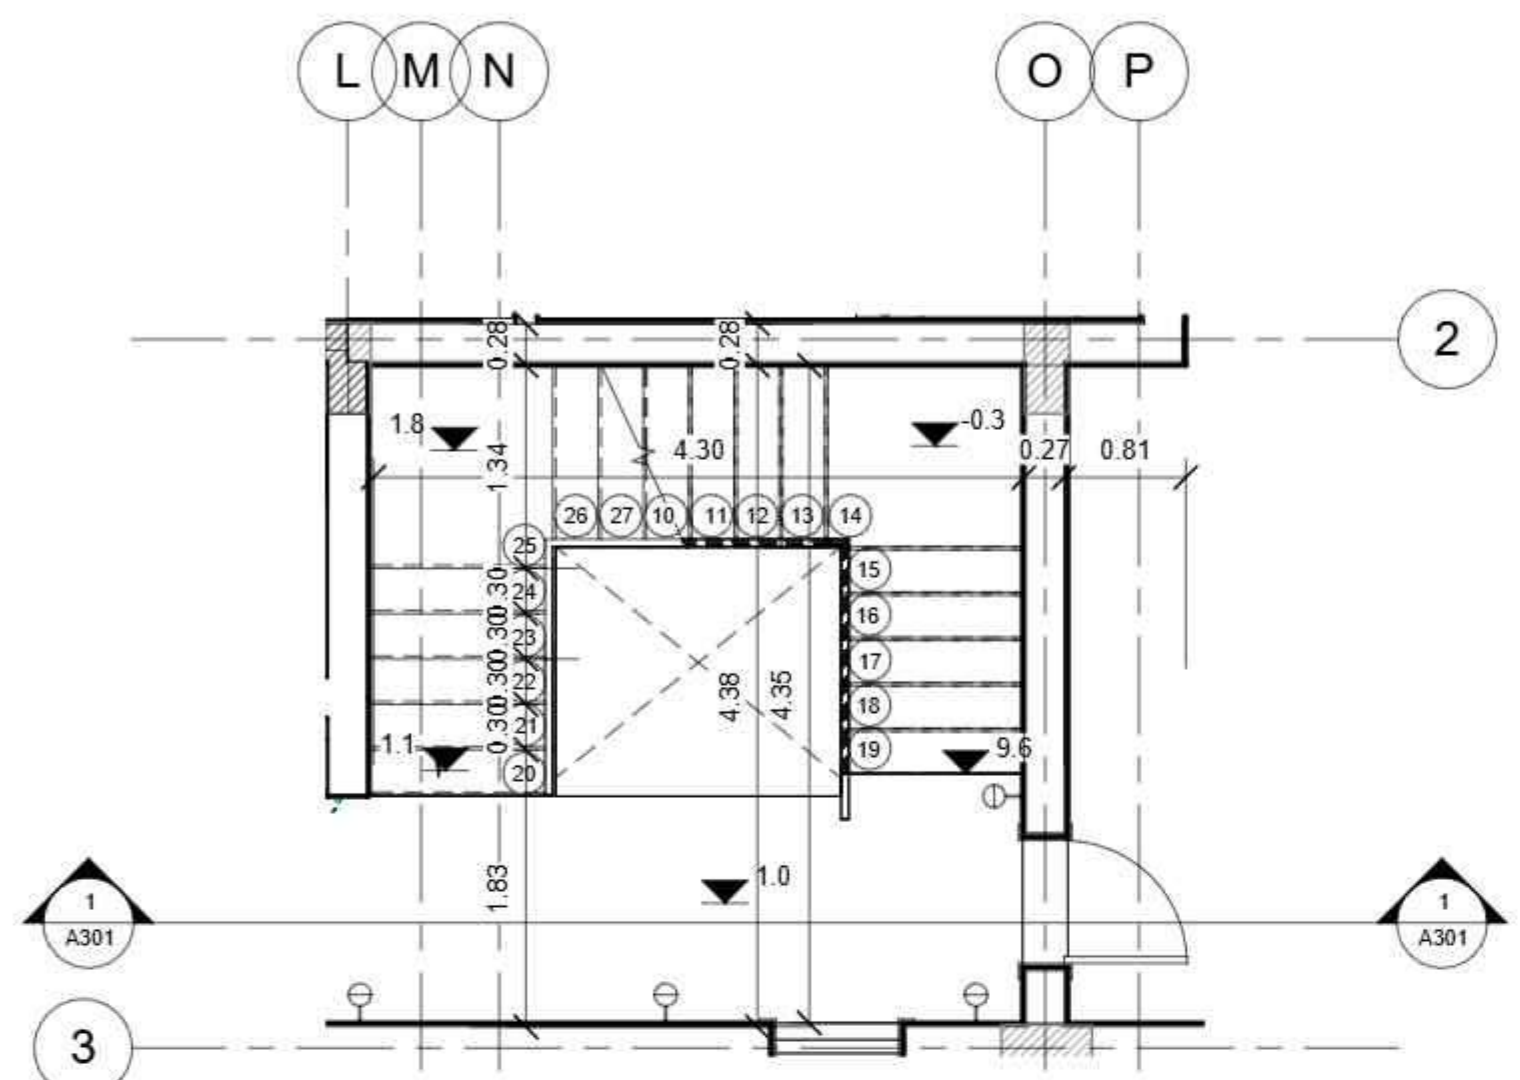


Ground Floor Plan - Callout
1 : 50

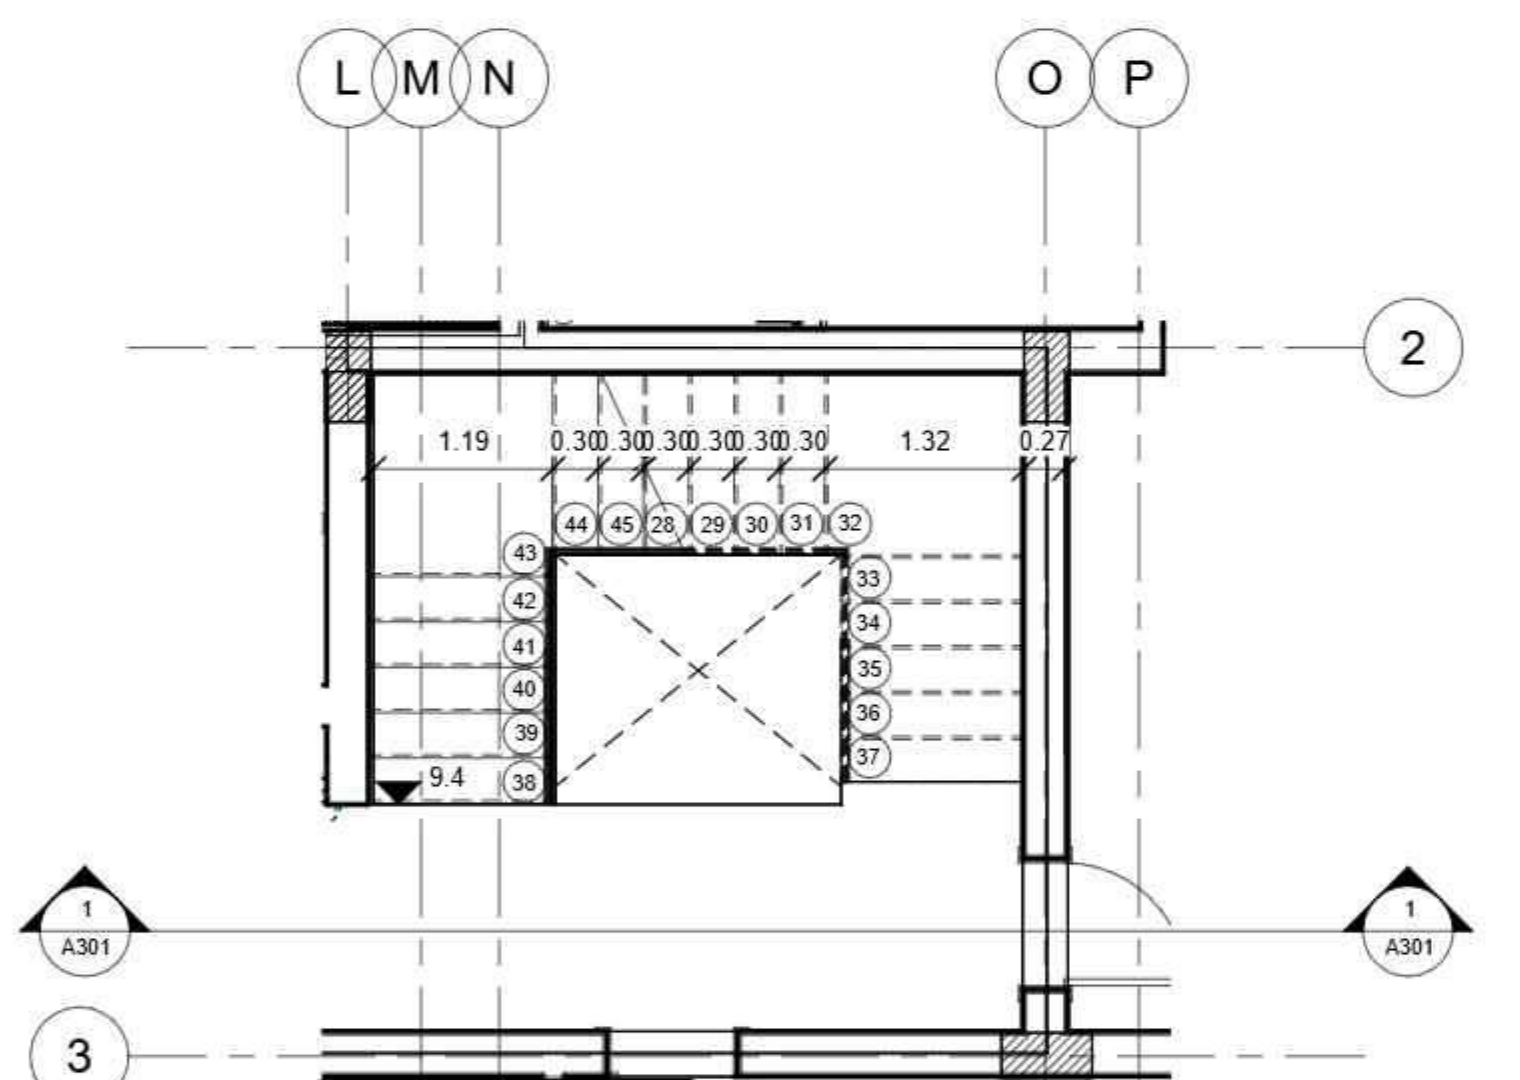


First Floor Plan - Callout 1
1 : 50

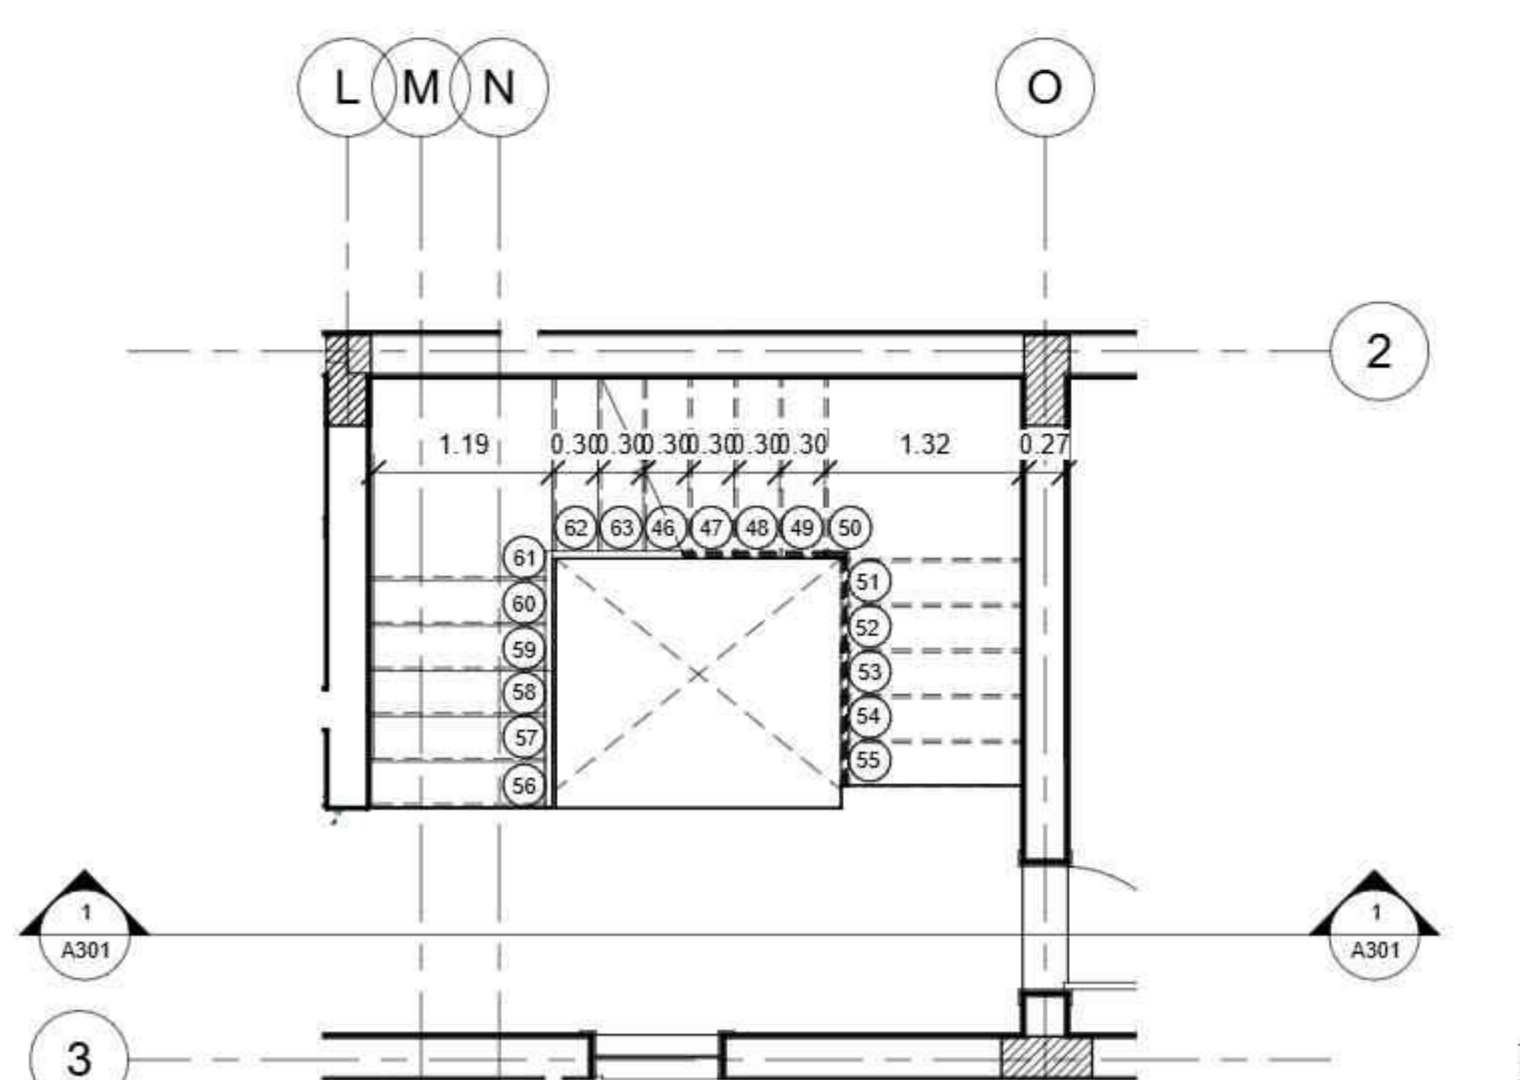


Second Floor Plan - Callout
1 : 50

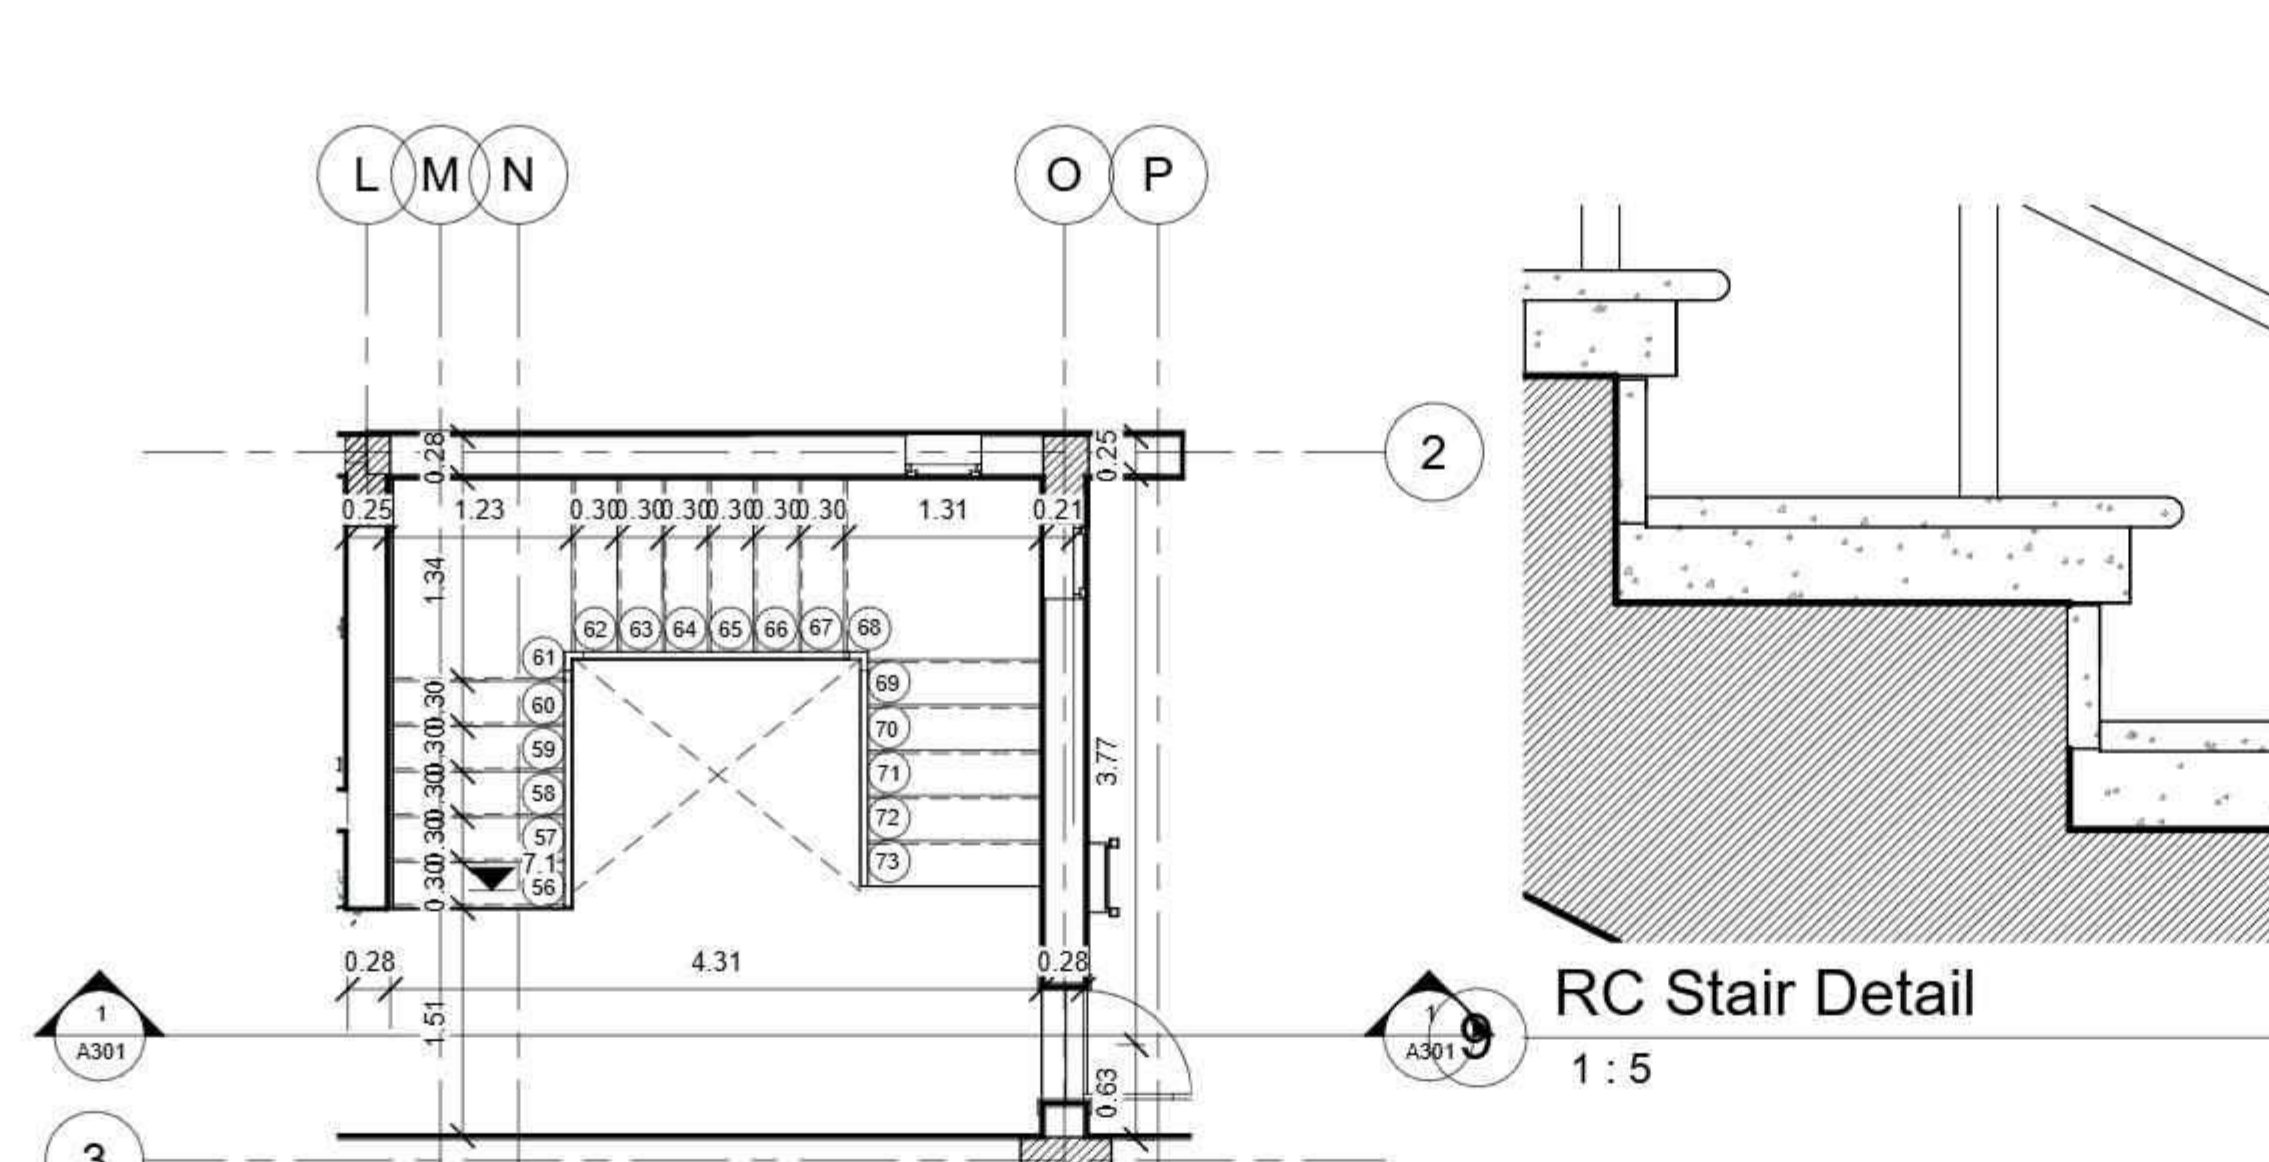


Roof Floor Plan - Callout 1
1 : 50

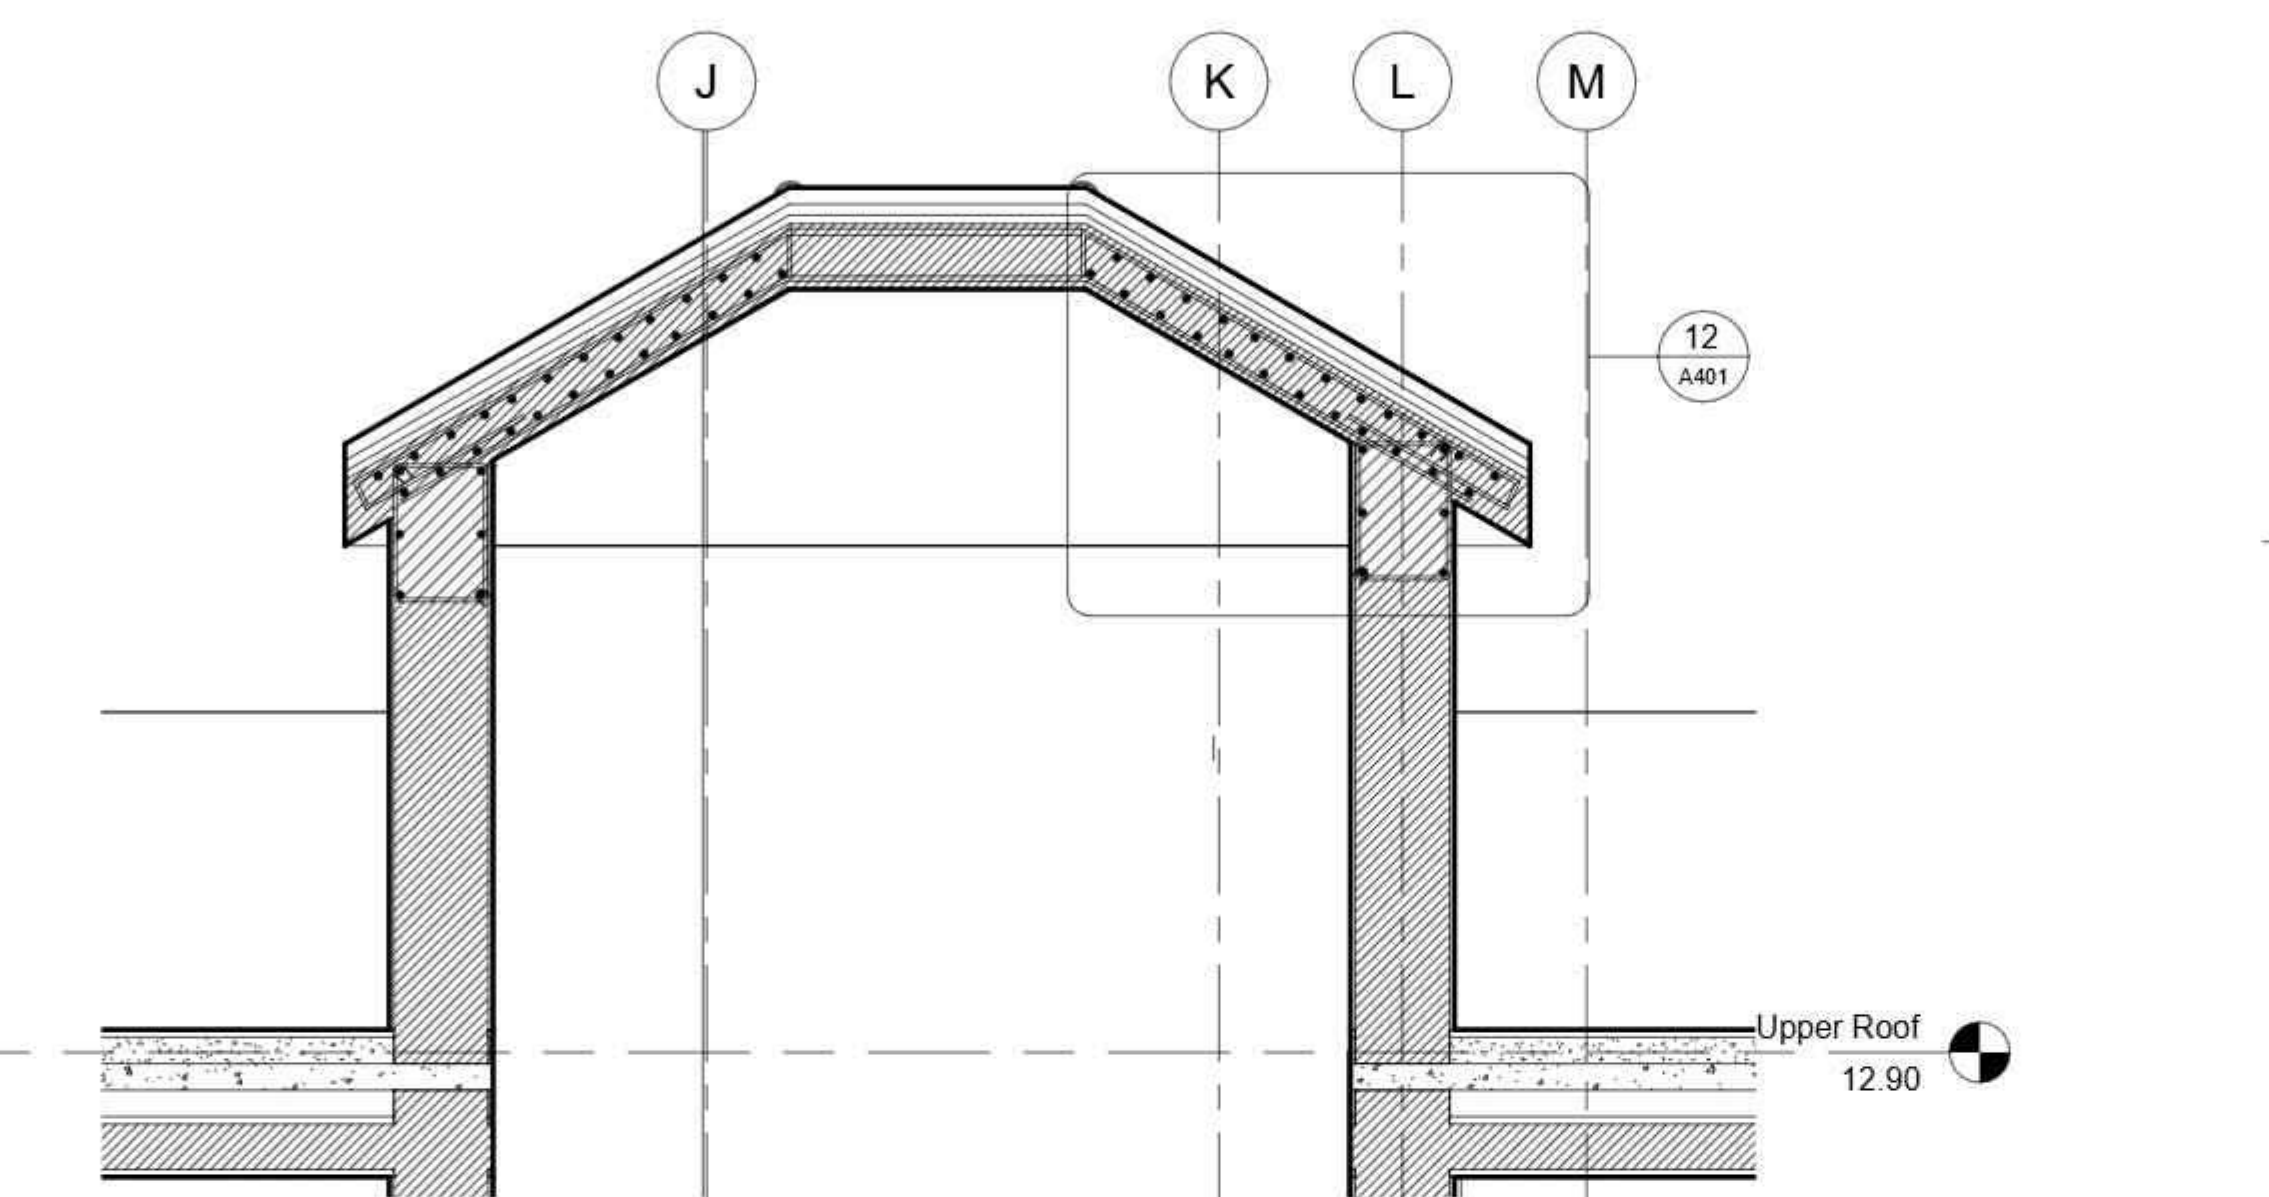


Pitched Roof Detail
1 : 20

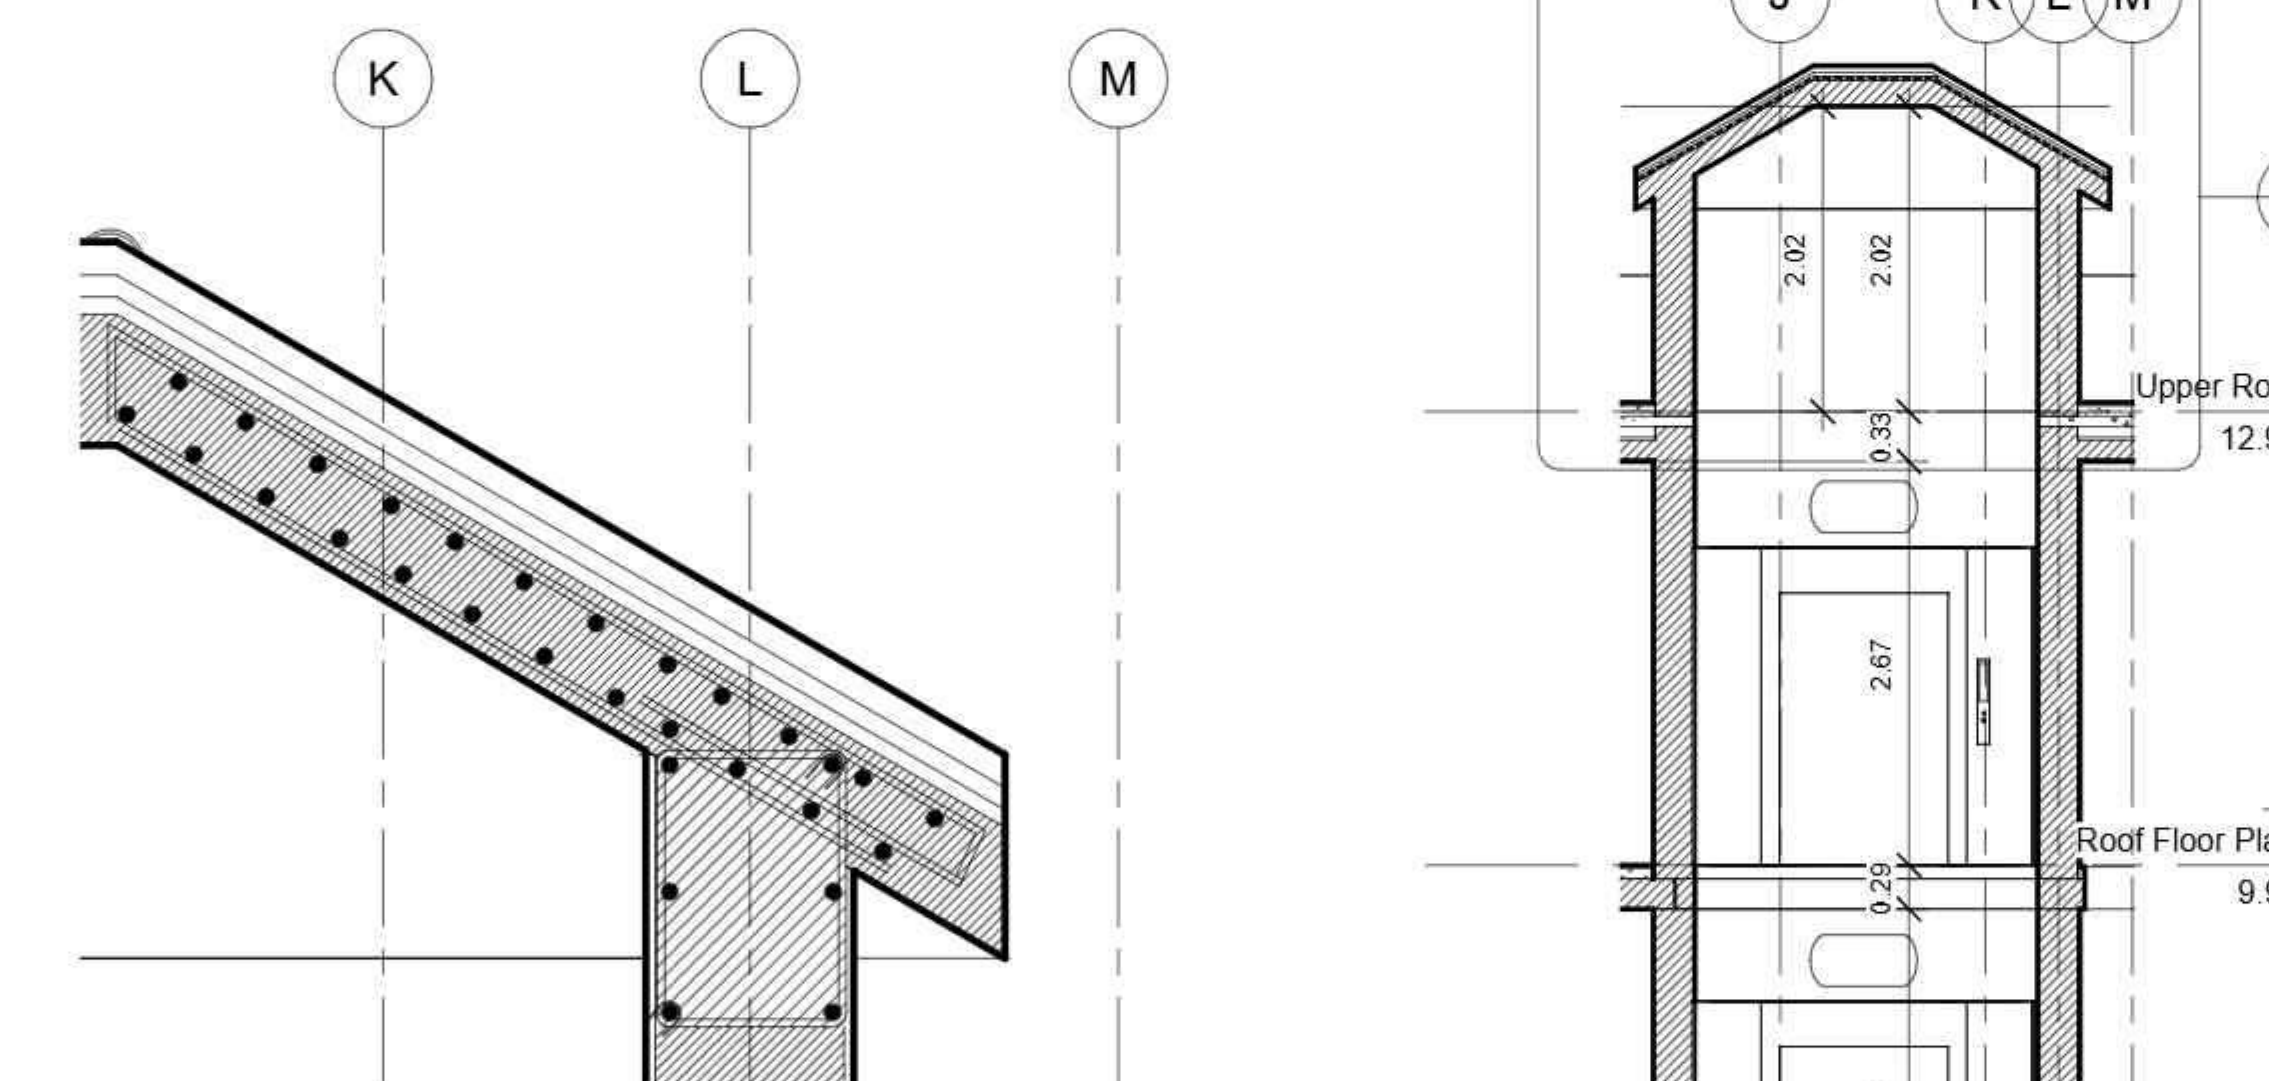


RC Steel Bars Detail
1 : 10

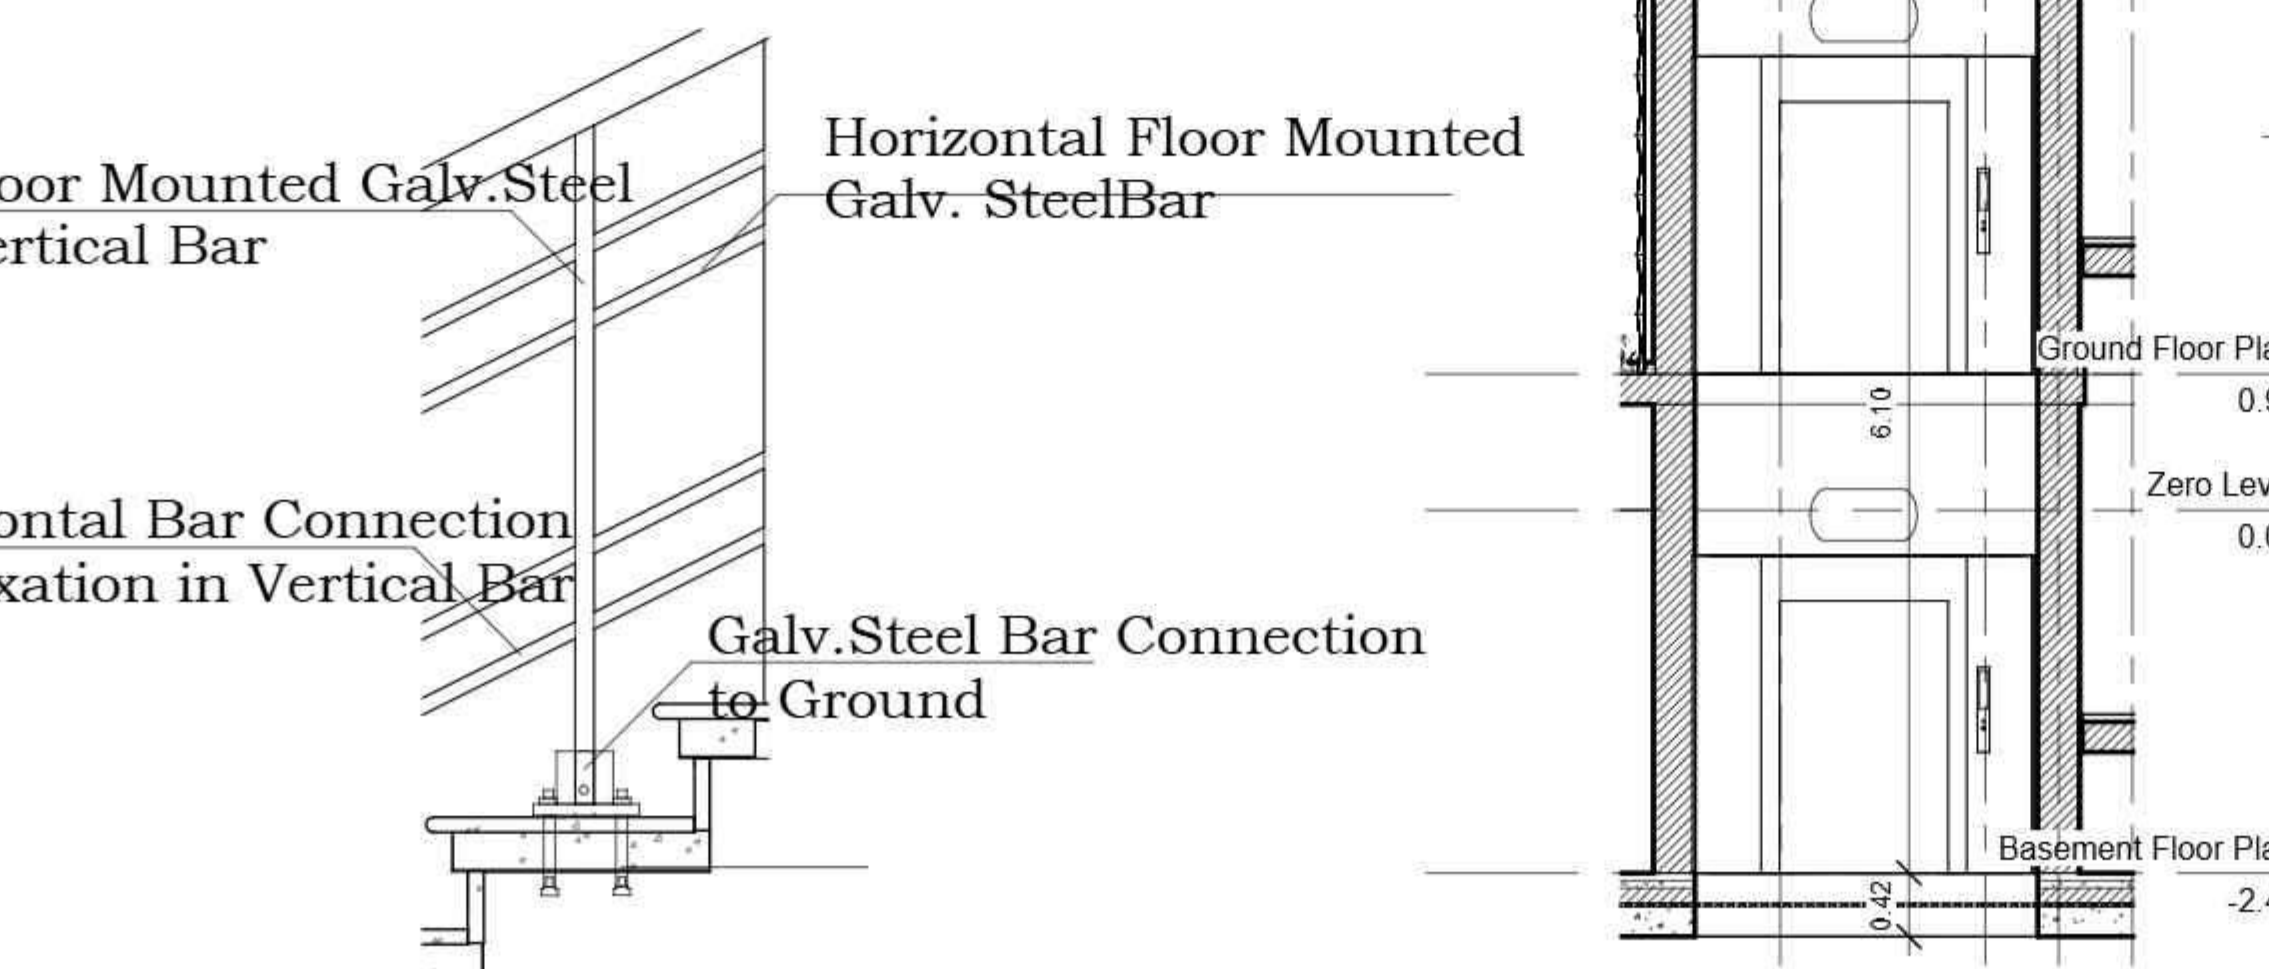

Floor Mounted Handrail
Detail
1 : 10

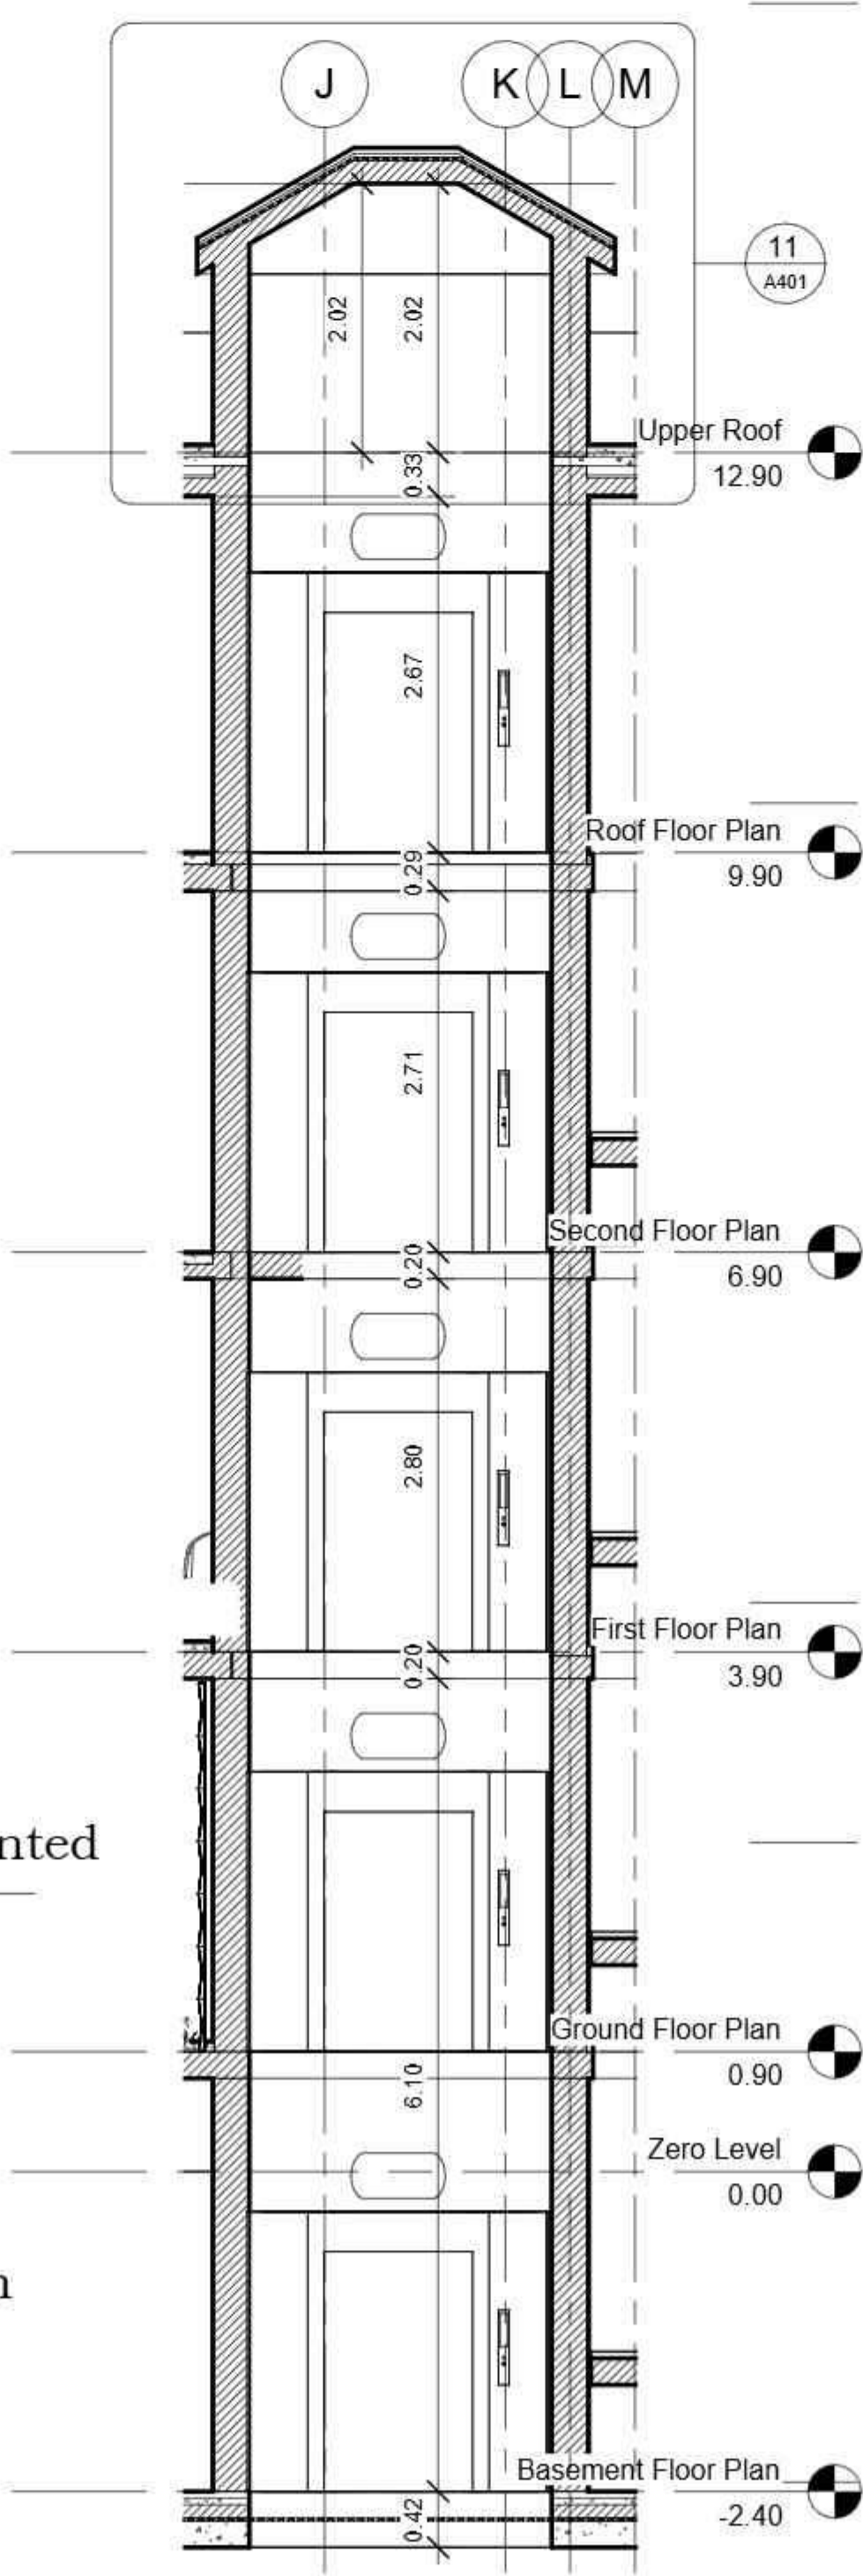


Elevator Section
1 : 50

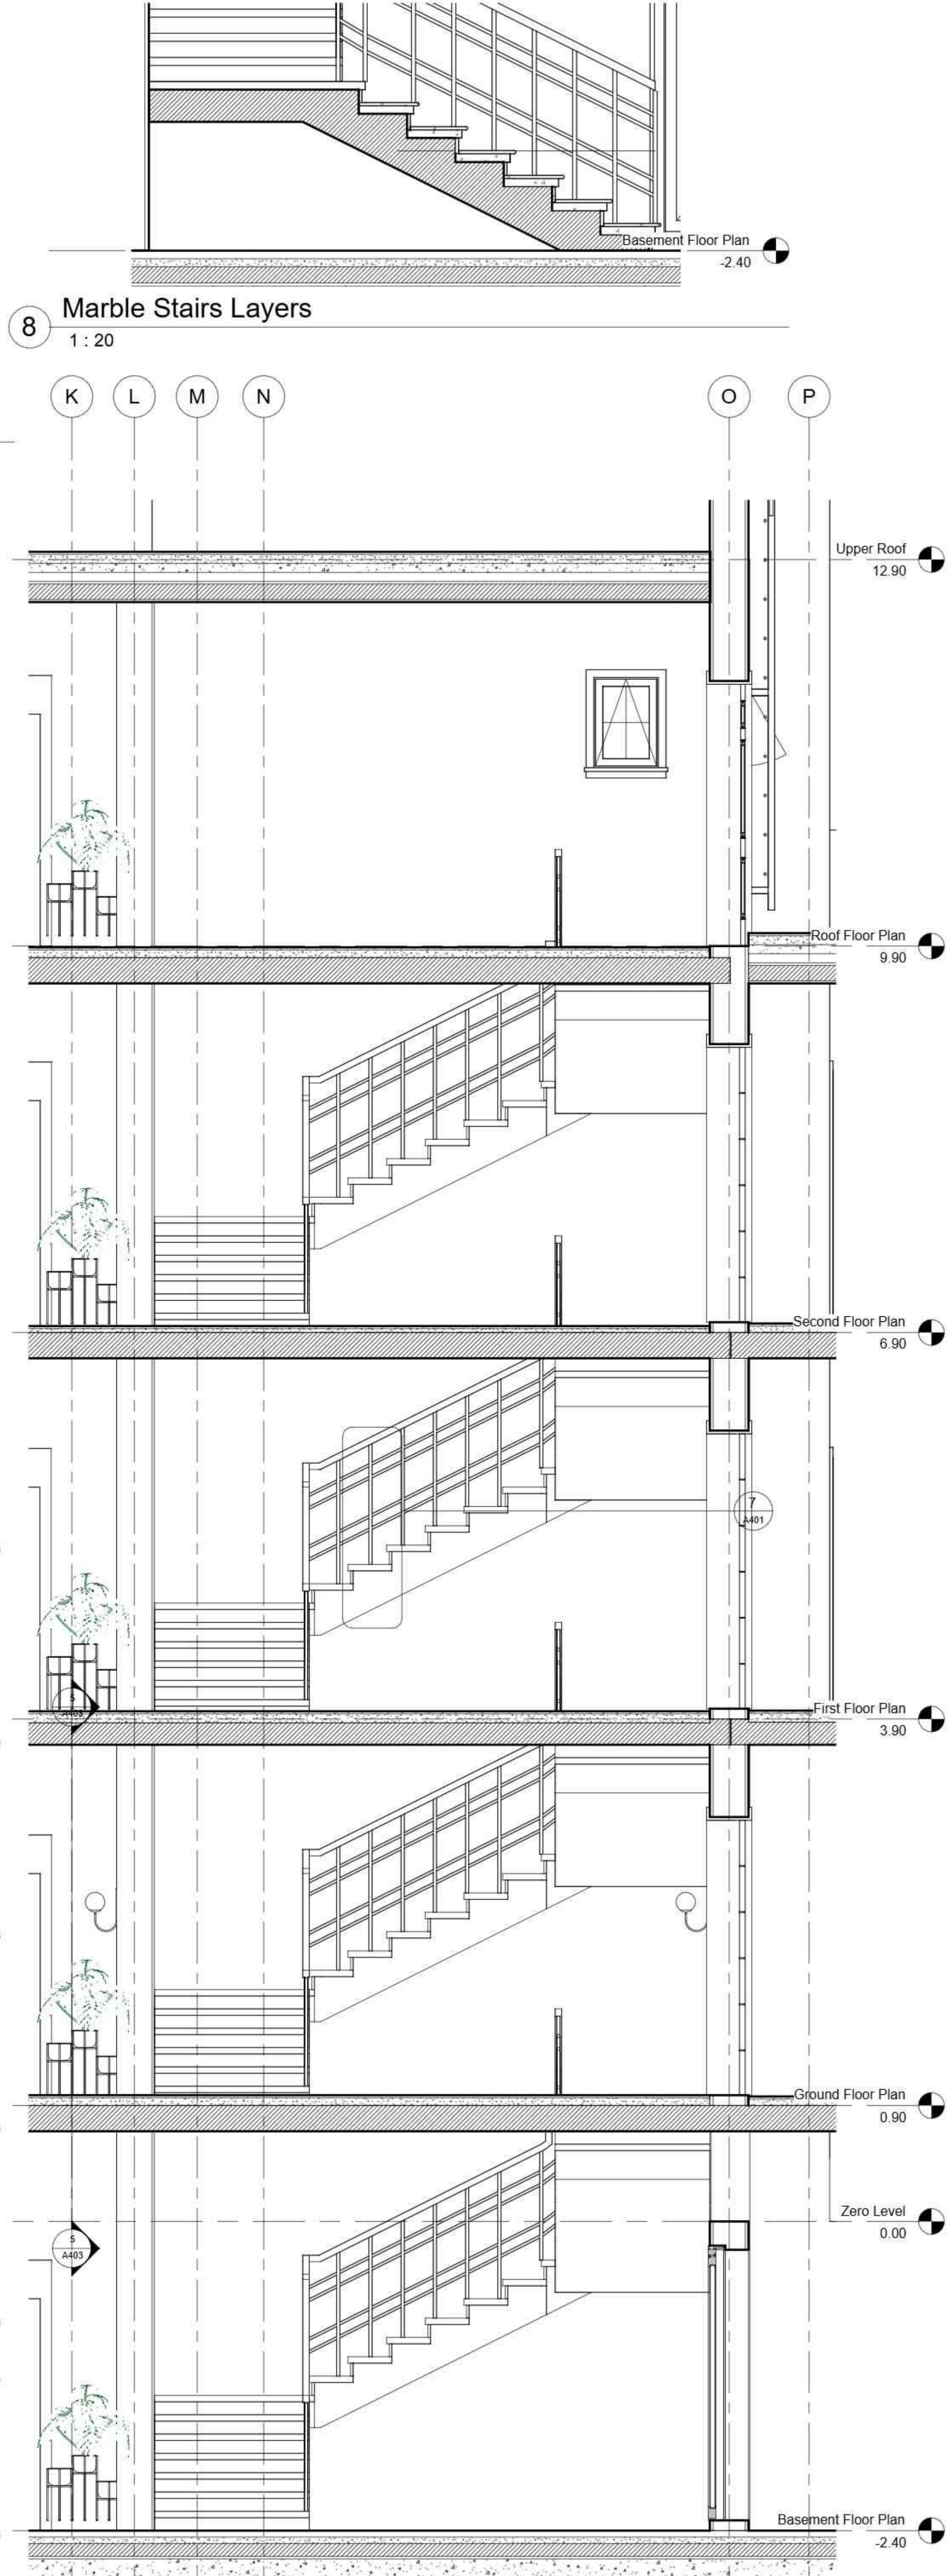

Section 13 - Callout 1
1 : 25

Marble Stairs Layers
1 : 20

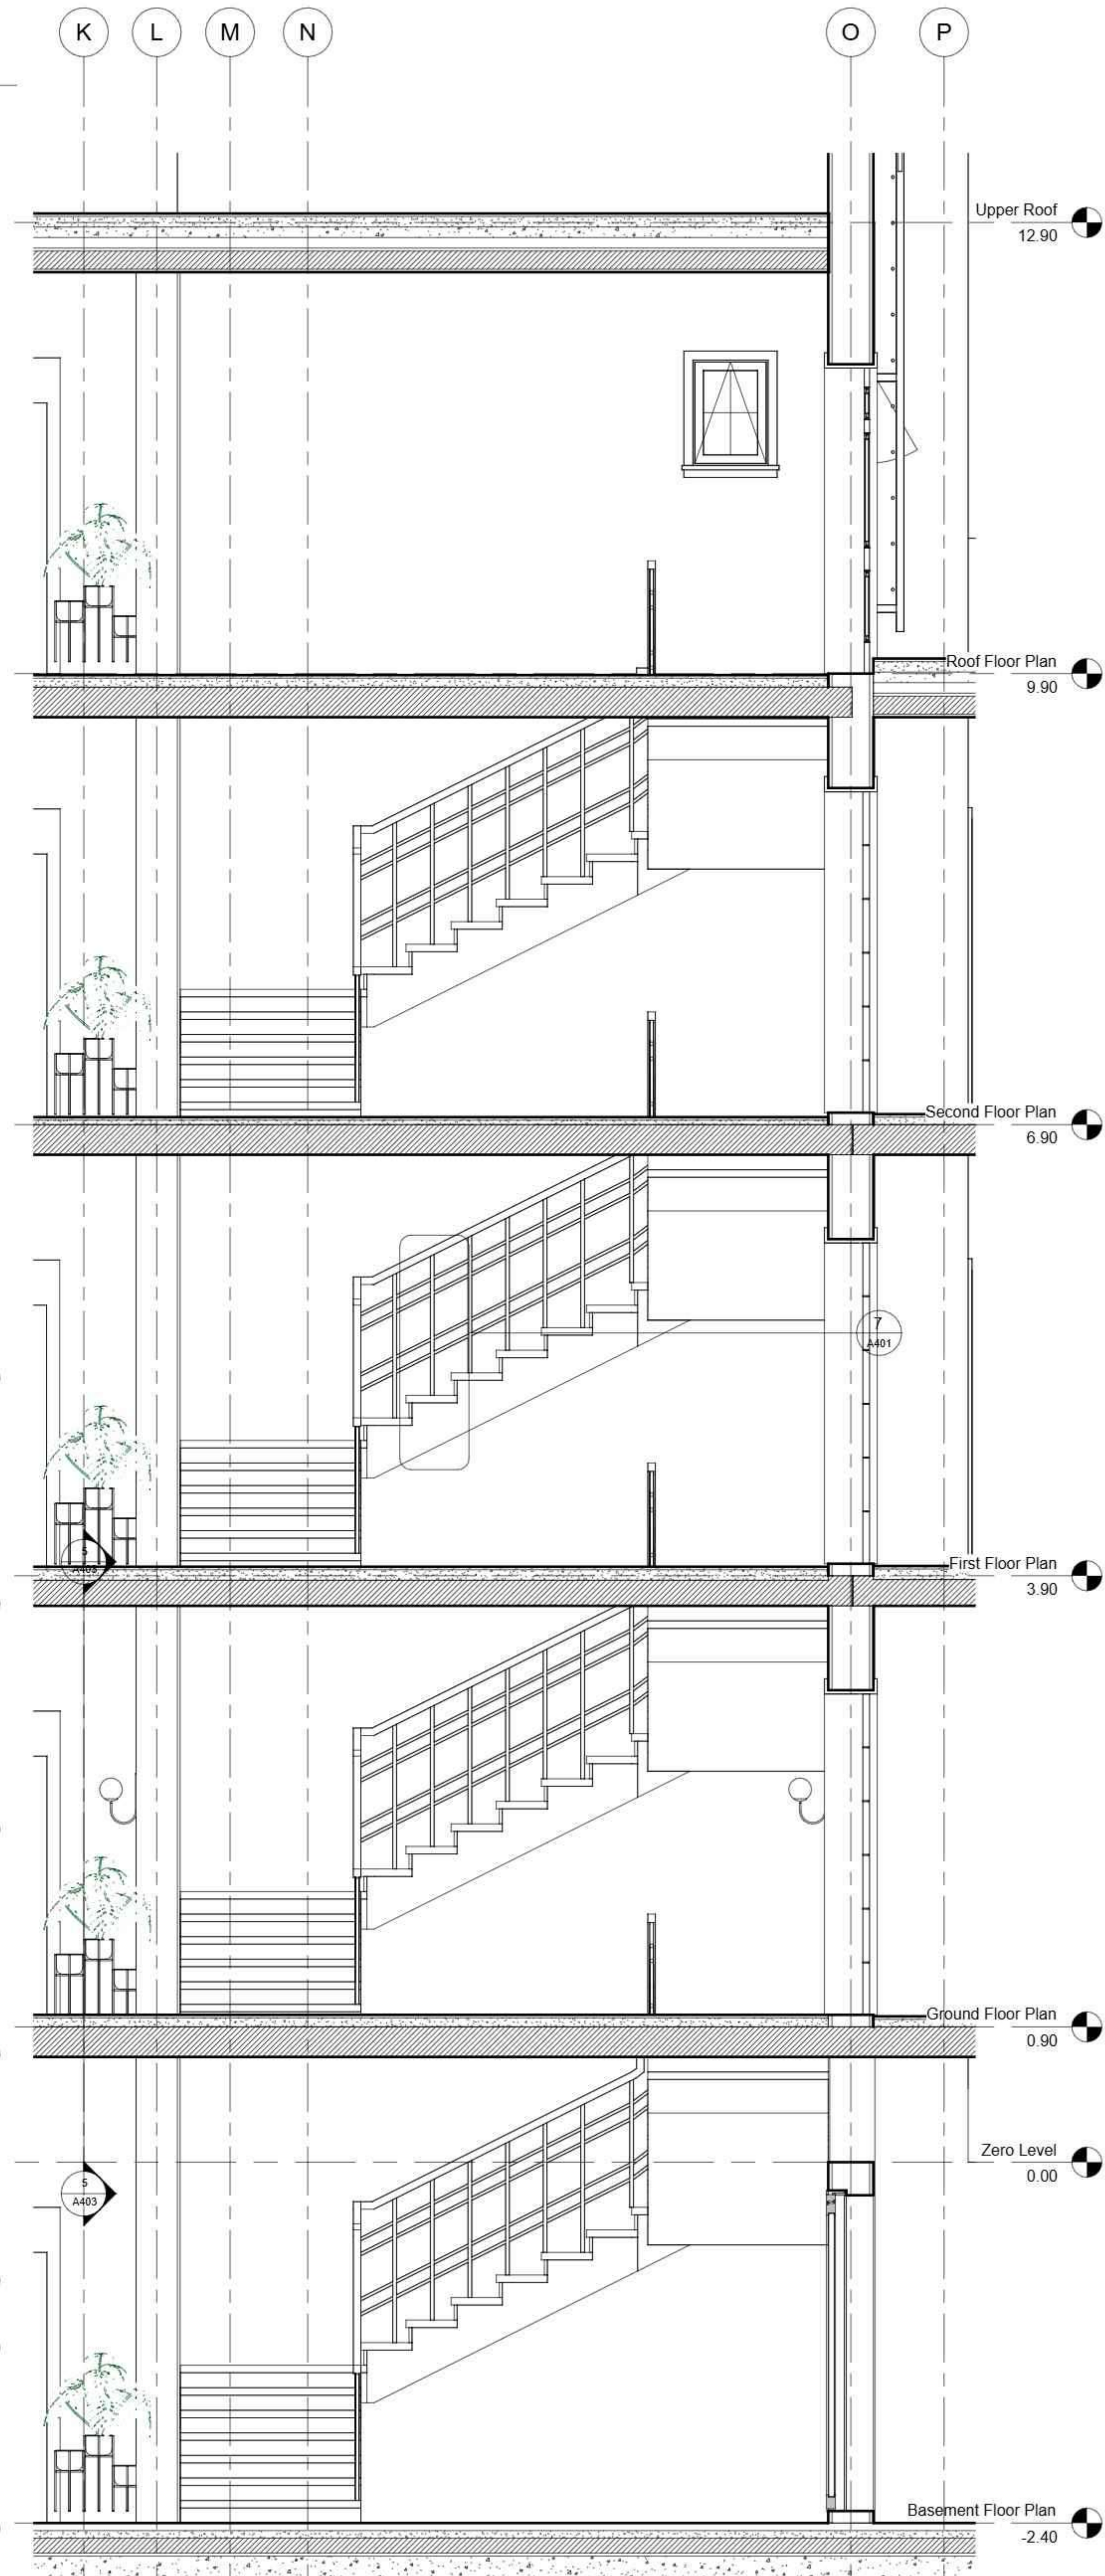

Marble Stairs Layers
1 : 20

Course Info:

ASE 464

Working Drawings III

GENERAL NOTES:

- ALL MATERIALS & WORK PRACTICES SHALL COMPLY WITH, BUT NOT LIMITED TO THE BUILDING REGULATION 2019, THE NATIONAL CONSTRUCTION CODE OF EGYPT UNLESS OTHERWISE SPECIFIED.

- ALL DIMENSIONS ARE IN METERS. IF IN DOUBT ASK, DO NOT SCALE.

- THESE DRAWINGS SHALL BE READ IN CONJUNCTION WITH ALL RELEVANT STRUCTURAL + ALL OTHER CONSULTANTS DRAWINGS/DETAILS & WITH ANY OTHER WRITTEN INSTRUCTIONS ISSUED IN THE COURSE OF THE CONTRACT.

- THESE DRAWINGS SHALL BE READ IN CONJUNCTION WITH ANY ENERGY RATING REPORT + SHALL BE CONSTRUCTED IN ACCORDANCE WITH THE STAMPED PLANS ENDORSED BY THE ACCREDITED THERMAL PERFORMANCE ASSESSOR WITHOUT ALTERATION



OWNER:



OCTOBER UNIVERSITY
FOR MODERN SCIENCES & ARTS
Architectural Engineering Department
Spring 2025

CLIENTS NAME:

Dr. Tarek Galal
Eng. Hend
Eng. Nermeen
Eng. Yousra


Student Name: Hadeel Zakaria
ID: 220009

PROJECT NAME:
APARTMENT BUILDING


SHEET NAME:
WALL SECTION 3 & DETAILS

SHEET NO: A305
SCALE: 1:25


DATE: 13-5-2025

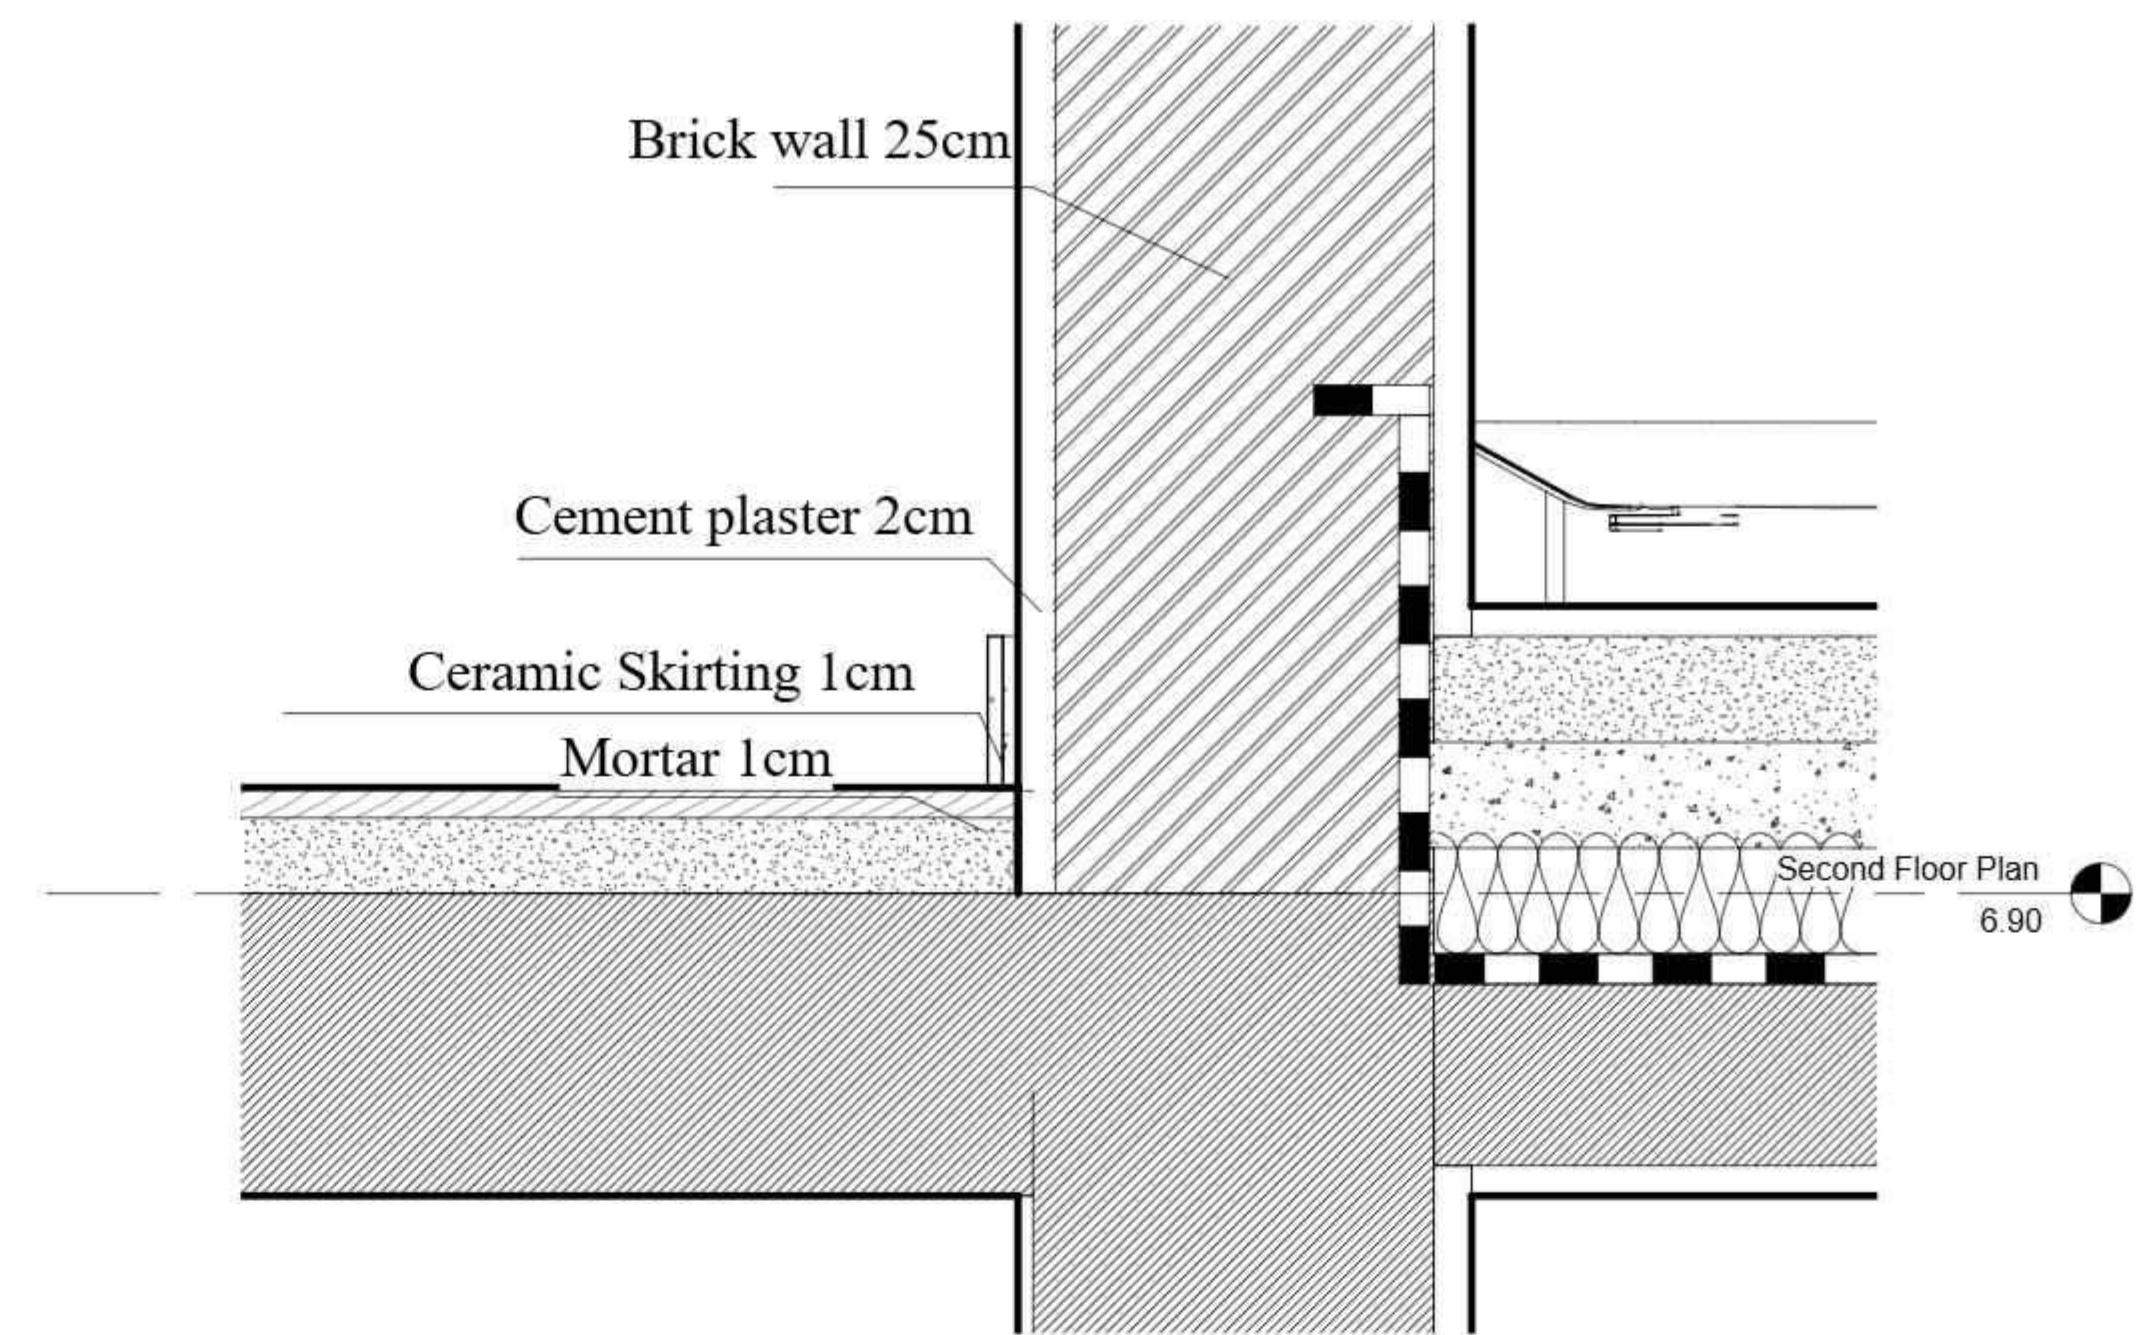

2 Skirting DETAIL
1 : 5

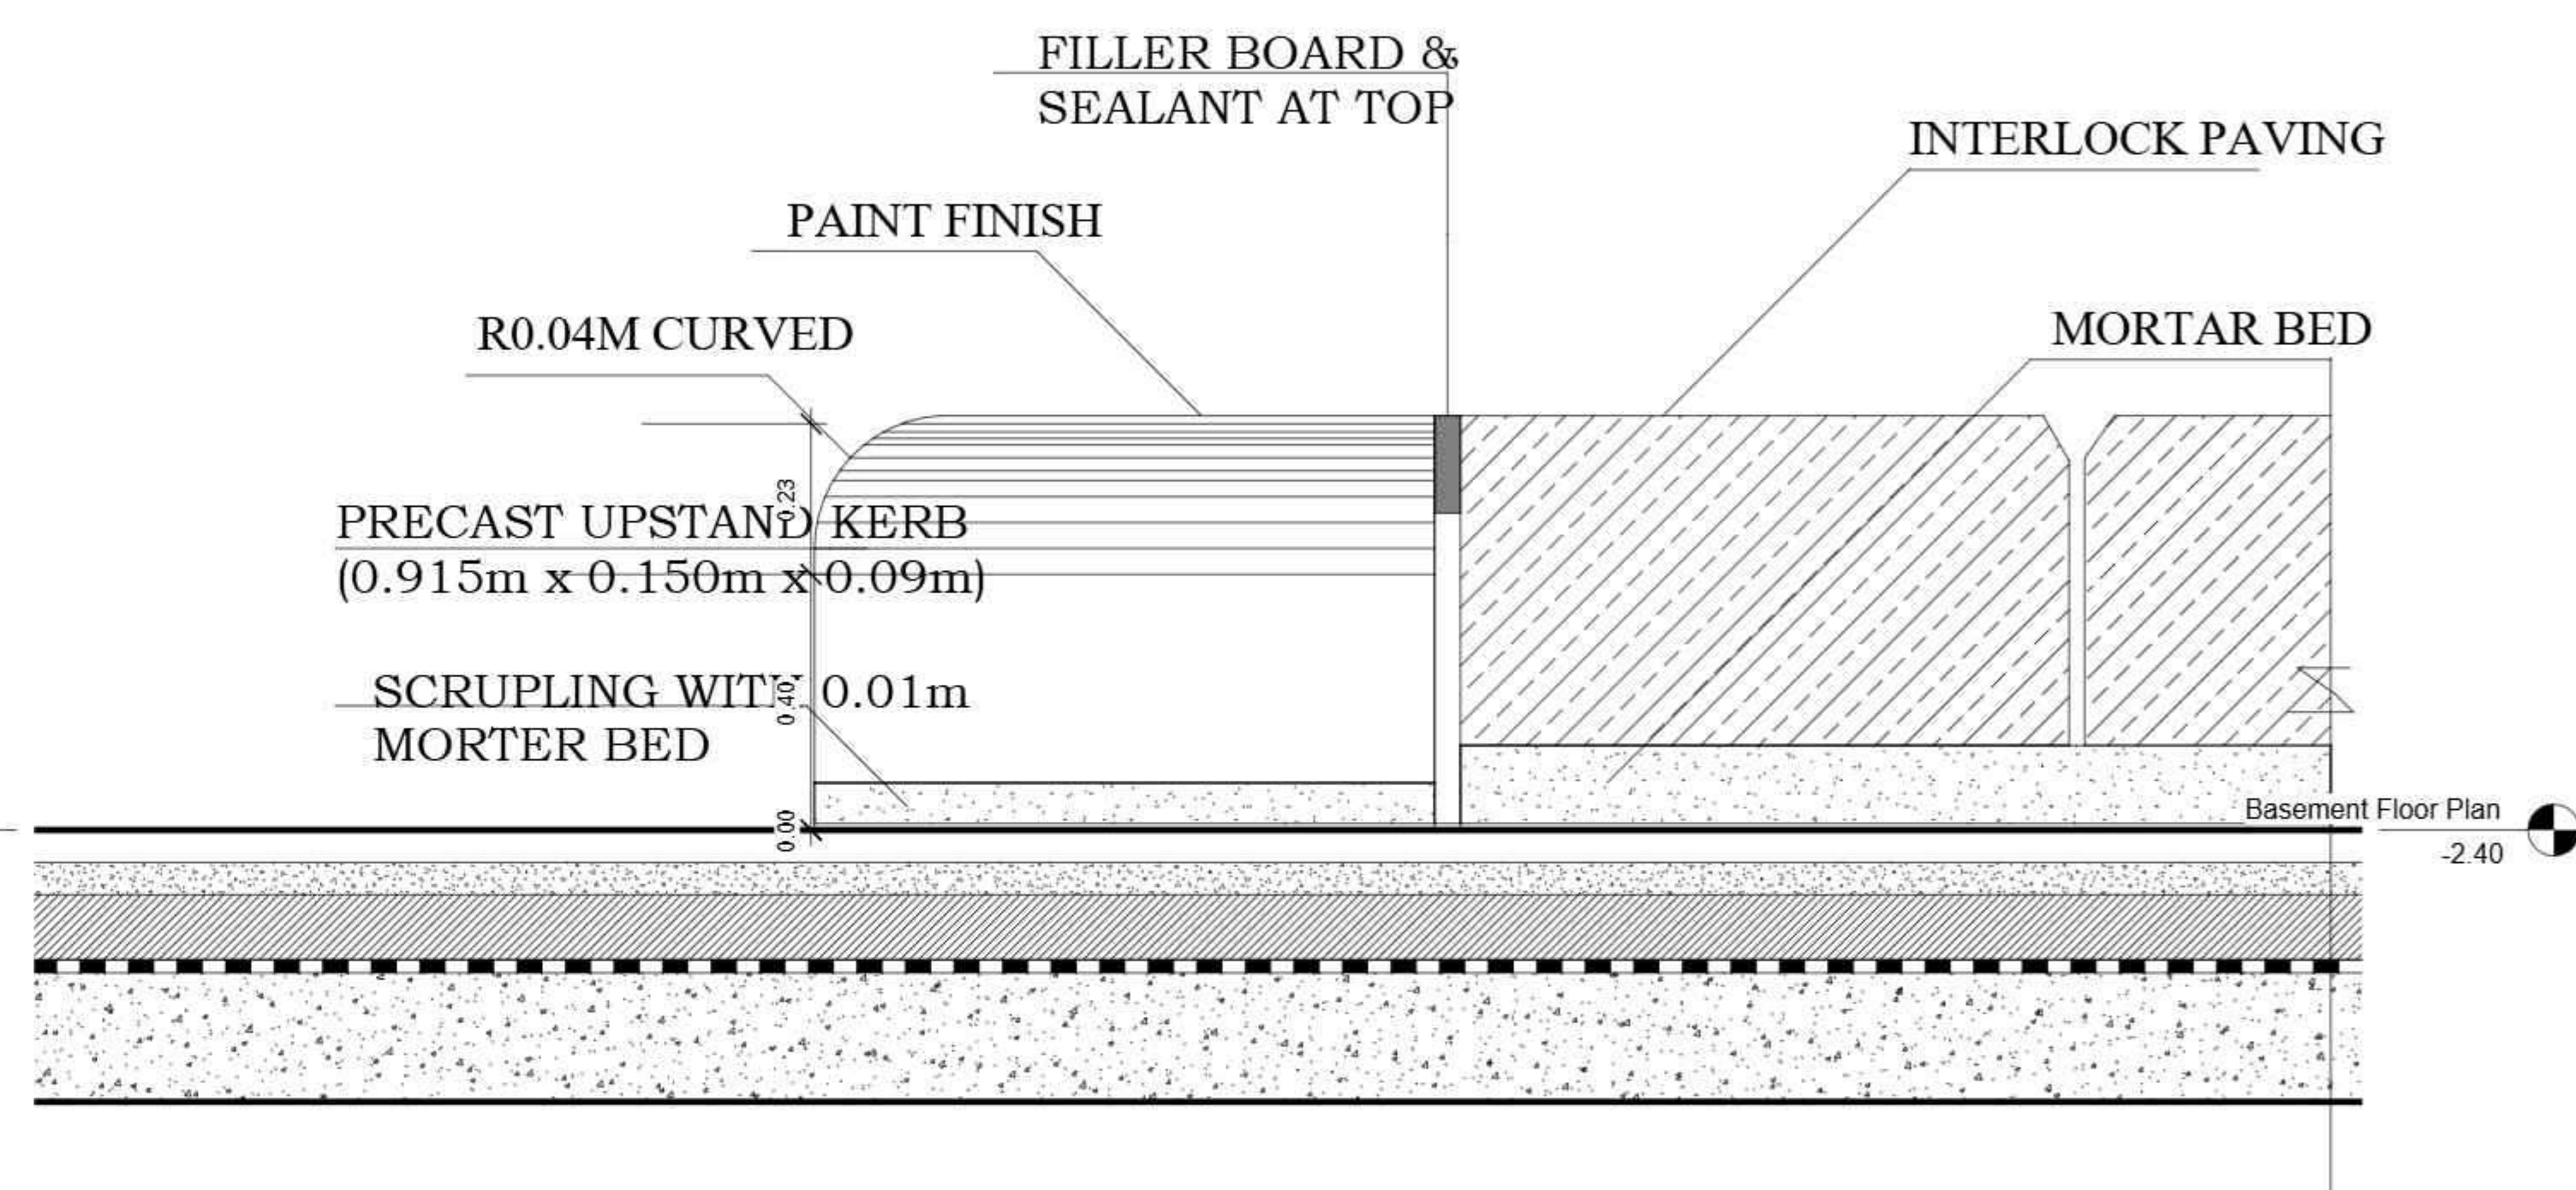


4 Kerb Detail
1 : 10

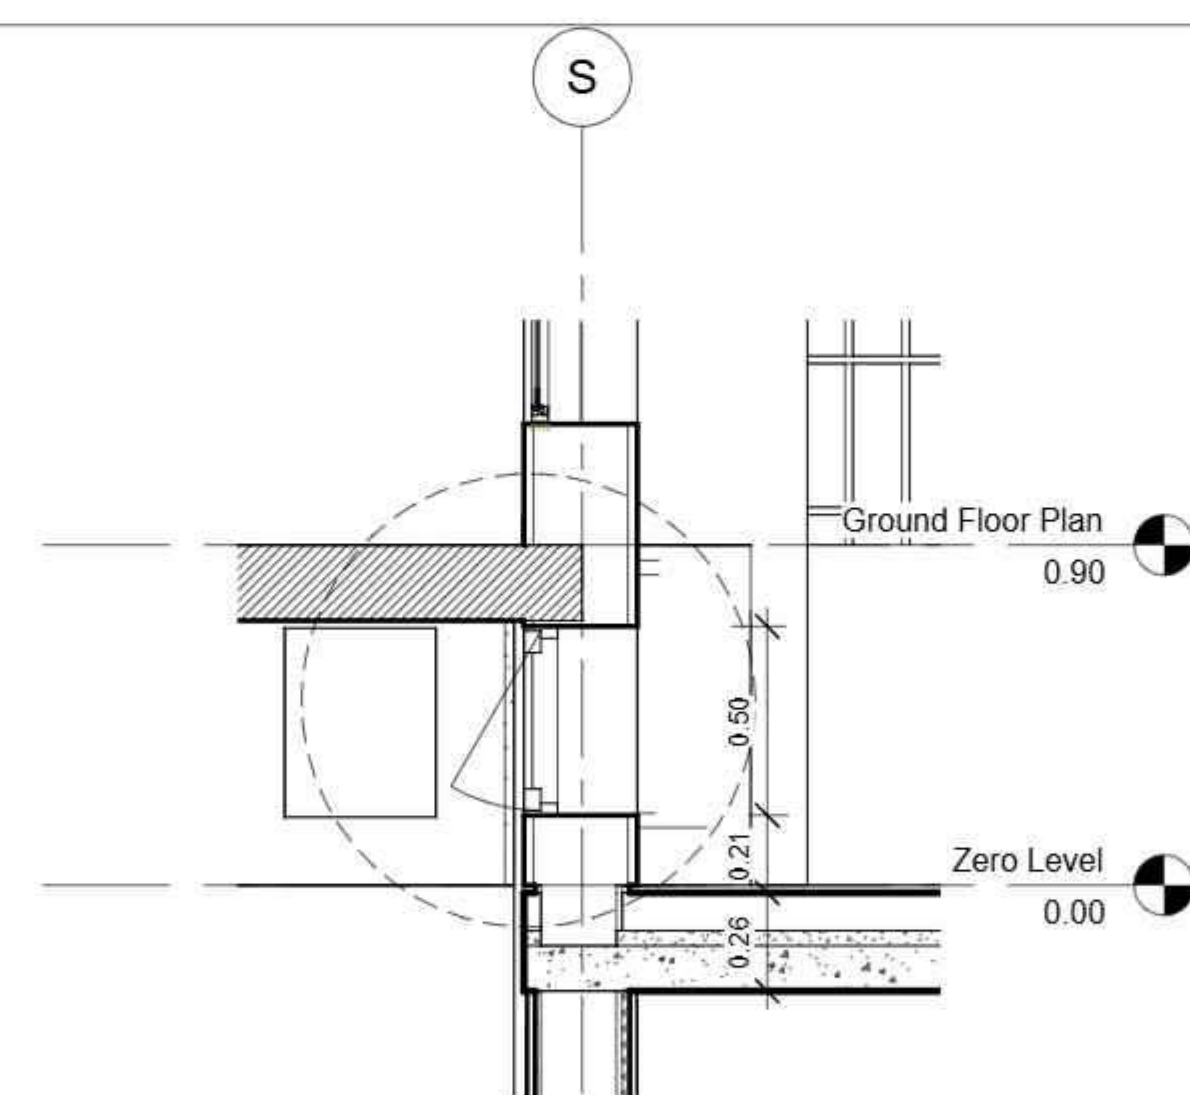

3 Basement Windows Details
1 : 20

Note: The windows are opened above the zero level with 0.18m. The window is placed at the very top leaving a sill height of 0.21m and 0m lintel to allow maximum rain protection and sunlight entry

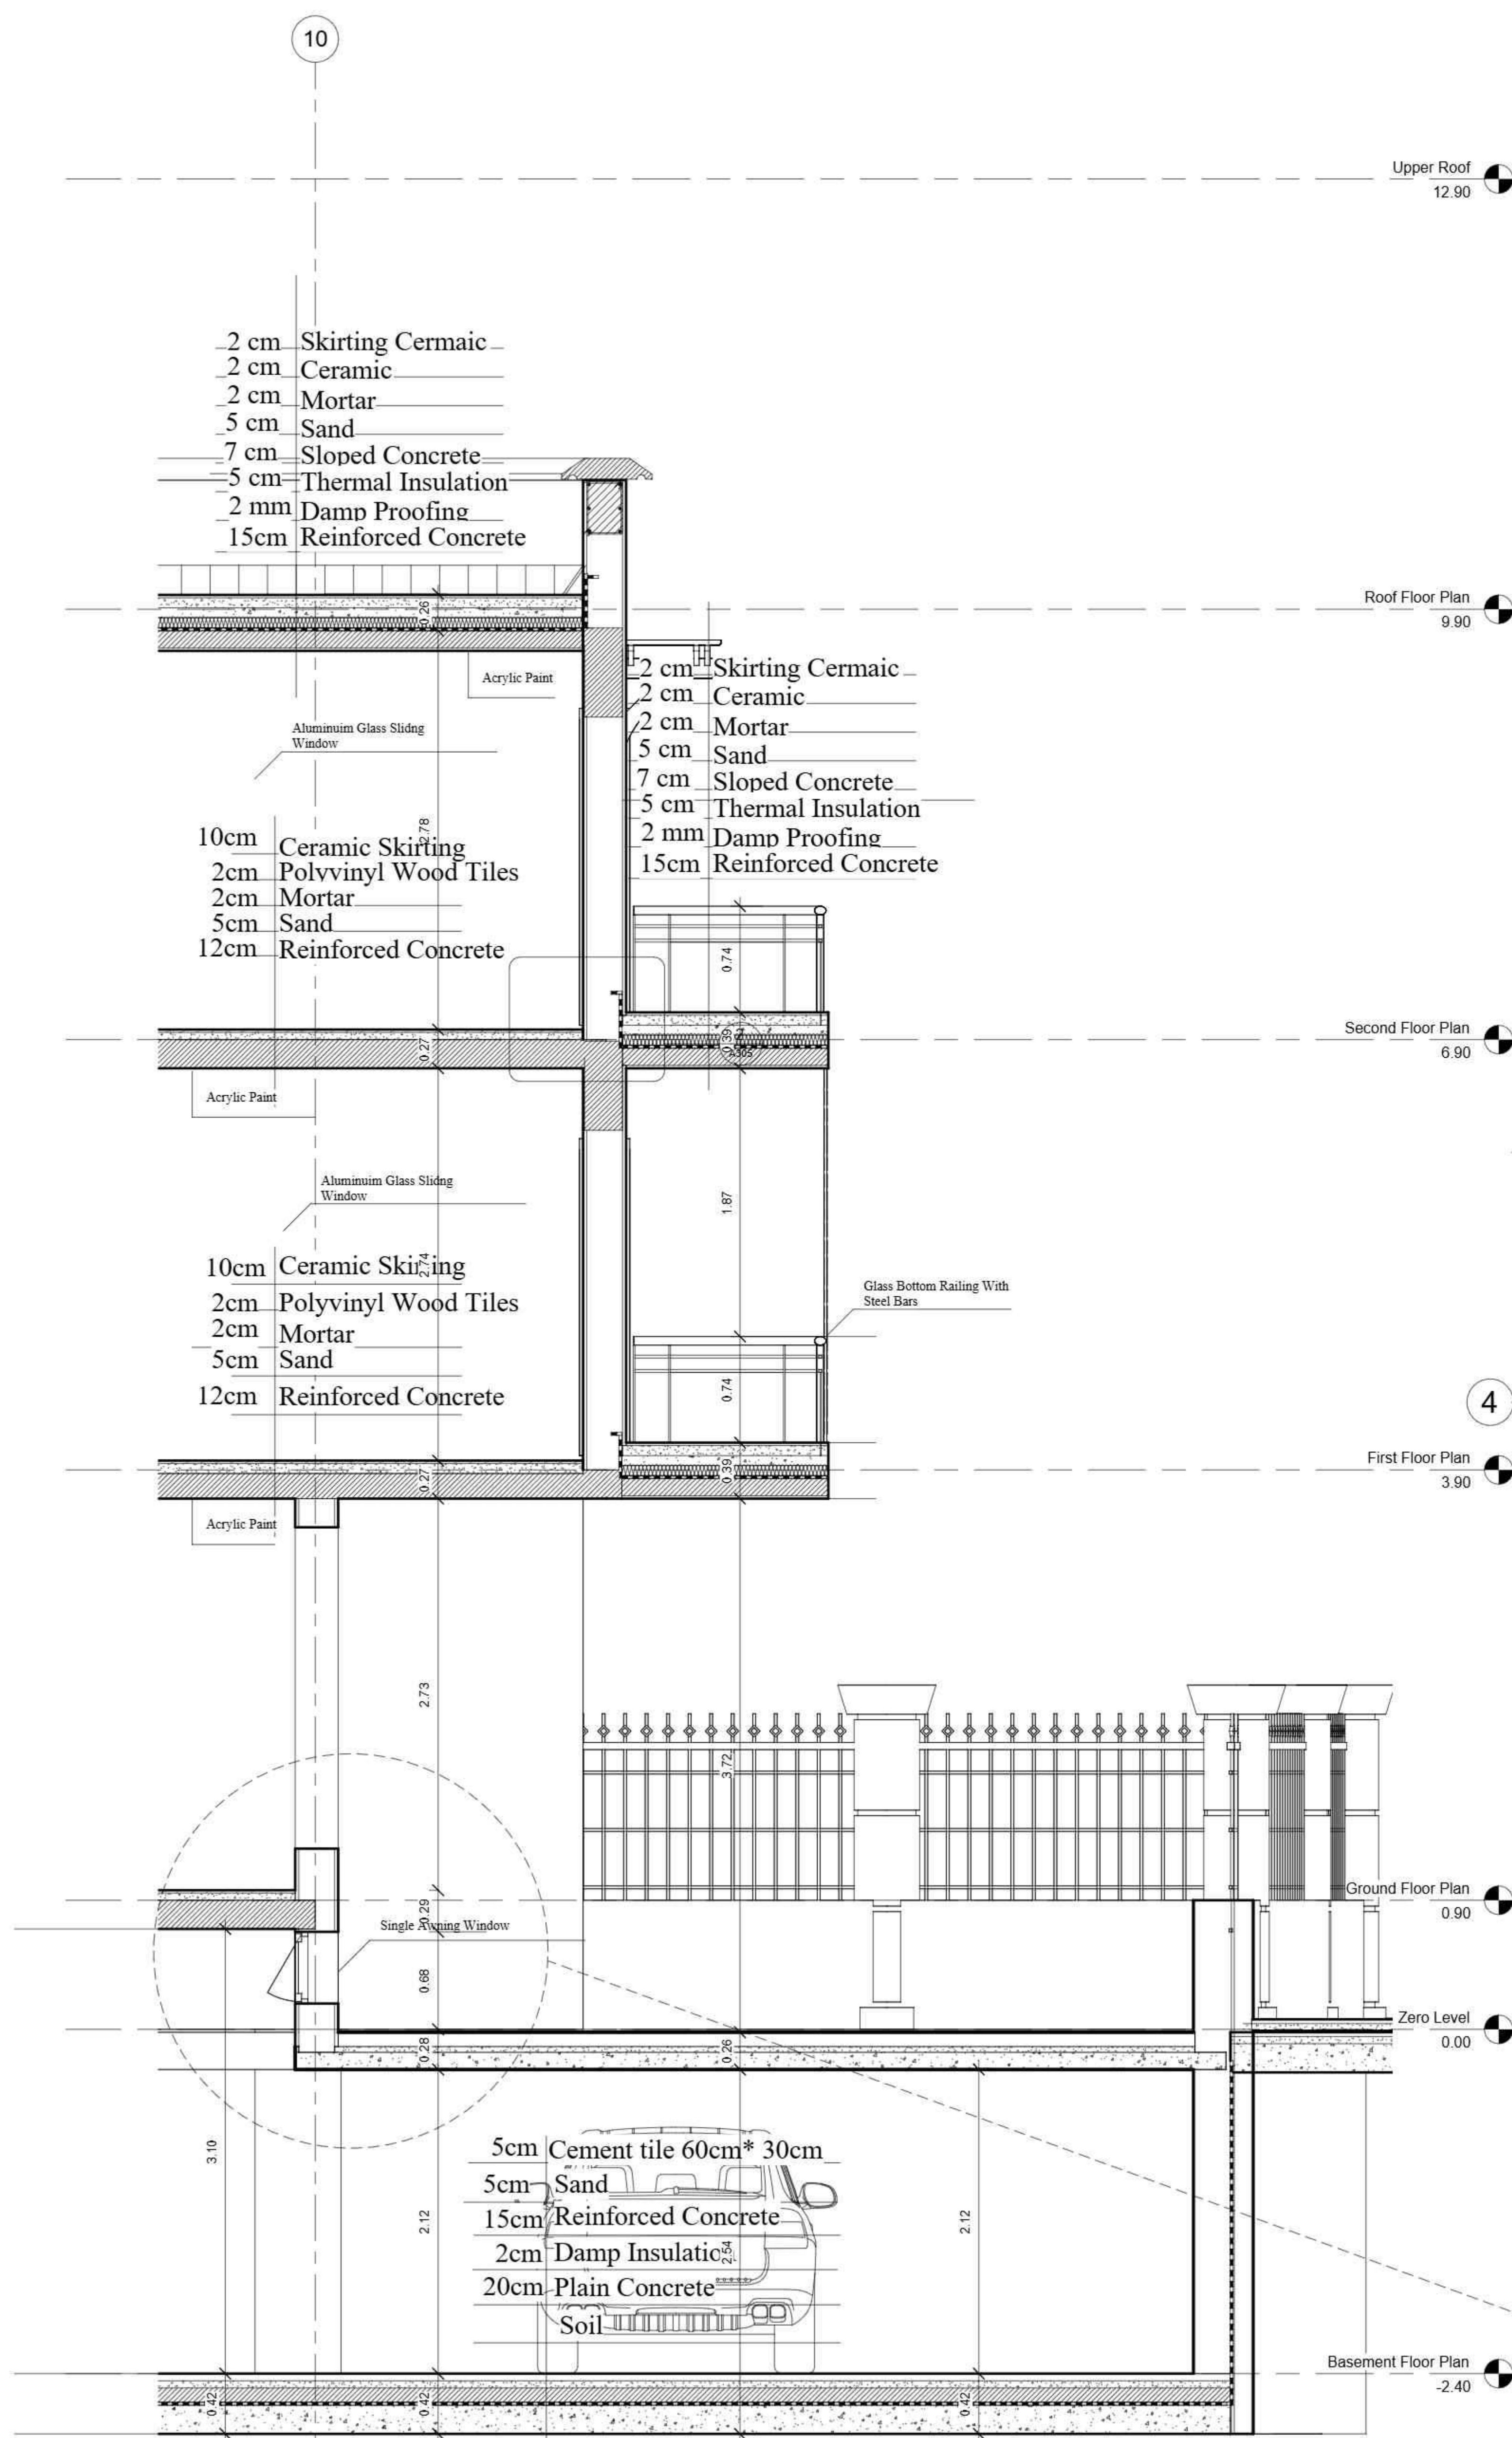

1 Wall Section 3
1 : 25

Course Info:
ASE 464
Working Drawings III

GENERAL NOTES:
- ALL MATERIALS & WORK PRACTICES SHALL COMPLY WITH, BUT NOT LIMITED TO THE BUILDING REGULATION 2019, THE NATIONAL CONSTRUCTION CODE OF EGYPT UNLESS OTHERWISE SPECIFIED.
- ALL DIMENSIONS ARE IN METERS. IF IN DOUBT ASK, DO NOT SCALE.
- THESE DRAWINGS SHALL BE READ IN CONJUNCTION WITH ALL RELEVANT STRUCTURAL + ALL OTHER CONSULTANTS DRAWINGS/DETAILS & WITH ANY OTHER WRITTEN INSTRUCTIONS ISSUED IN THE COURSE OF THE CONTRACT.
- THESE DRAWINGS SHALL BE READ IN CONJUNCTION WITH ANY ENERGY RATING REPORT + SHALL BE CONSTRUCTED IN ACCORDANCE WITH THE STAMPED PLANS ENDORSED BY THE ACCREDITED THERMAL PERFORMANCE ASSESSOR WITHOUT ALTERATION



OWNER:
MSA UNIVERSITY
جامعة أكتوبر للعلوم الحديثة والآداب
UNIVERSITY of GREENWICH
OCTOBER UNIVERSITY
FOR MODERN SCIENCES & ARTS
Architectural Engineering Department
Spring 2025

CLIENTS NAME:
Dr. Tarek Galal
Eng. Hend
Eng. Nermeen
Eng. Yousra


Student Name: Hadeel Zakaria
ID: 220009

PROJECT NAME:
APARTMENT BUILDING


SHEET NAME:
WALL SECTION 1 &
DETAILS

SHEET NO: A303
SCALE: 1:25


DATE: 13-5-2025

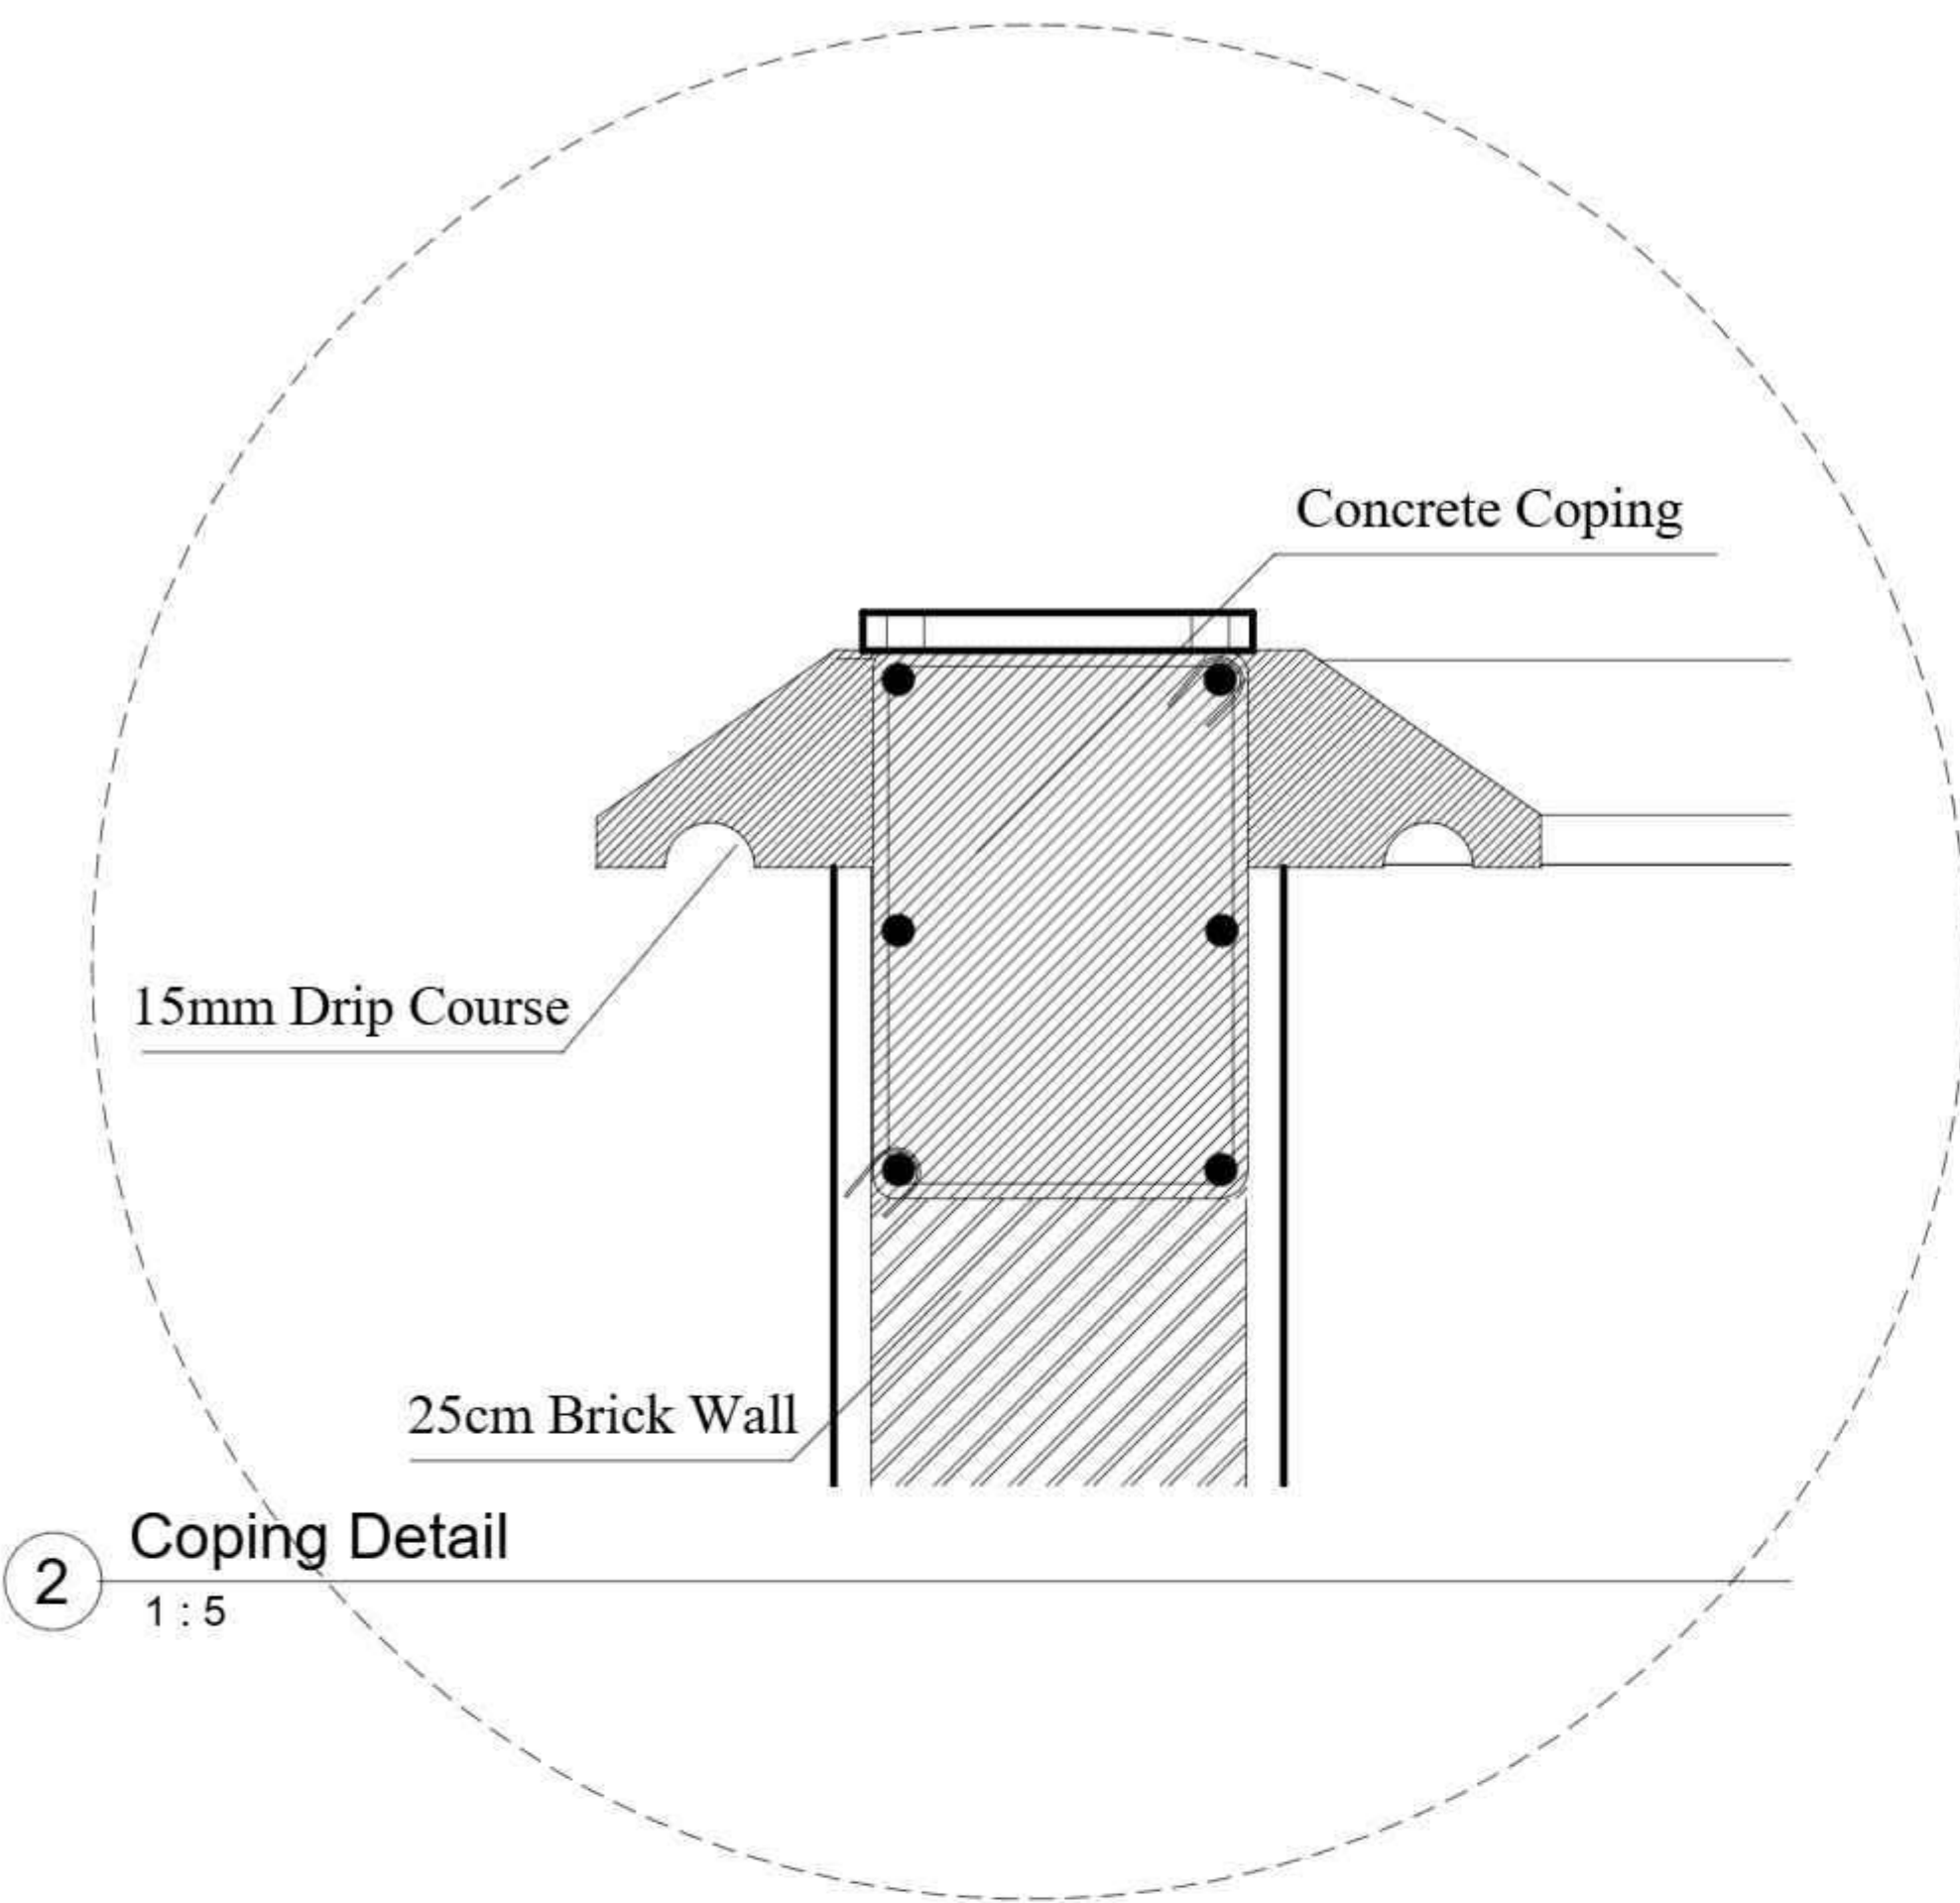

2 Coping Detail
1:5

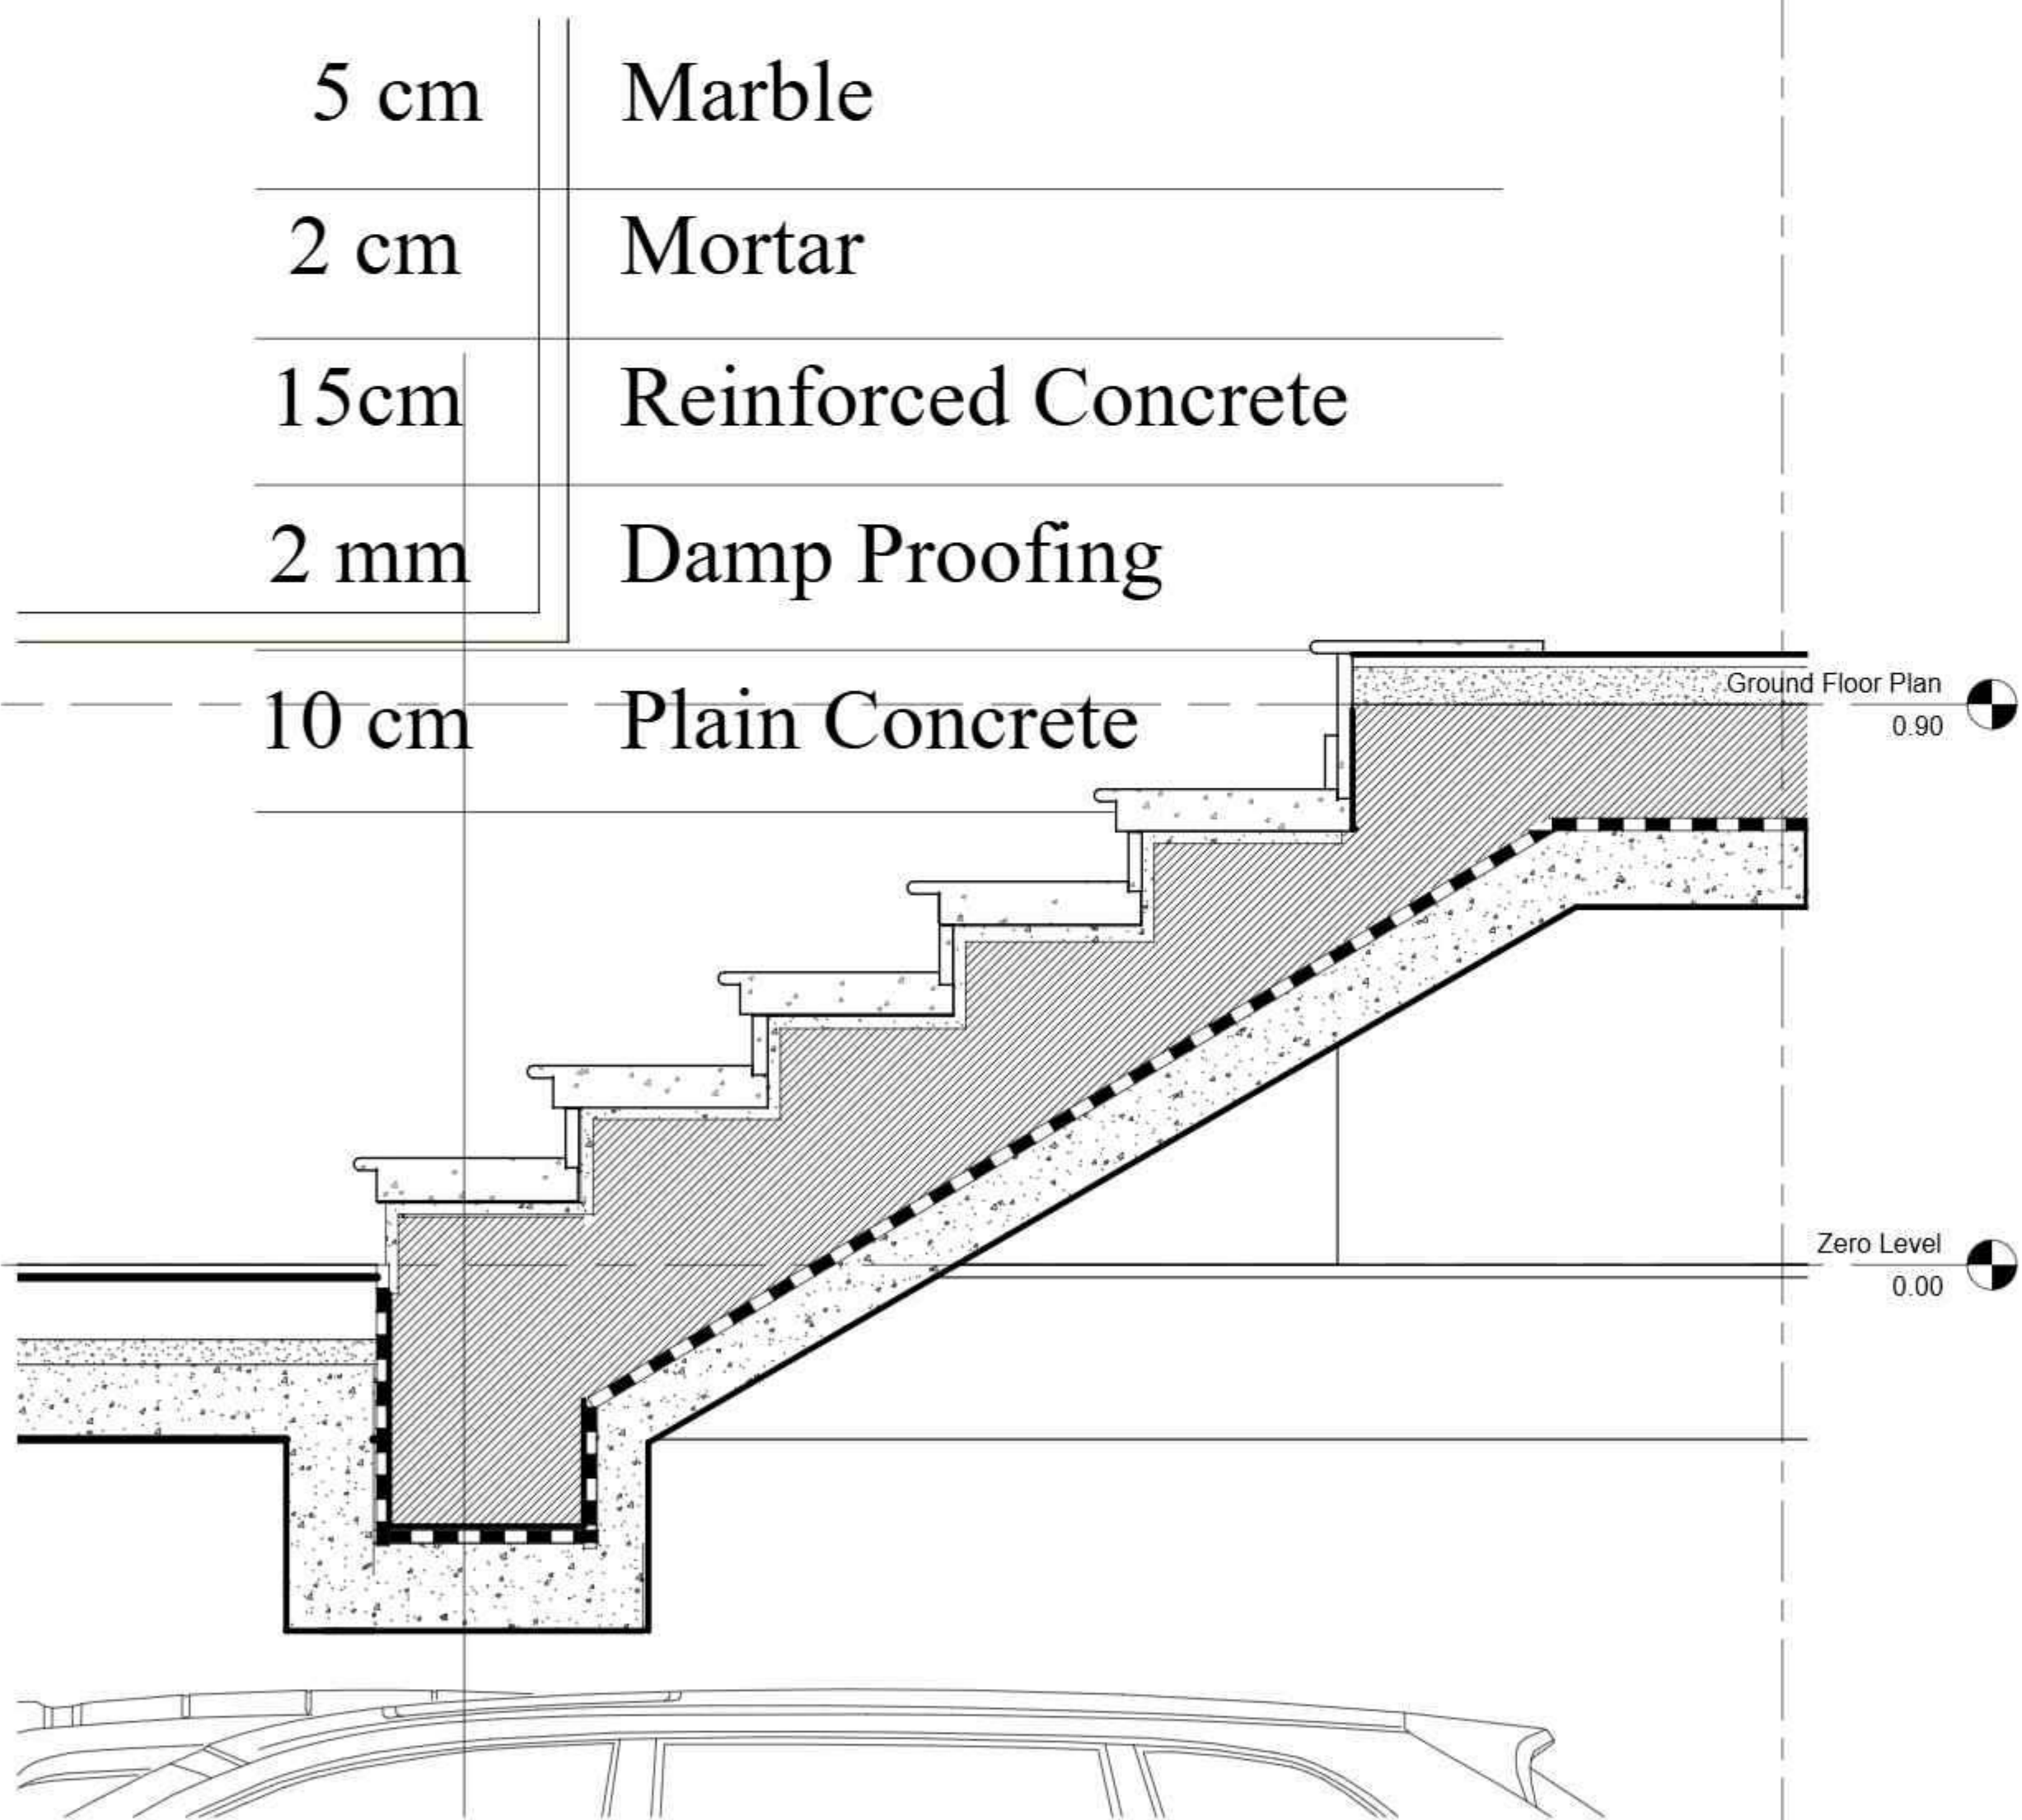

3 Entrance Wall Section -
Callout 1
1:10

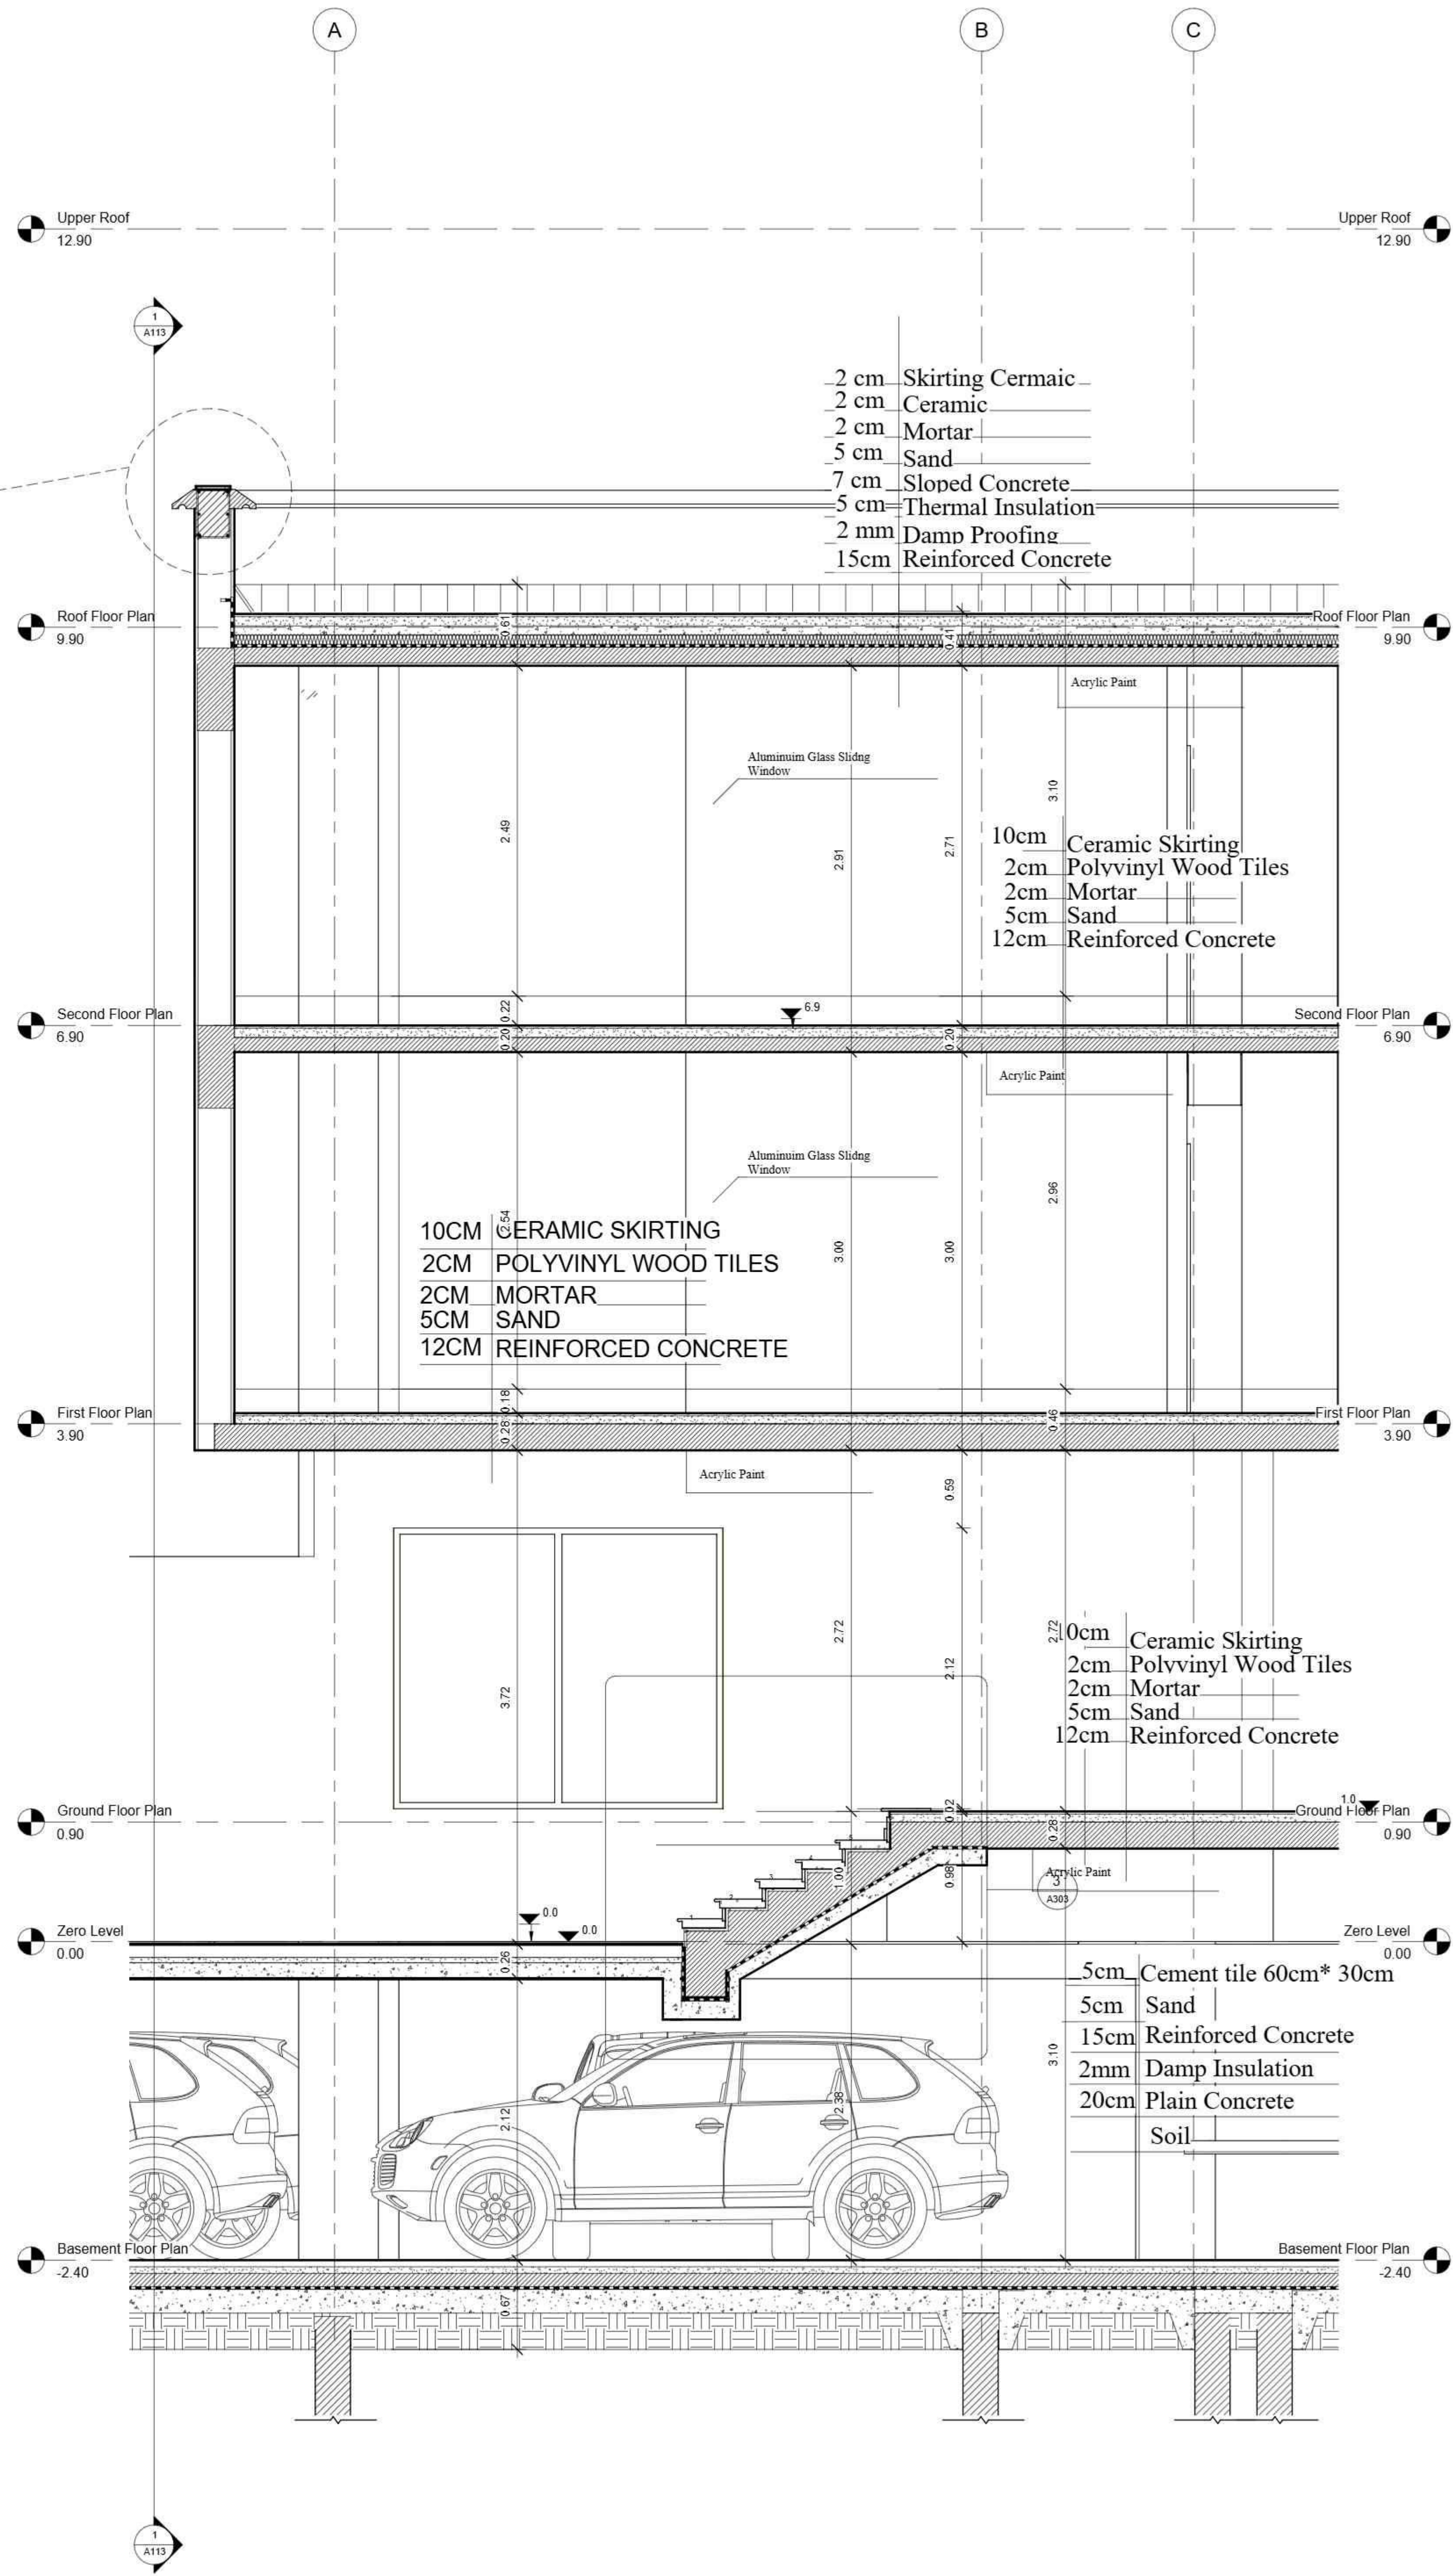

1 Entrance Wall Section
1:25

GENERAL NOTES:

- ALL MATERIALS & WORK PRACTICES SHALL COMPLY WITH, BUT NOT LIMITED TO THE BUILDING REGULATION 2019, THE NATIONAL CONSTRUCTION CODE OF EGYPT UNLESS OTHERWISE SPECIFIED.

- ALL DIMENSIONS ARE IN METERS. IF IN DOUBT ASK, DO NOT SCALE.

- THESE DRAWINGS SHALL BE READ IN CONJUNCTION WITH ALL RELEVANT STRUCTURAL + ALL OTHER CONSULTANTS DRAWINGS/DETAILS & WITH ANY OTHER WRITTEN INSTRUCTIONS ISSUED IN THE COURSE OF THE CONTRACT.

- THESE DRAWINGS SHALL BE READ IN CONJUNCTION WITH ANY ENERGY RATING REPORT + SHALL BE CONSTRUCTED IN ACCORDANCE WITH THE STAMPED PLANS ENDORSED BY THE ACCREDITED THERMAL PERFORMANCE ASSESSOR WITHOUT ALTERATION



OWNER:

OCTOBER UNIVERSITY
FOR MODERN SCIENCES & ARTS
Architectural Engineering Department
Spring 2025

CLIENTS NAME:

Dr. Tarek Galal
Eng. Hend
Eng. Nermeen
Eng. Yousra

Student Name: Hadeel Zakaria

ID: 220009

PROJECT NAME:
APARTMENT BUILDING

SHEET NAME:
DETAILS



SHEET NO:

A403


SCALE:

1:-


DATE: 13-5-2025

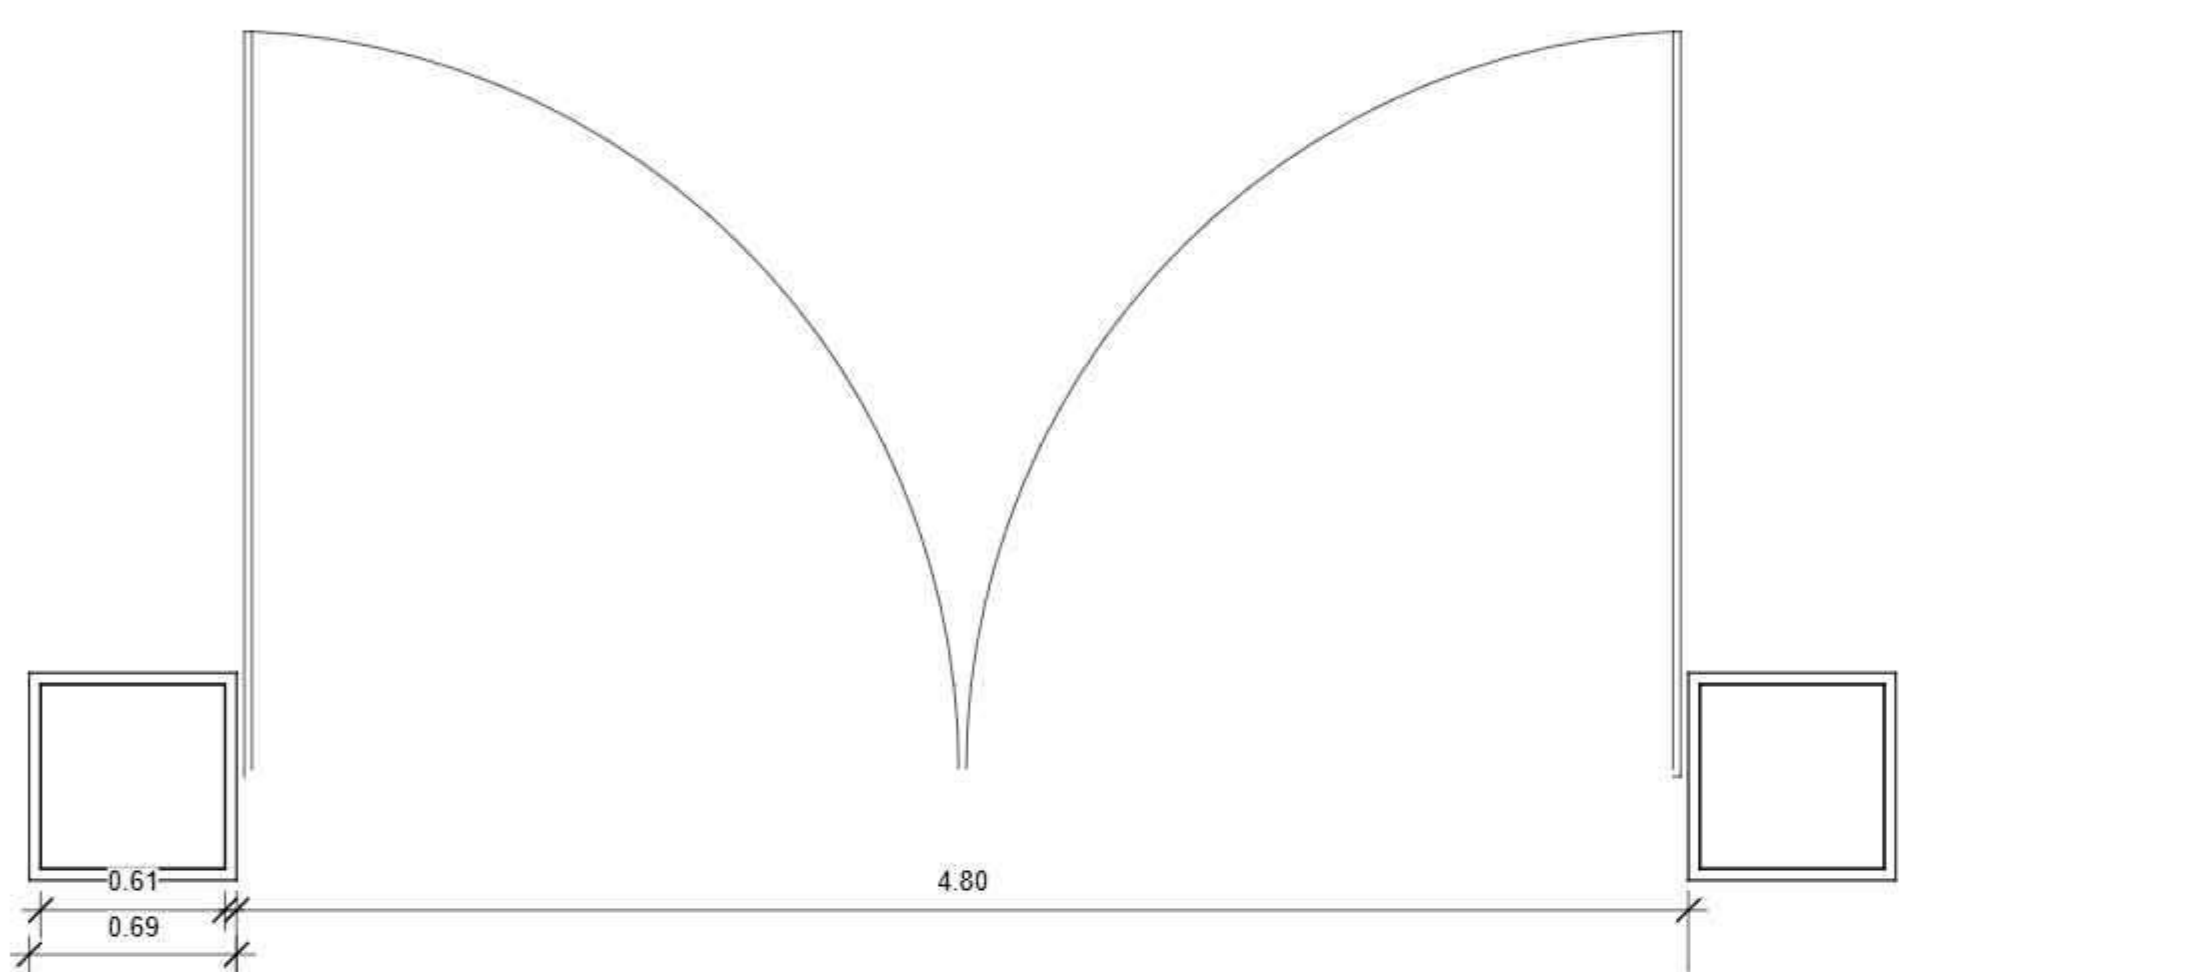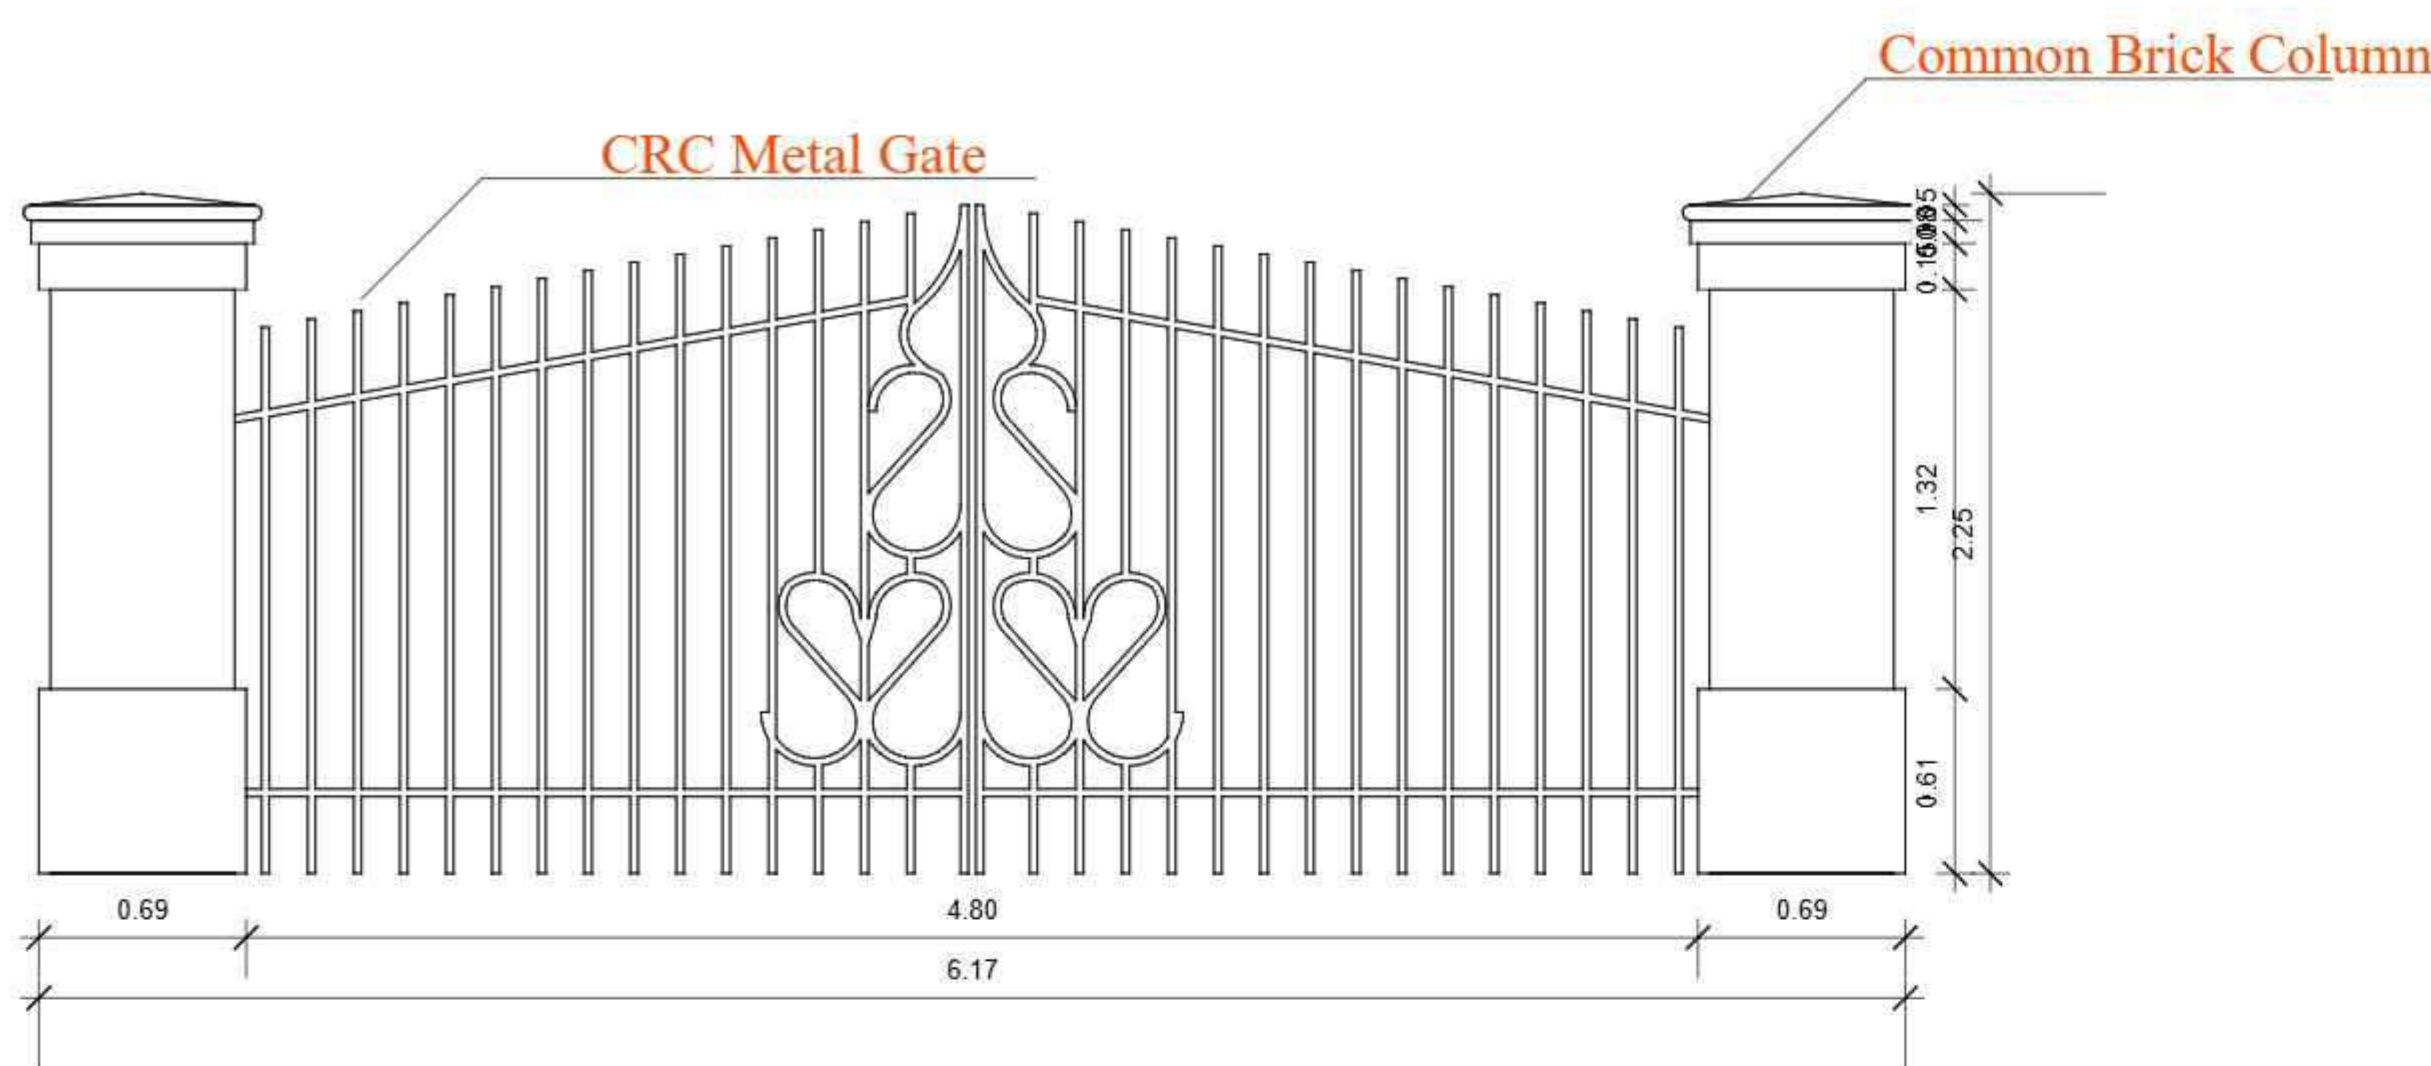


Entrance fence
1 : 25

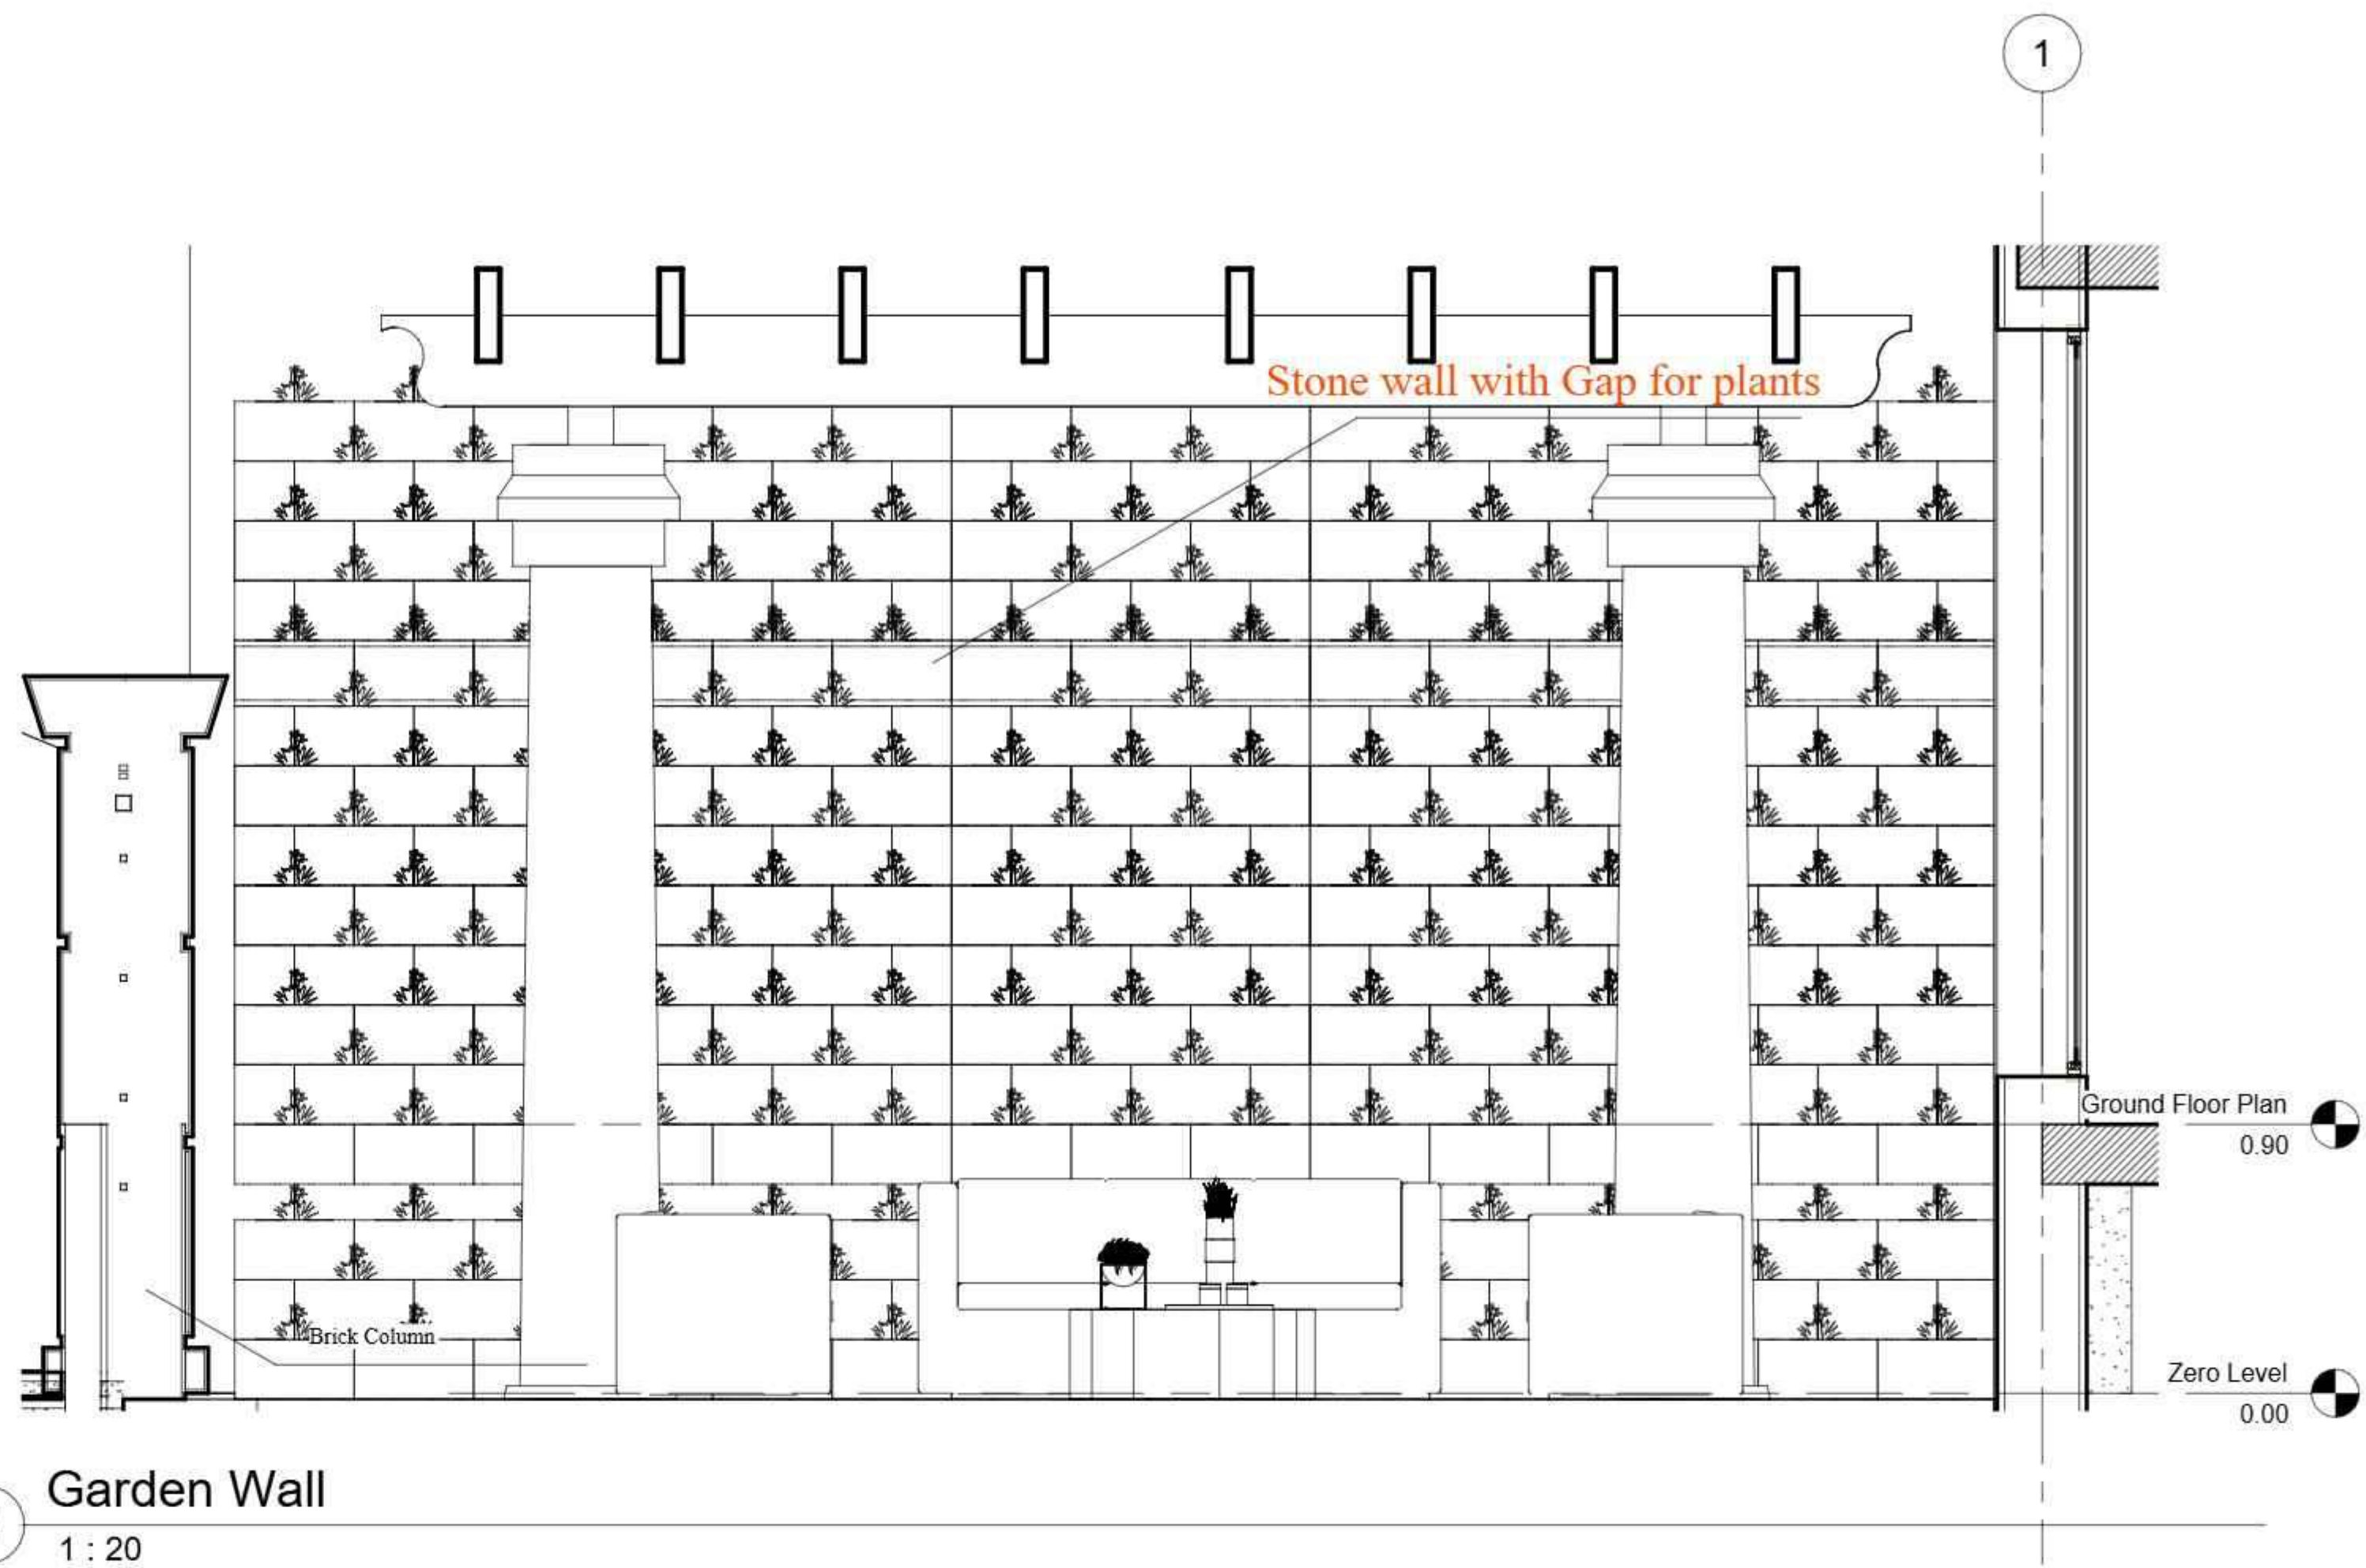

5 Garden Wall
1 : 20

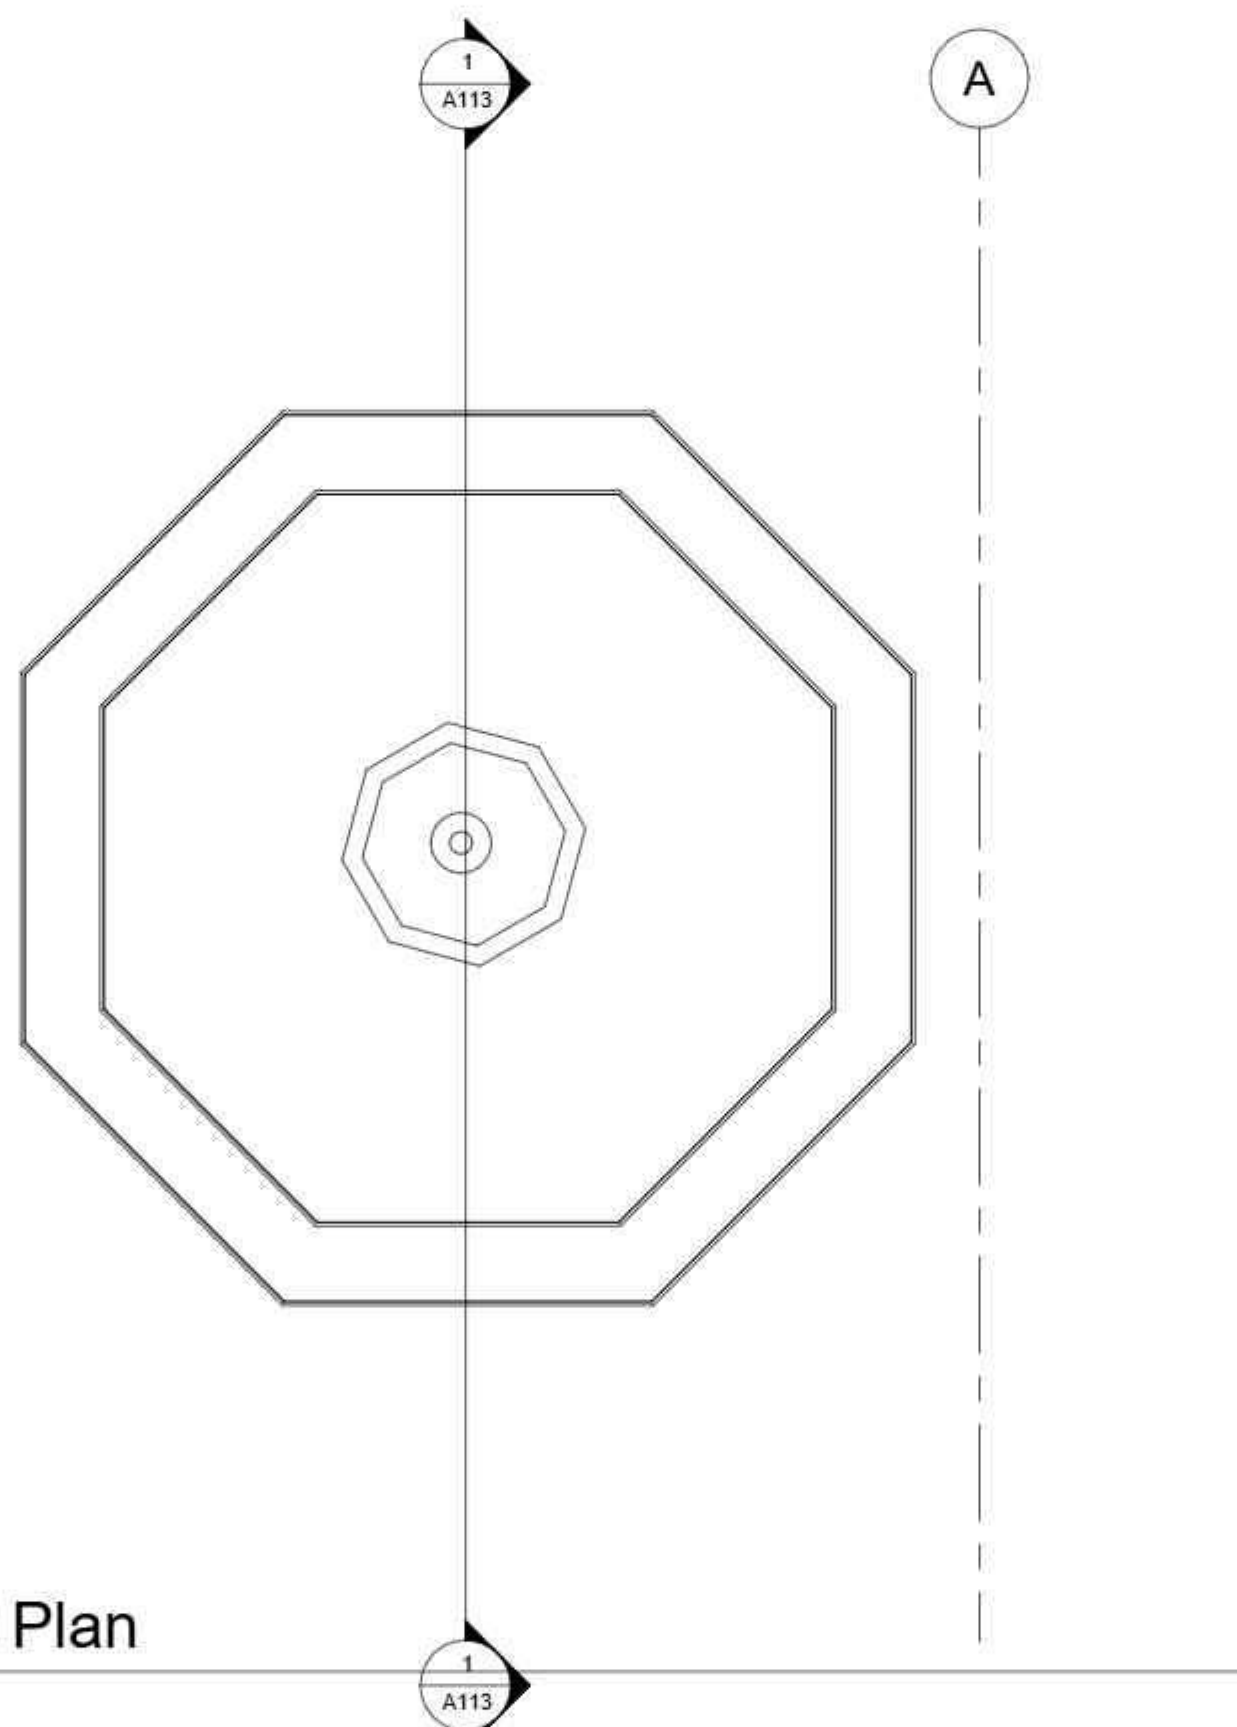


2 Fountain Plan
1 : 20

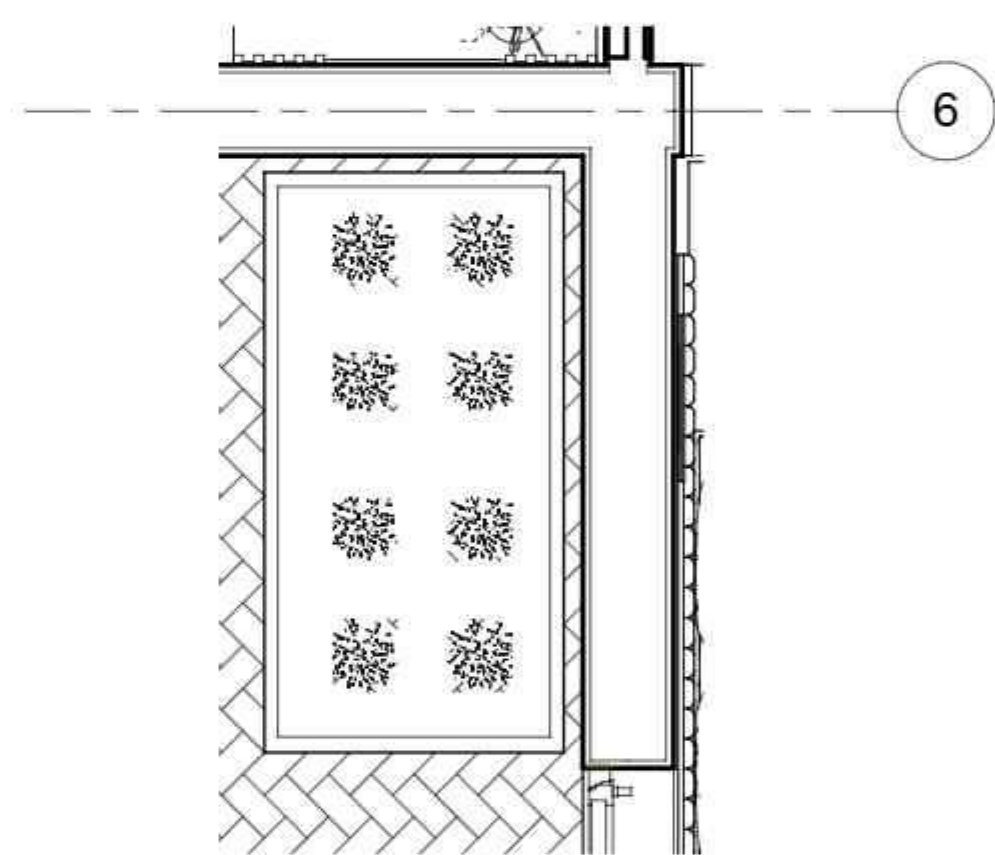


4 Flower Box at Entrance
1 : 25

2cm	Ceramic Tile 20cm x 20cm
2cm	Mortar
1cm	Adhesive Rubber
2cm	Mortar
2mm	Damp Insulation
12cm	Reinforced Concrete
2cm	Ceramic Tile 20cm x 20cm

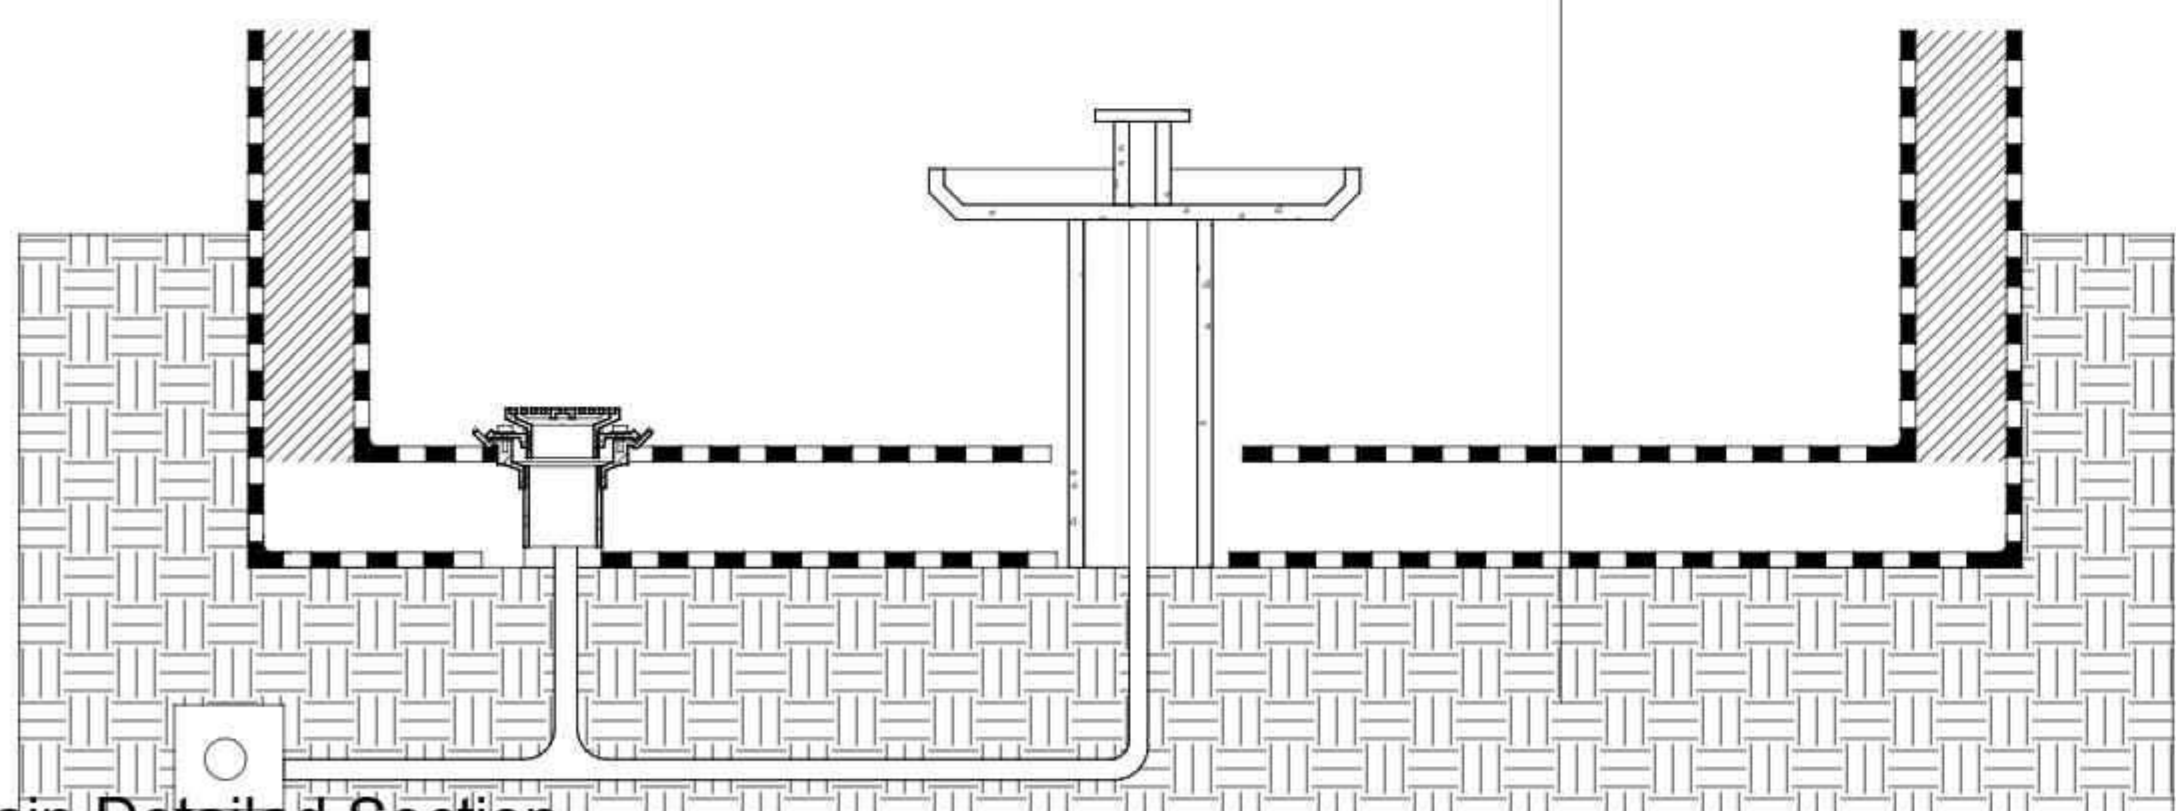




1 Fountain Detailed Section
1 : 10

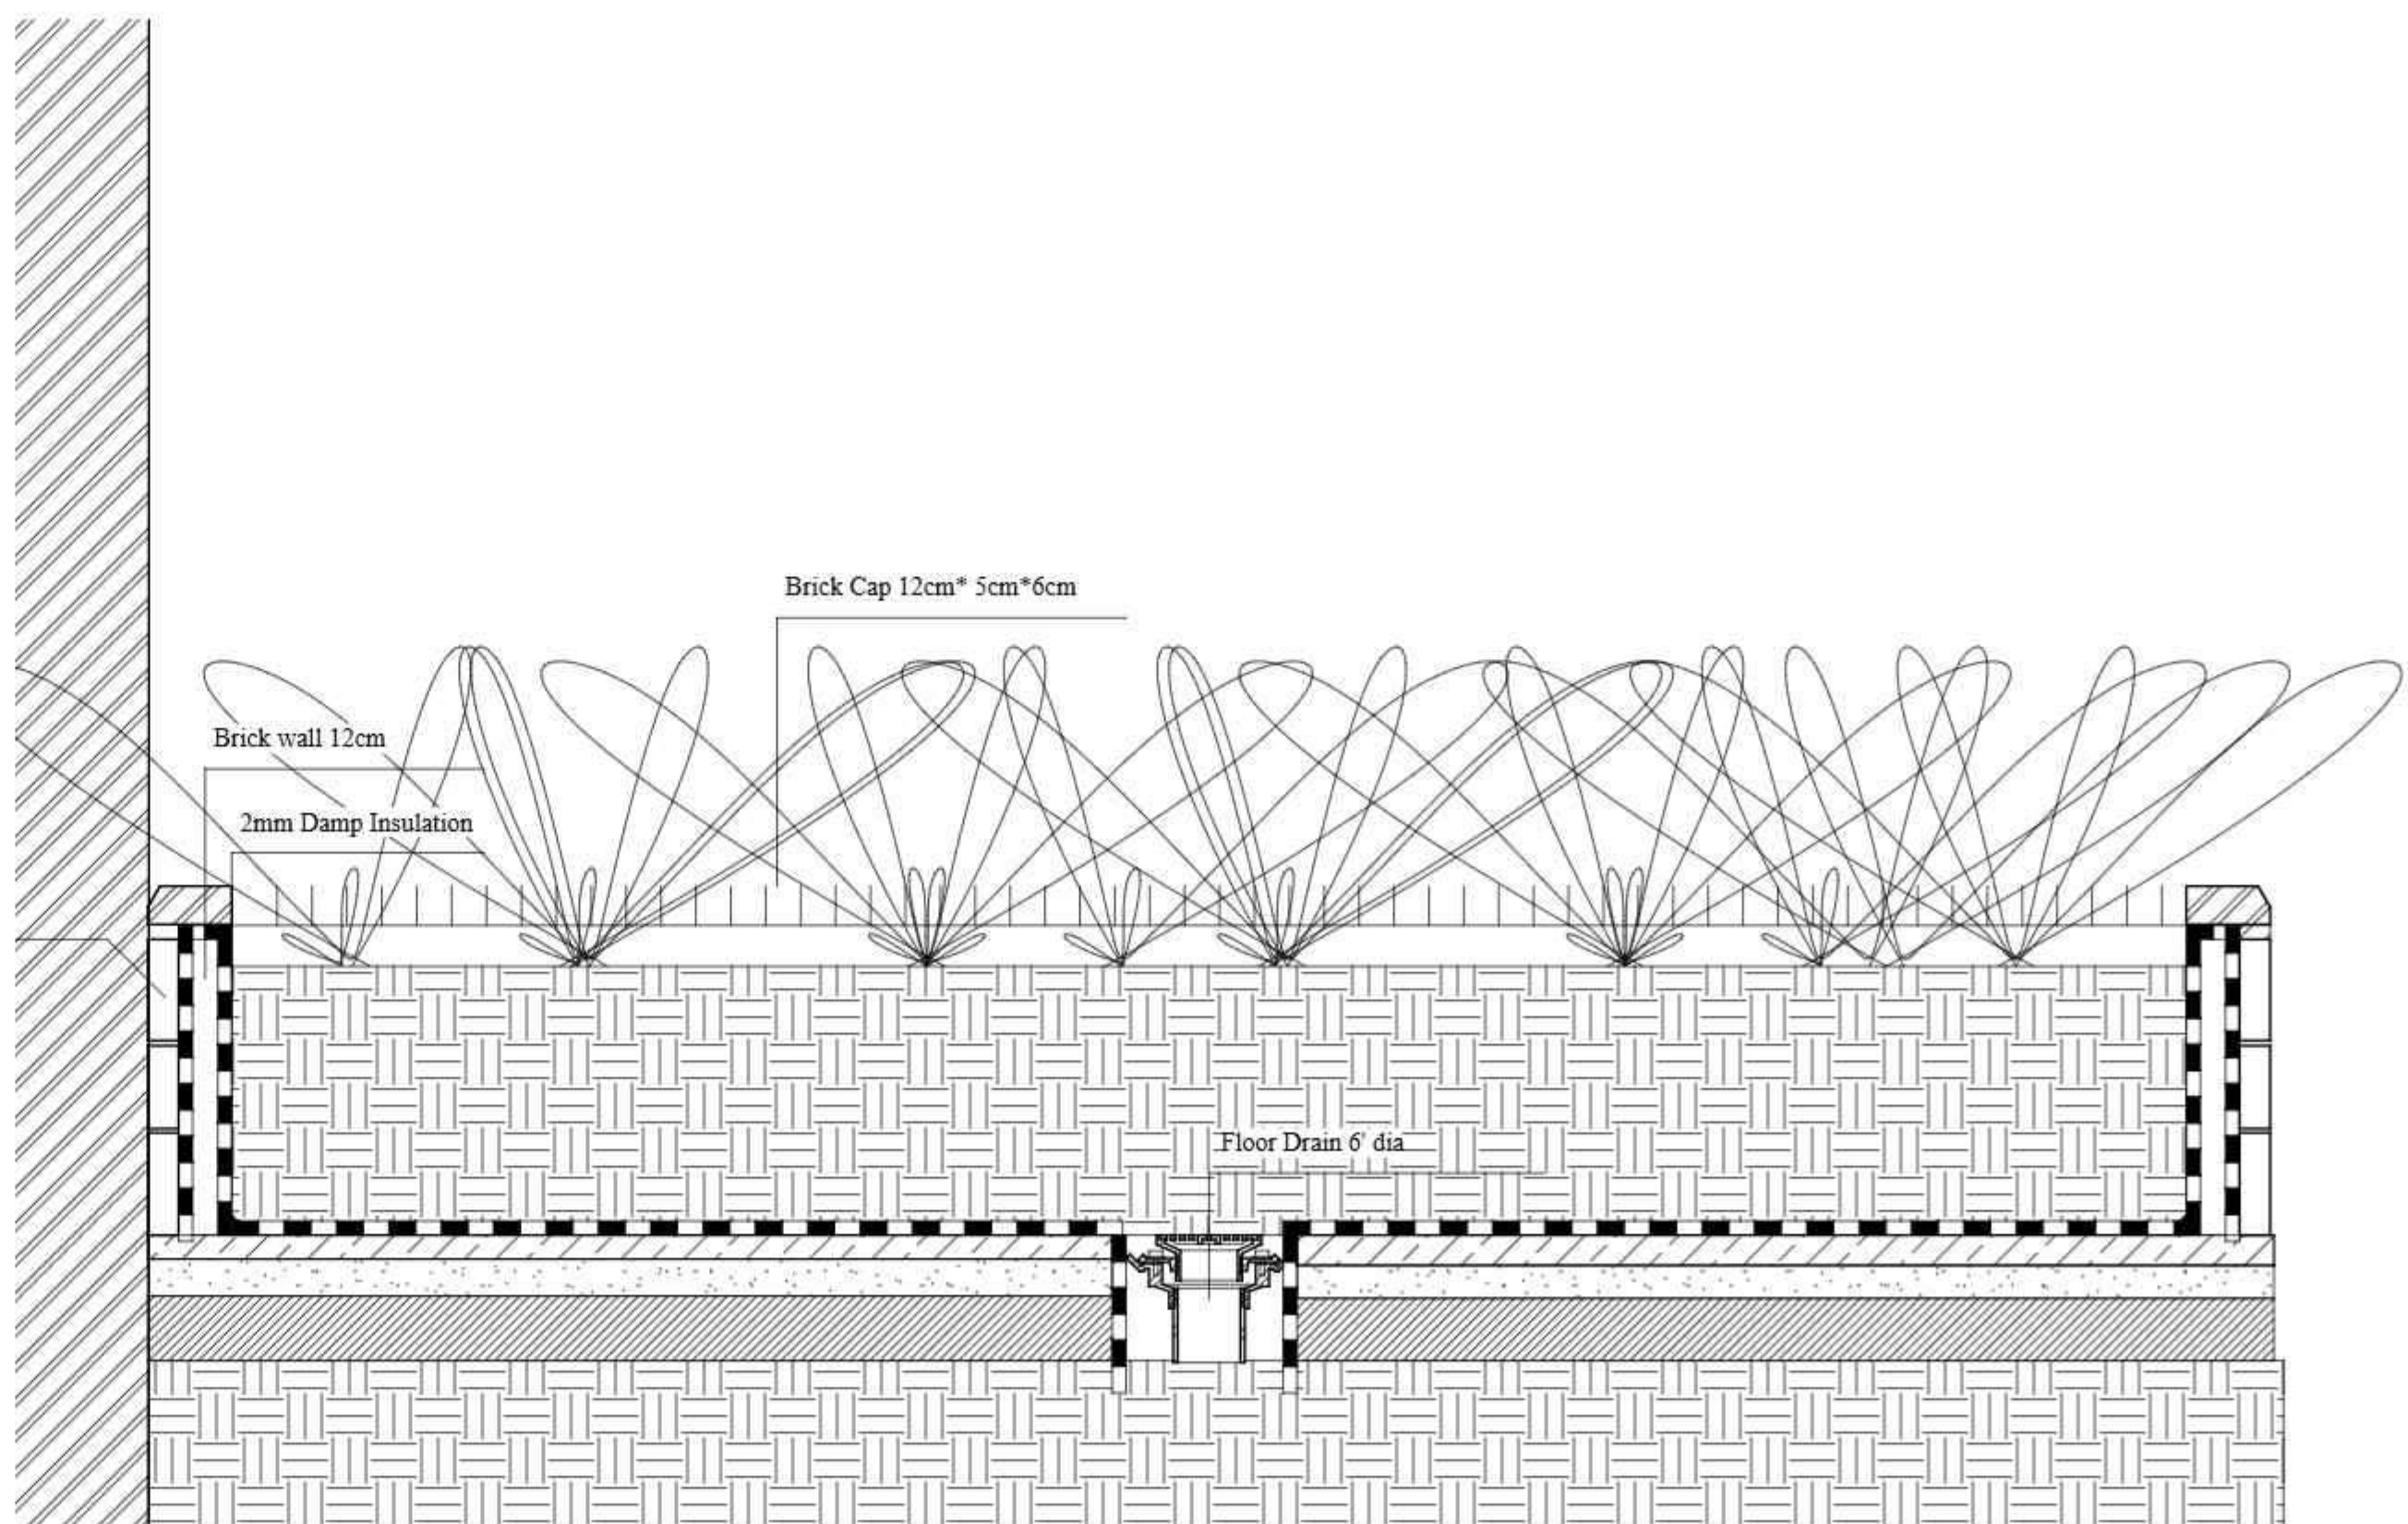



3 Flower Box Details
1 : 10

Course Info:
ASE 464
Working Drawings III

GENERAL NOTES:
- ALL MATERIALS & WORK PRACTICES SHALL COMPLY WITH, BUT NOT LIMITED TO THE BUILDING REGULATION 2019, THE NATIONAL CONSTRUCTION CODE OF EGYPT UNLESS OTHERWISE SPECIFIED.
- ALL DIMENSIONS ARE IN METERS. IF IN DOUBT ASK, DO NOT SCALE.
- THESE DRAWINGS SHALL BE READ IN CONJUNCTION WITH ALL RELEVANT STRUCTURAL + ALL OTHER CONSULTANTS DRAWINGS/DETAILS & WITH ANY OTHER WRITTEN INSTRUCTIONS ISSUED IN THE COURSE OF THE CONTRACT.
- THESE DRAWINGS SHALL BE READ IN CONJUNCTION WITH ANY ENERGY RATING REPORT + SHALL BE CONSTRUCTED IN ACCORDANCE WITH THE STAMPED PLANS ENDORSED BY THE ACCREDITED THERMAL PERFORMANCE ASSESSOR WITHOUT ALTERATION

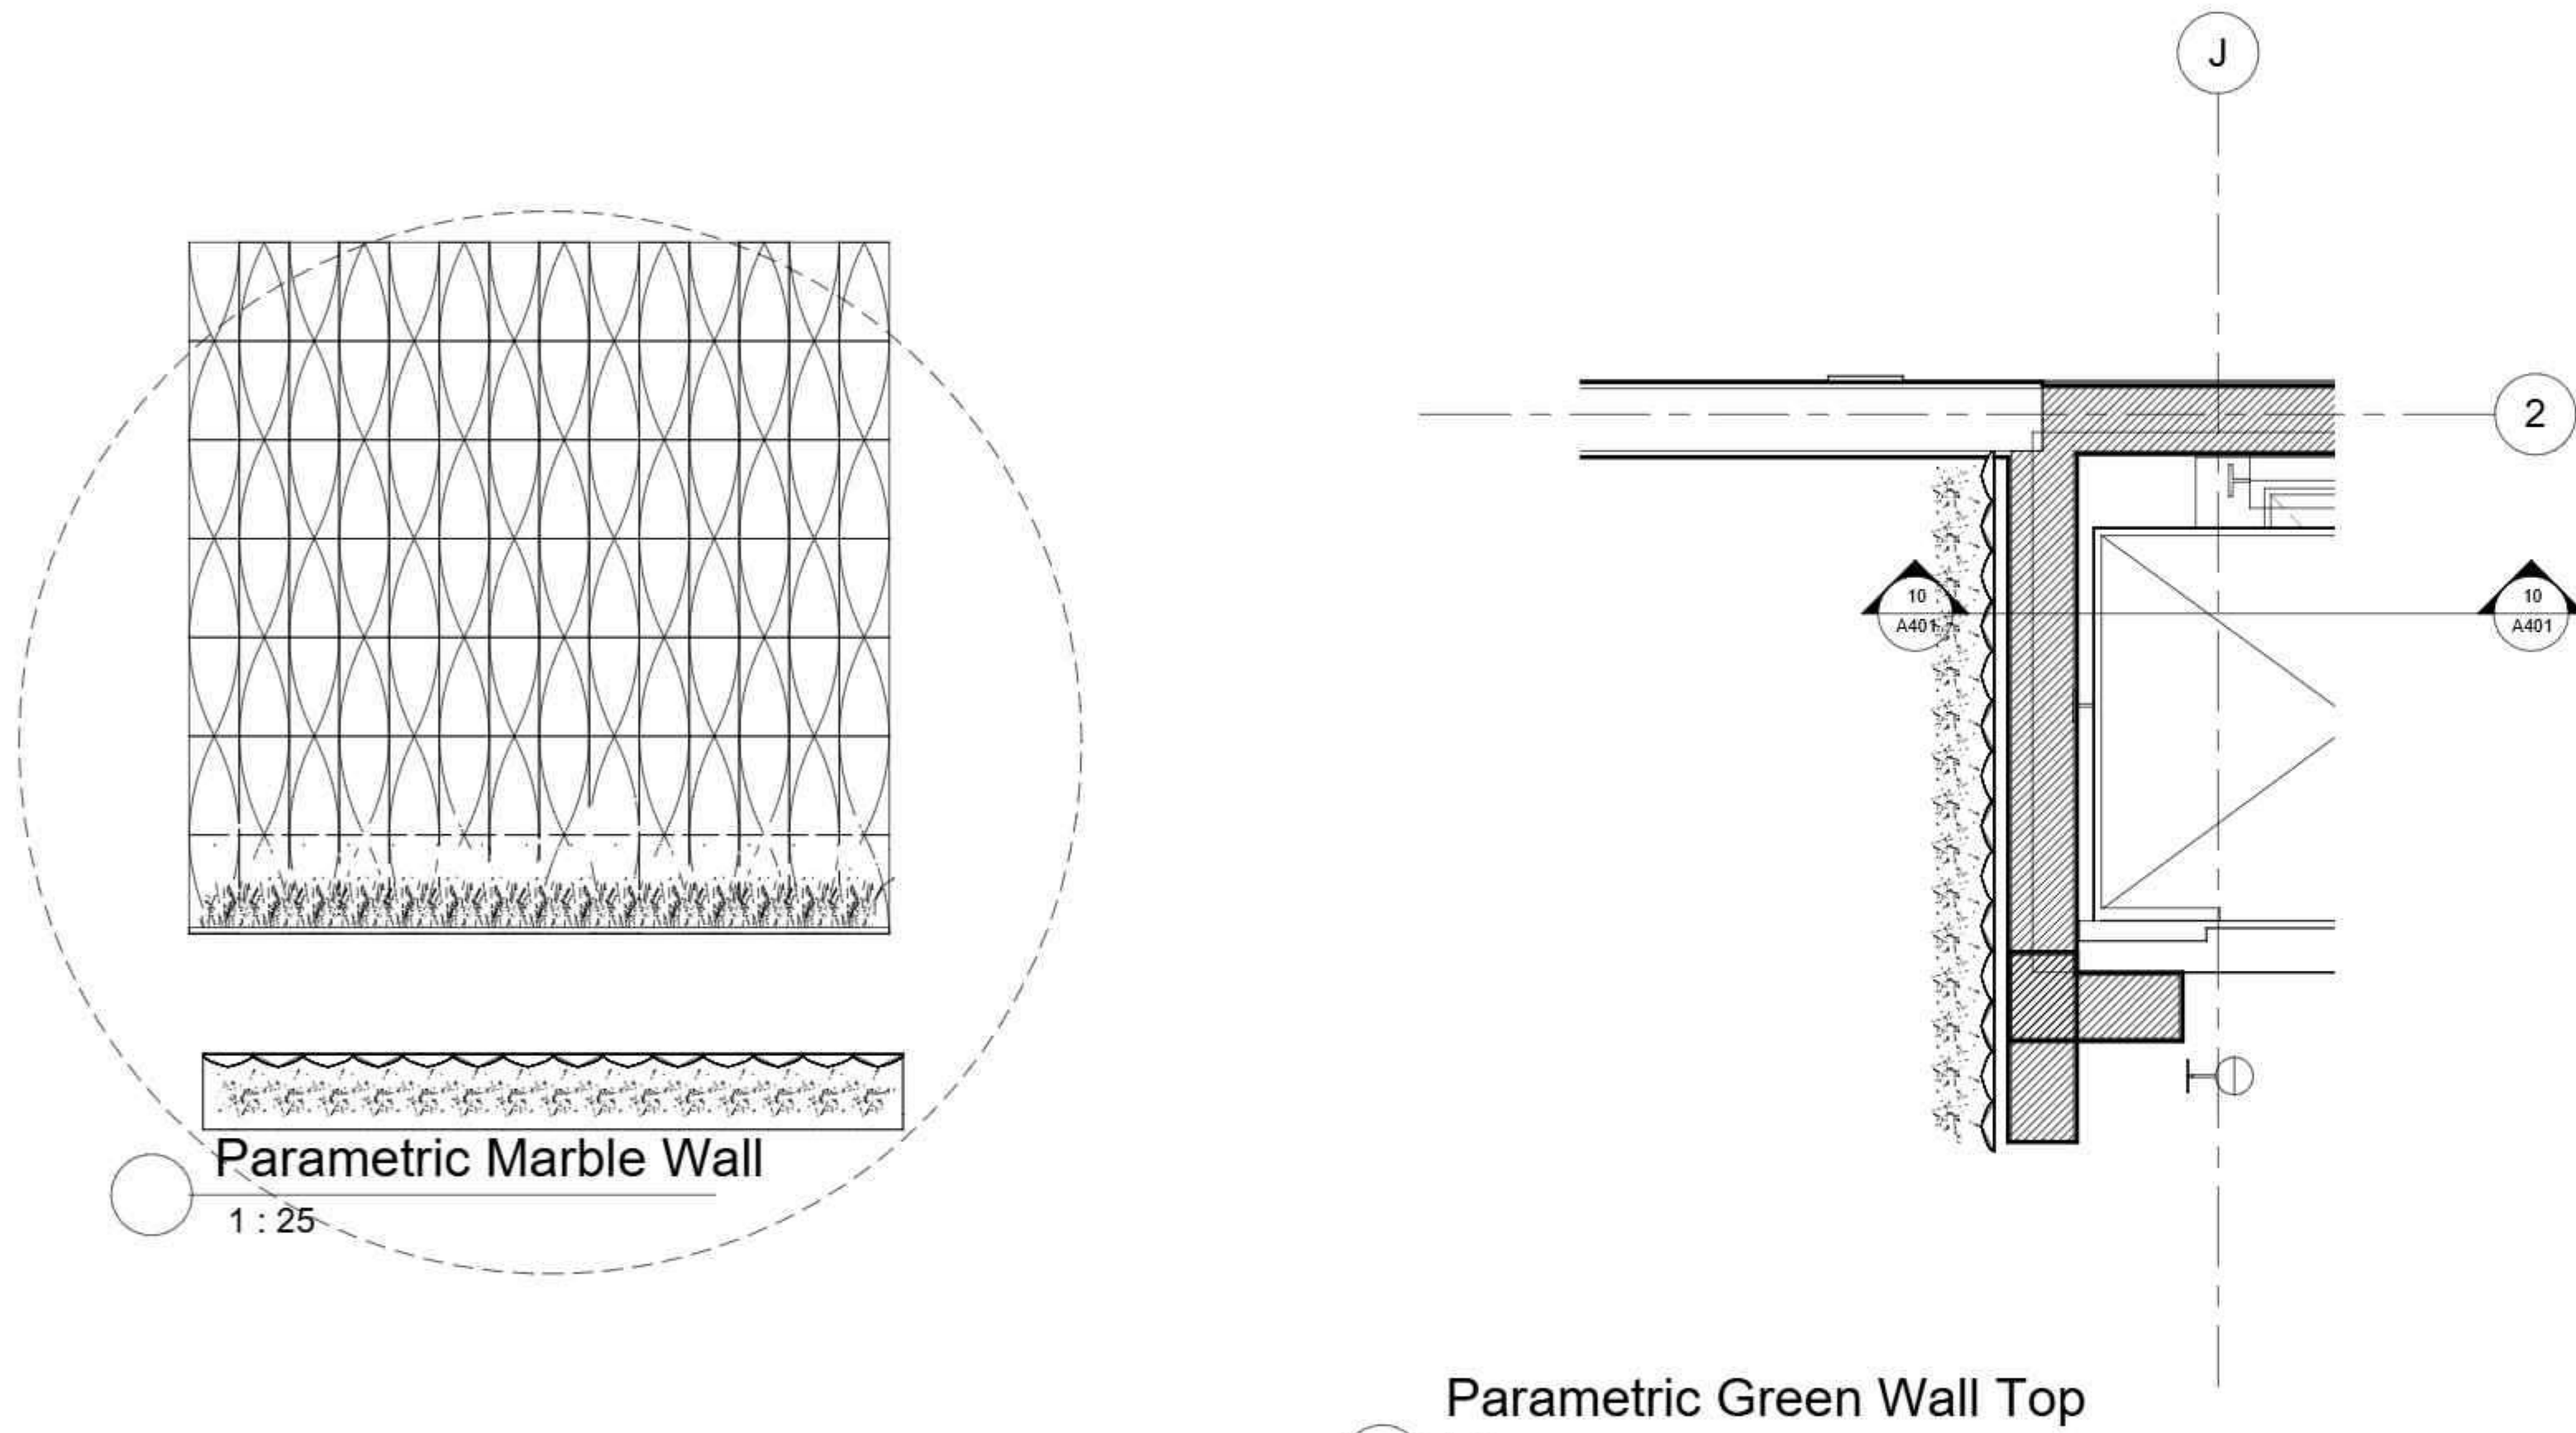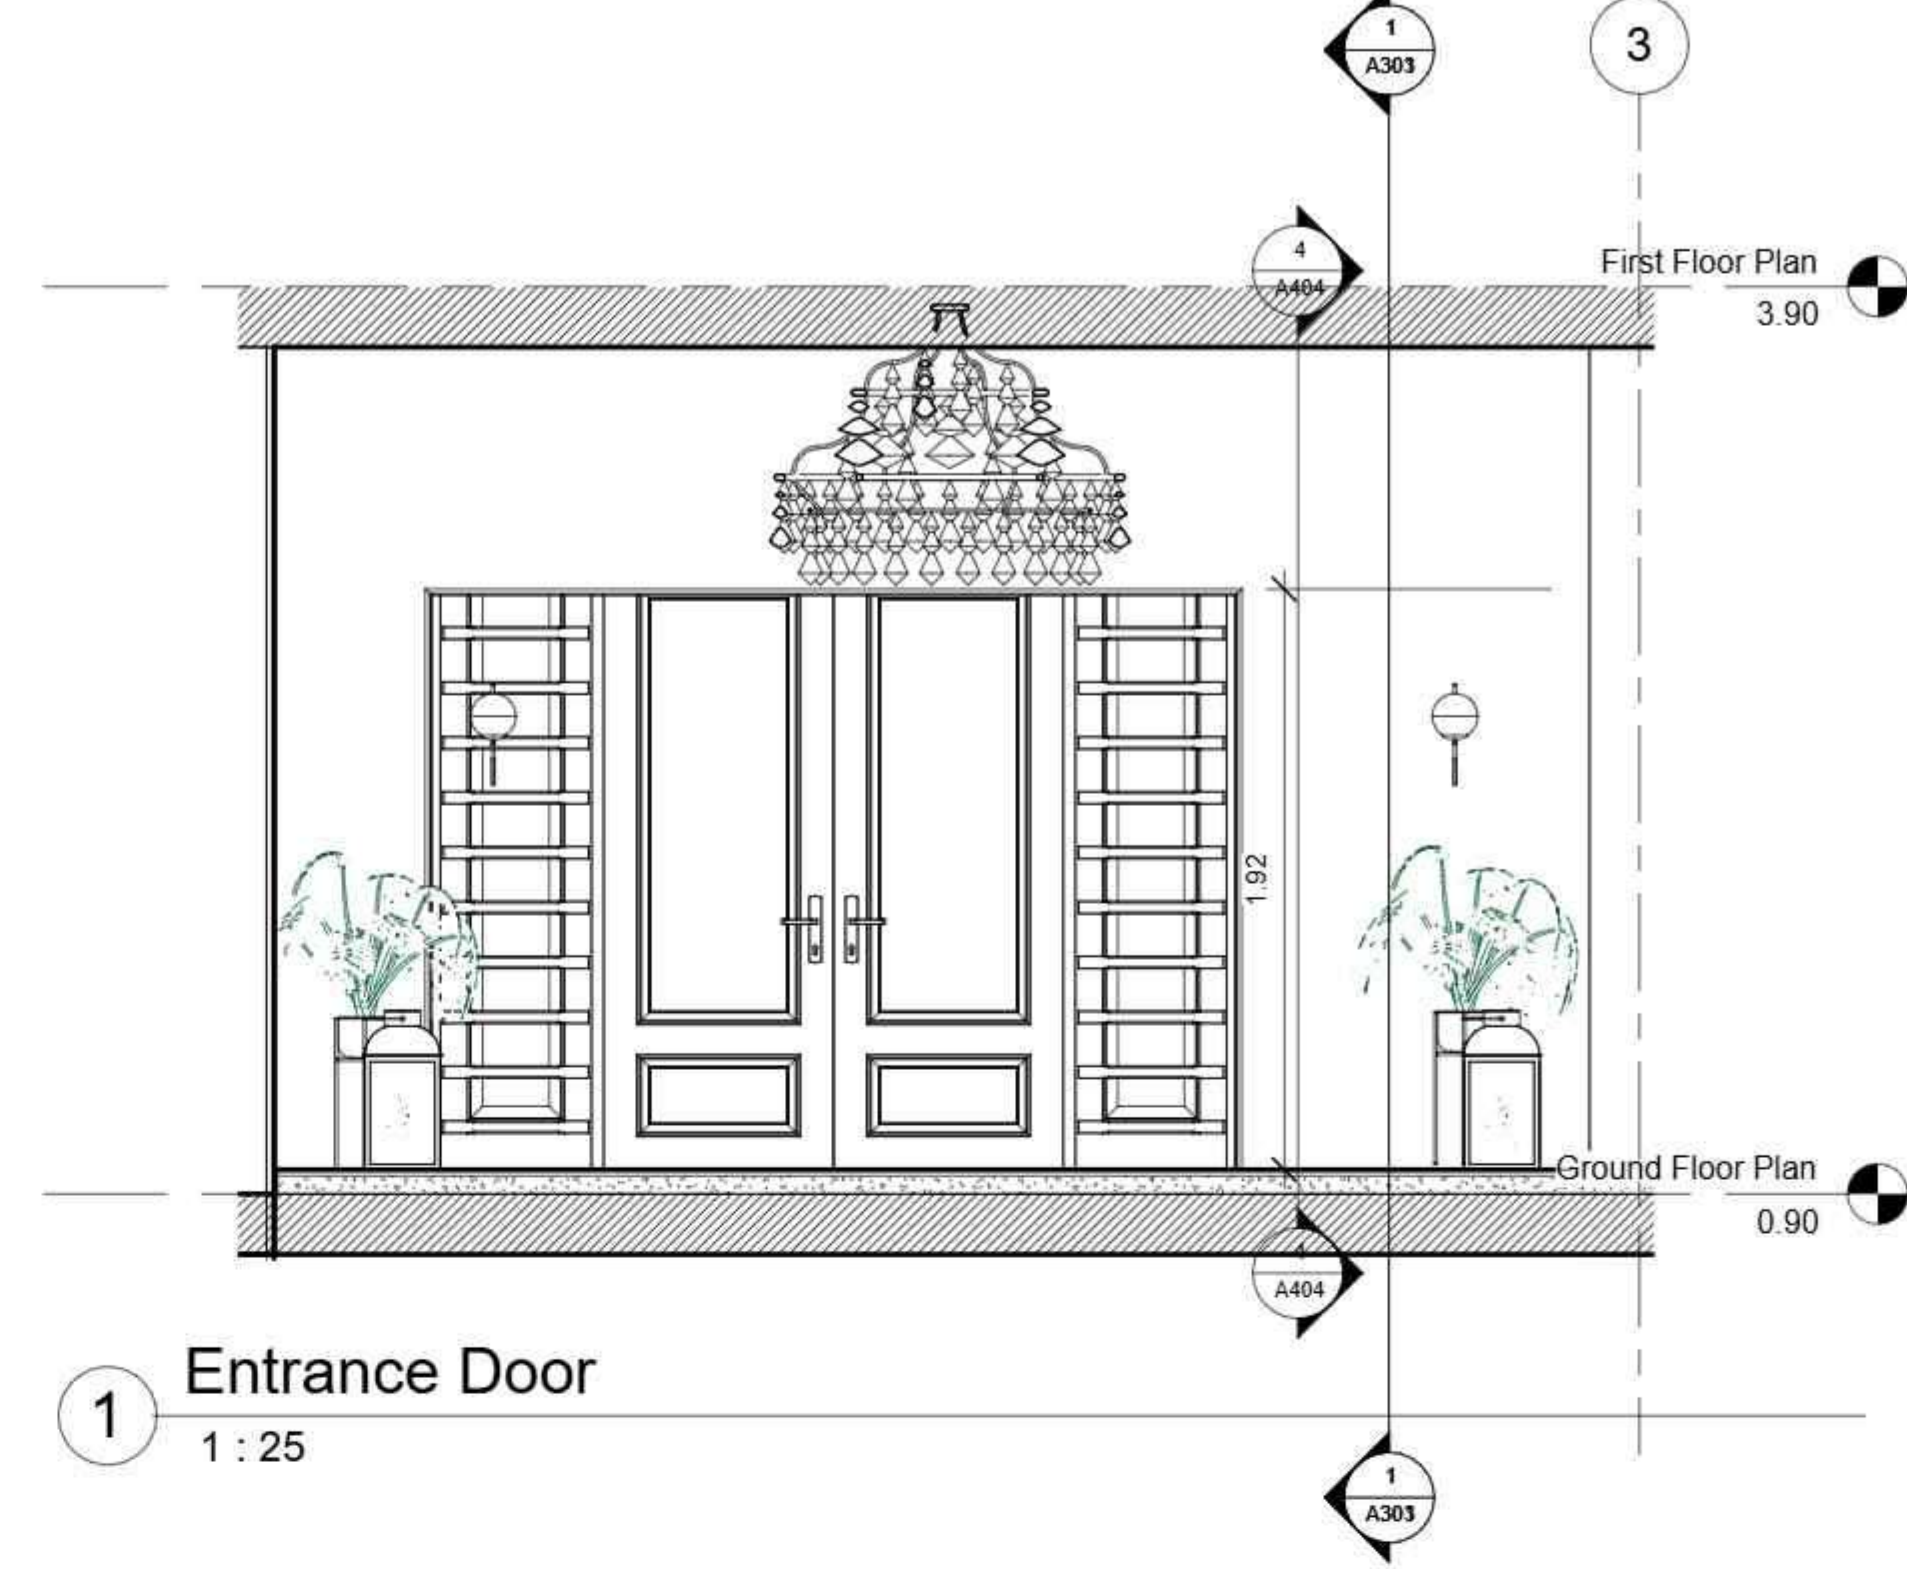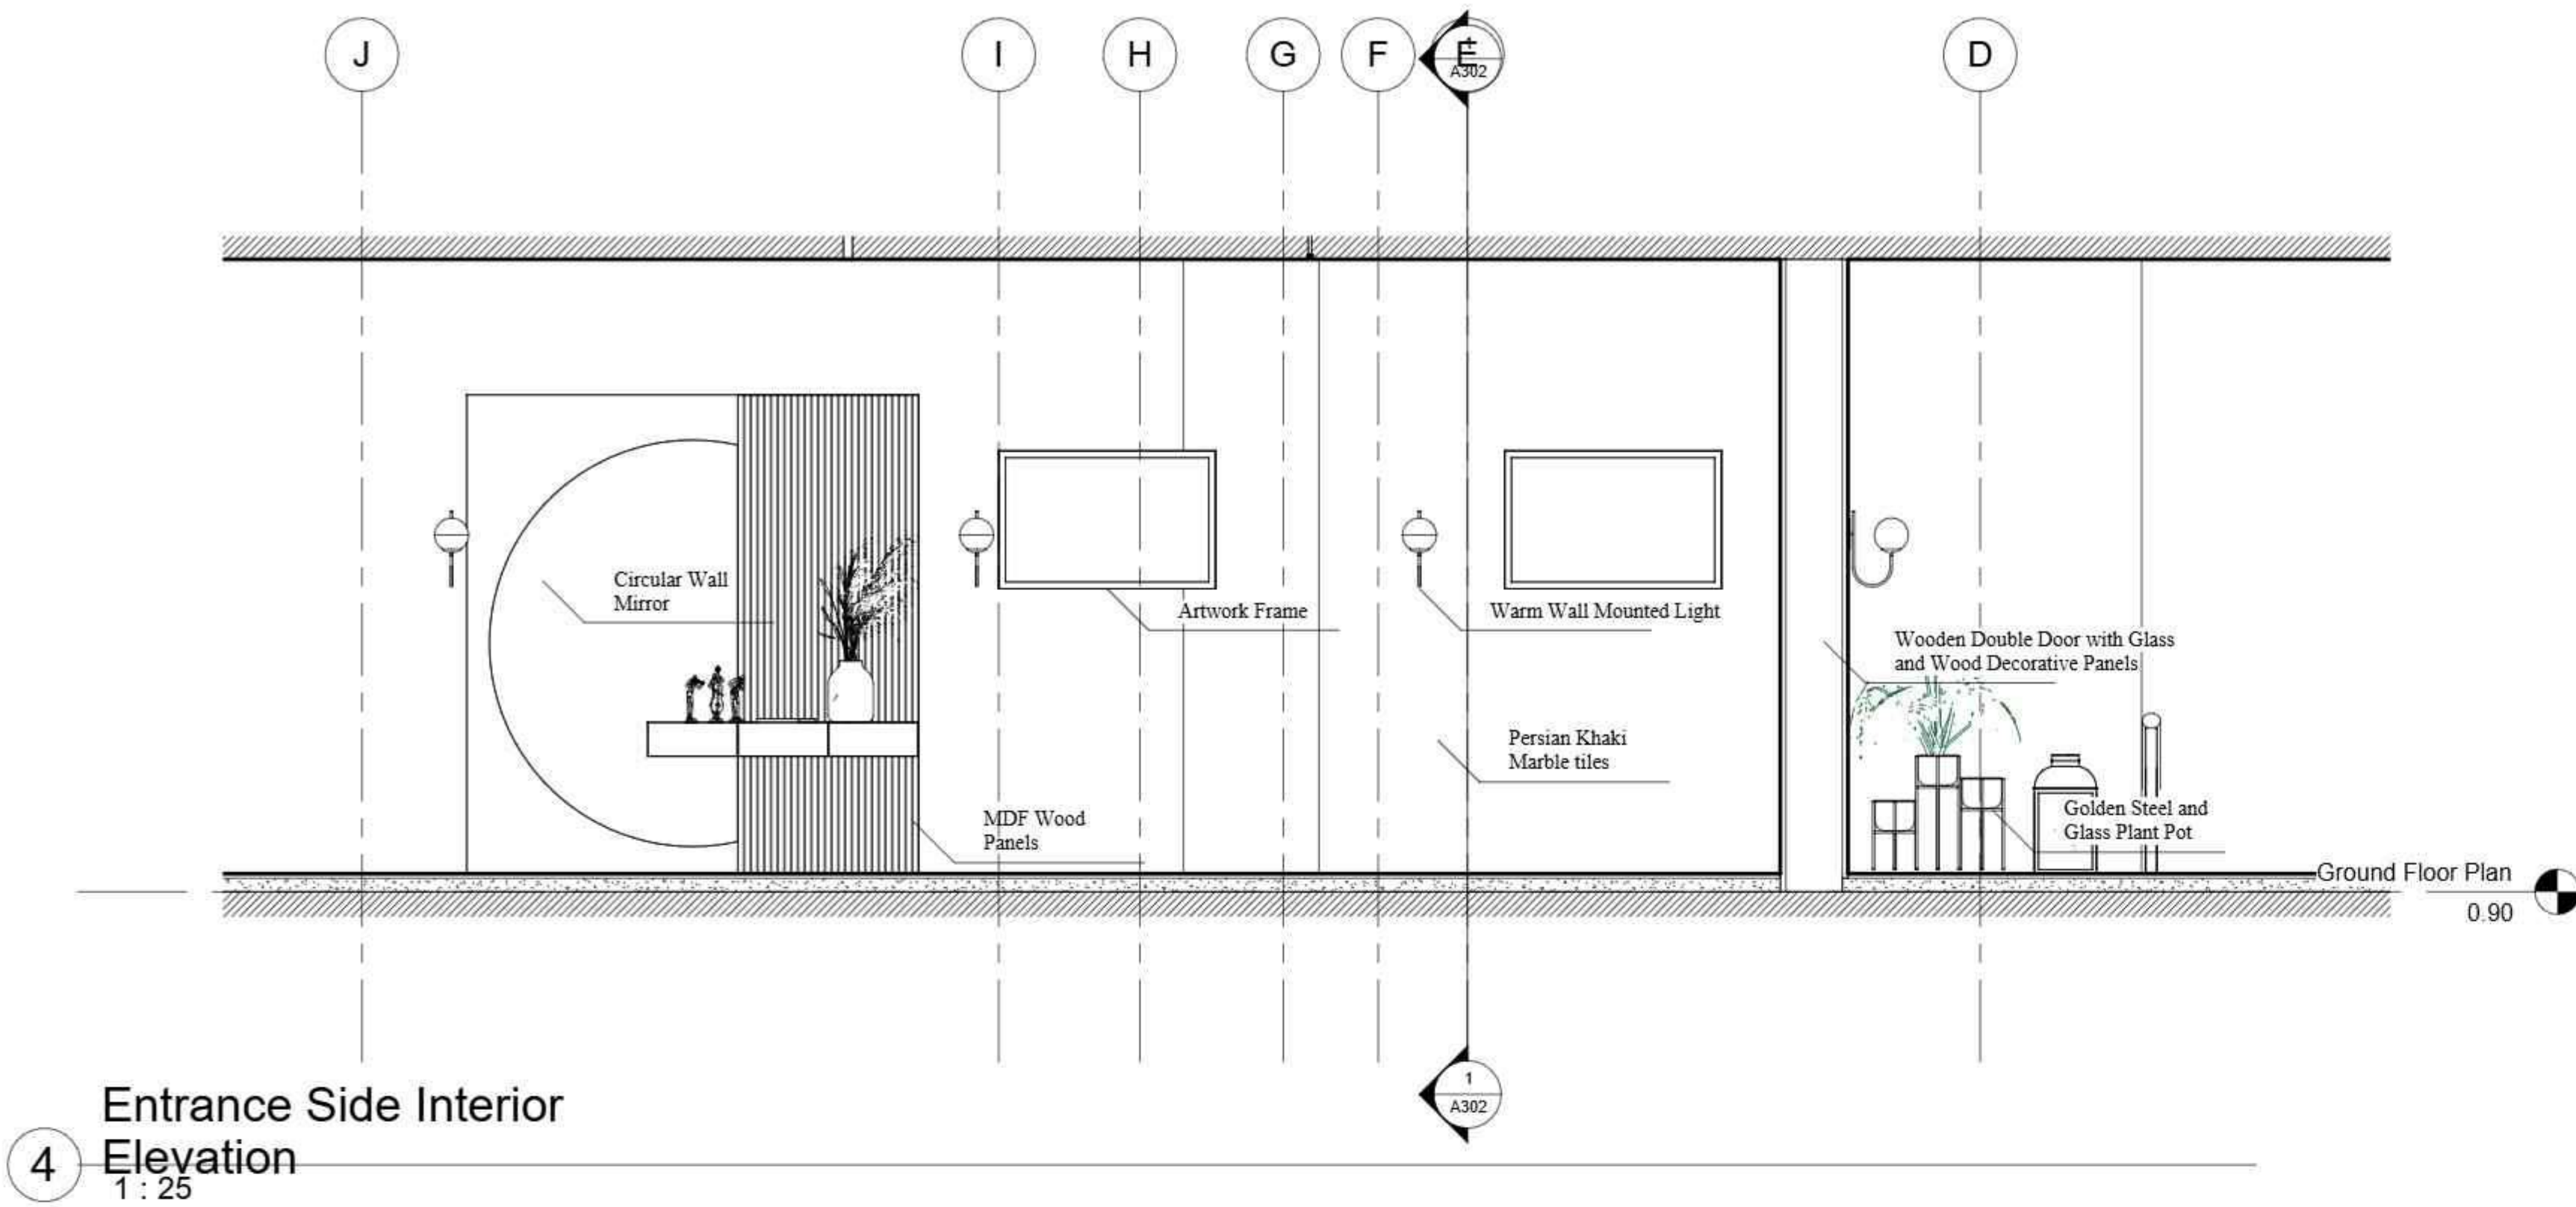

Note: This Parametric Wall Design is located at the side of the elevator wall, and it will be seen the moment someone entrance the building

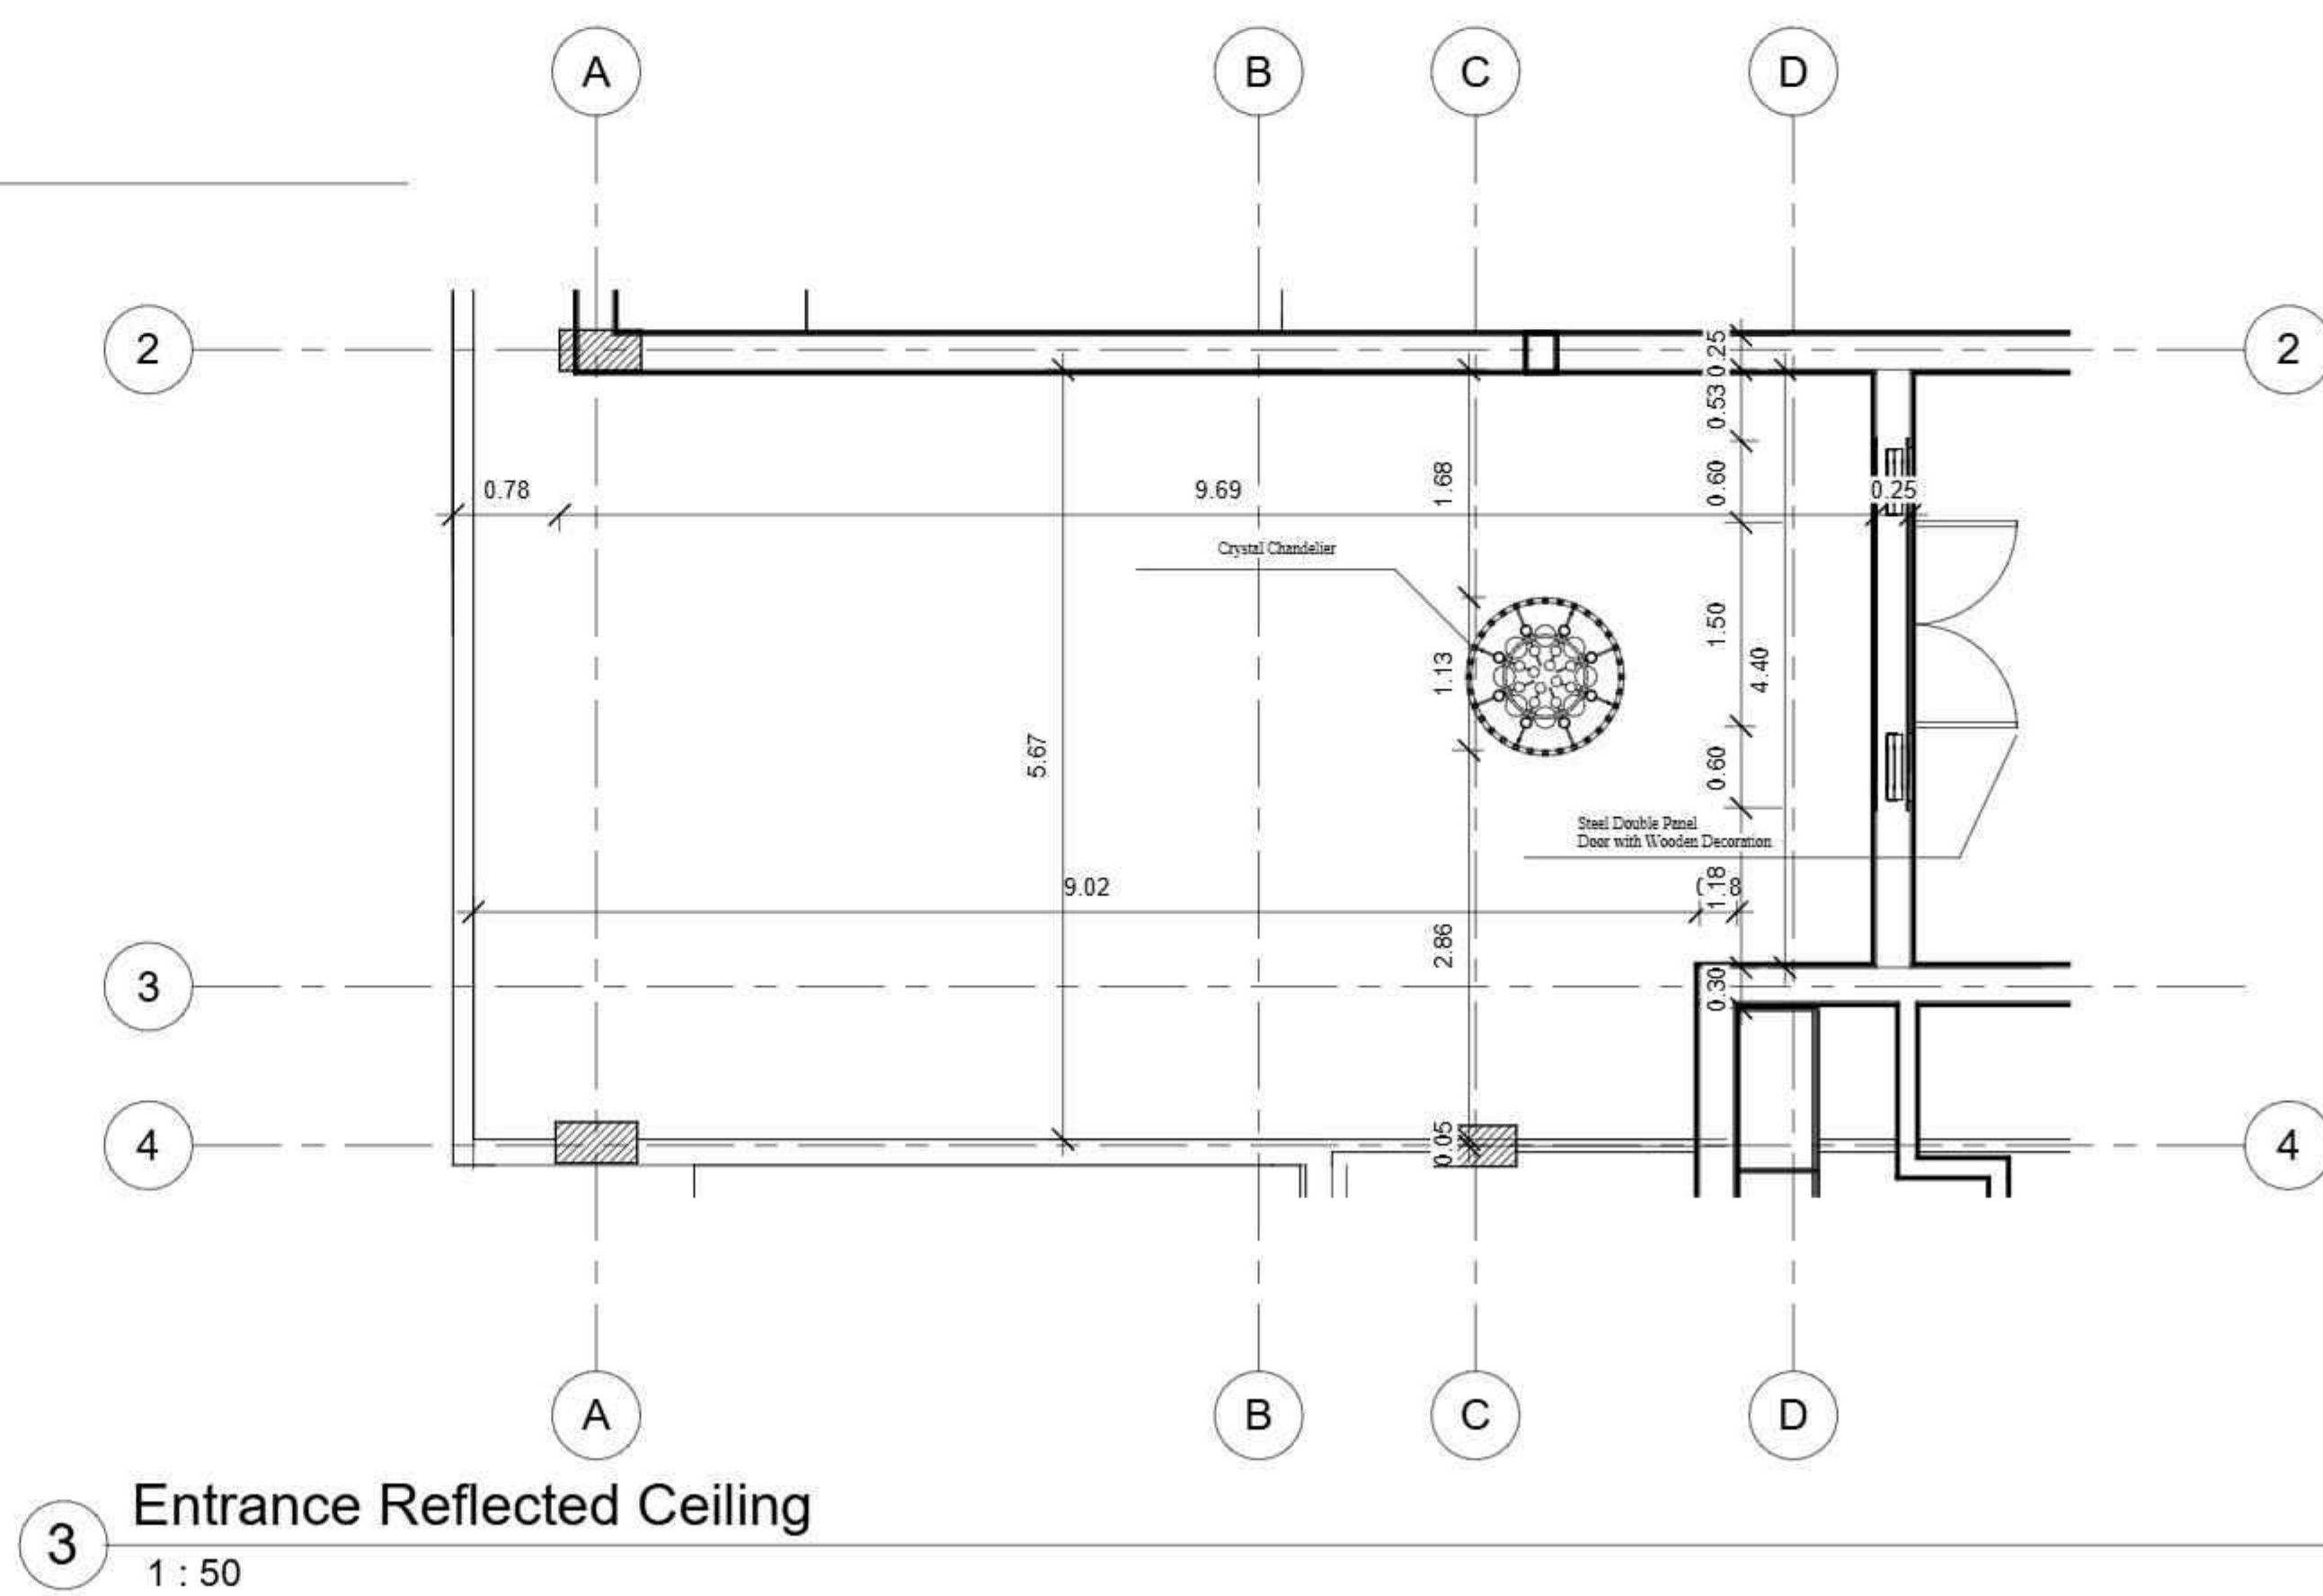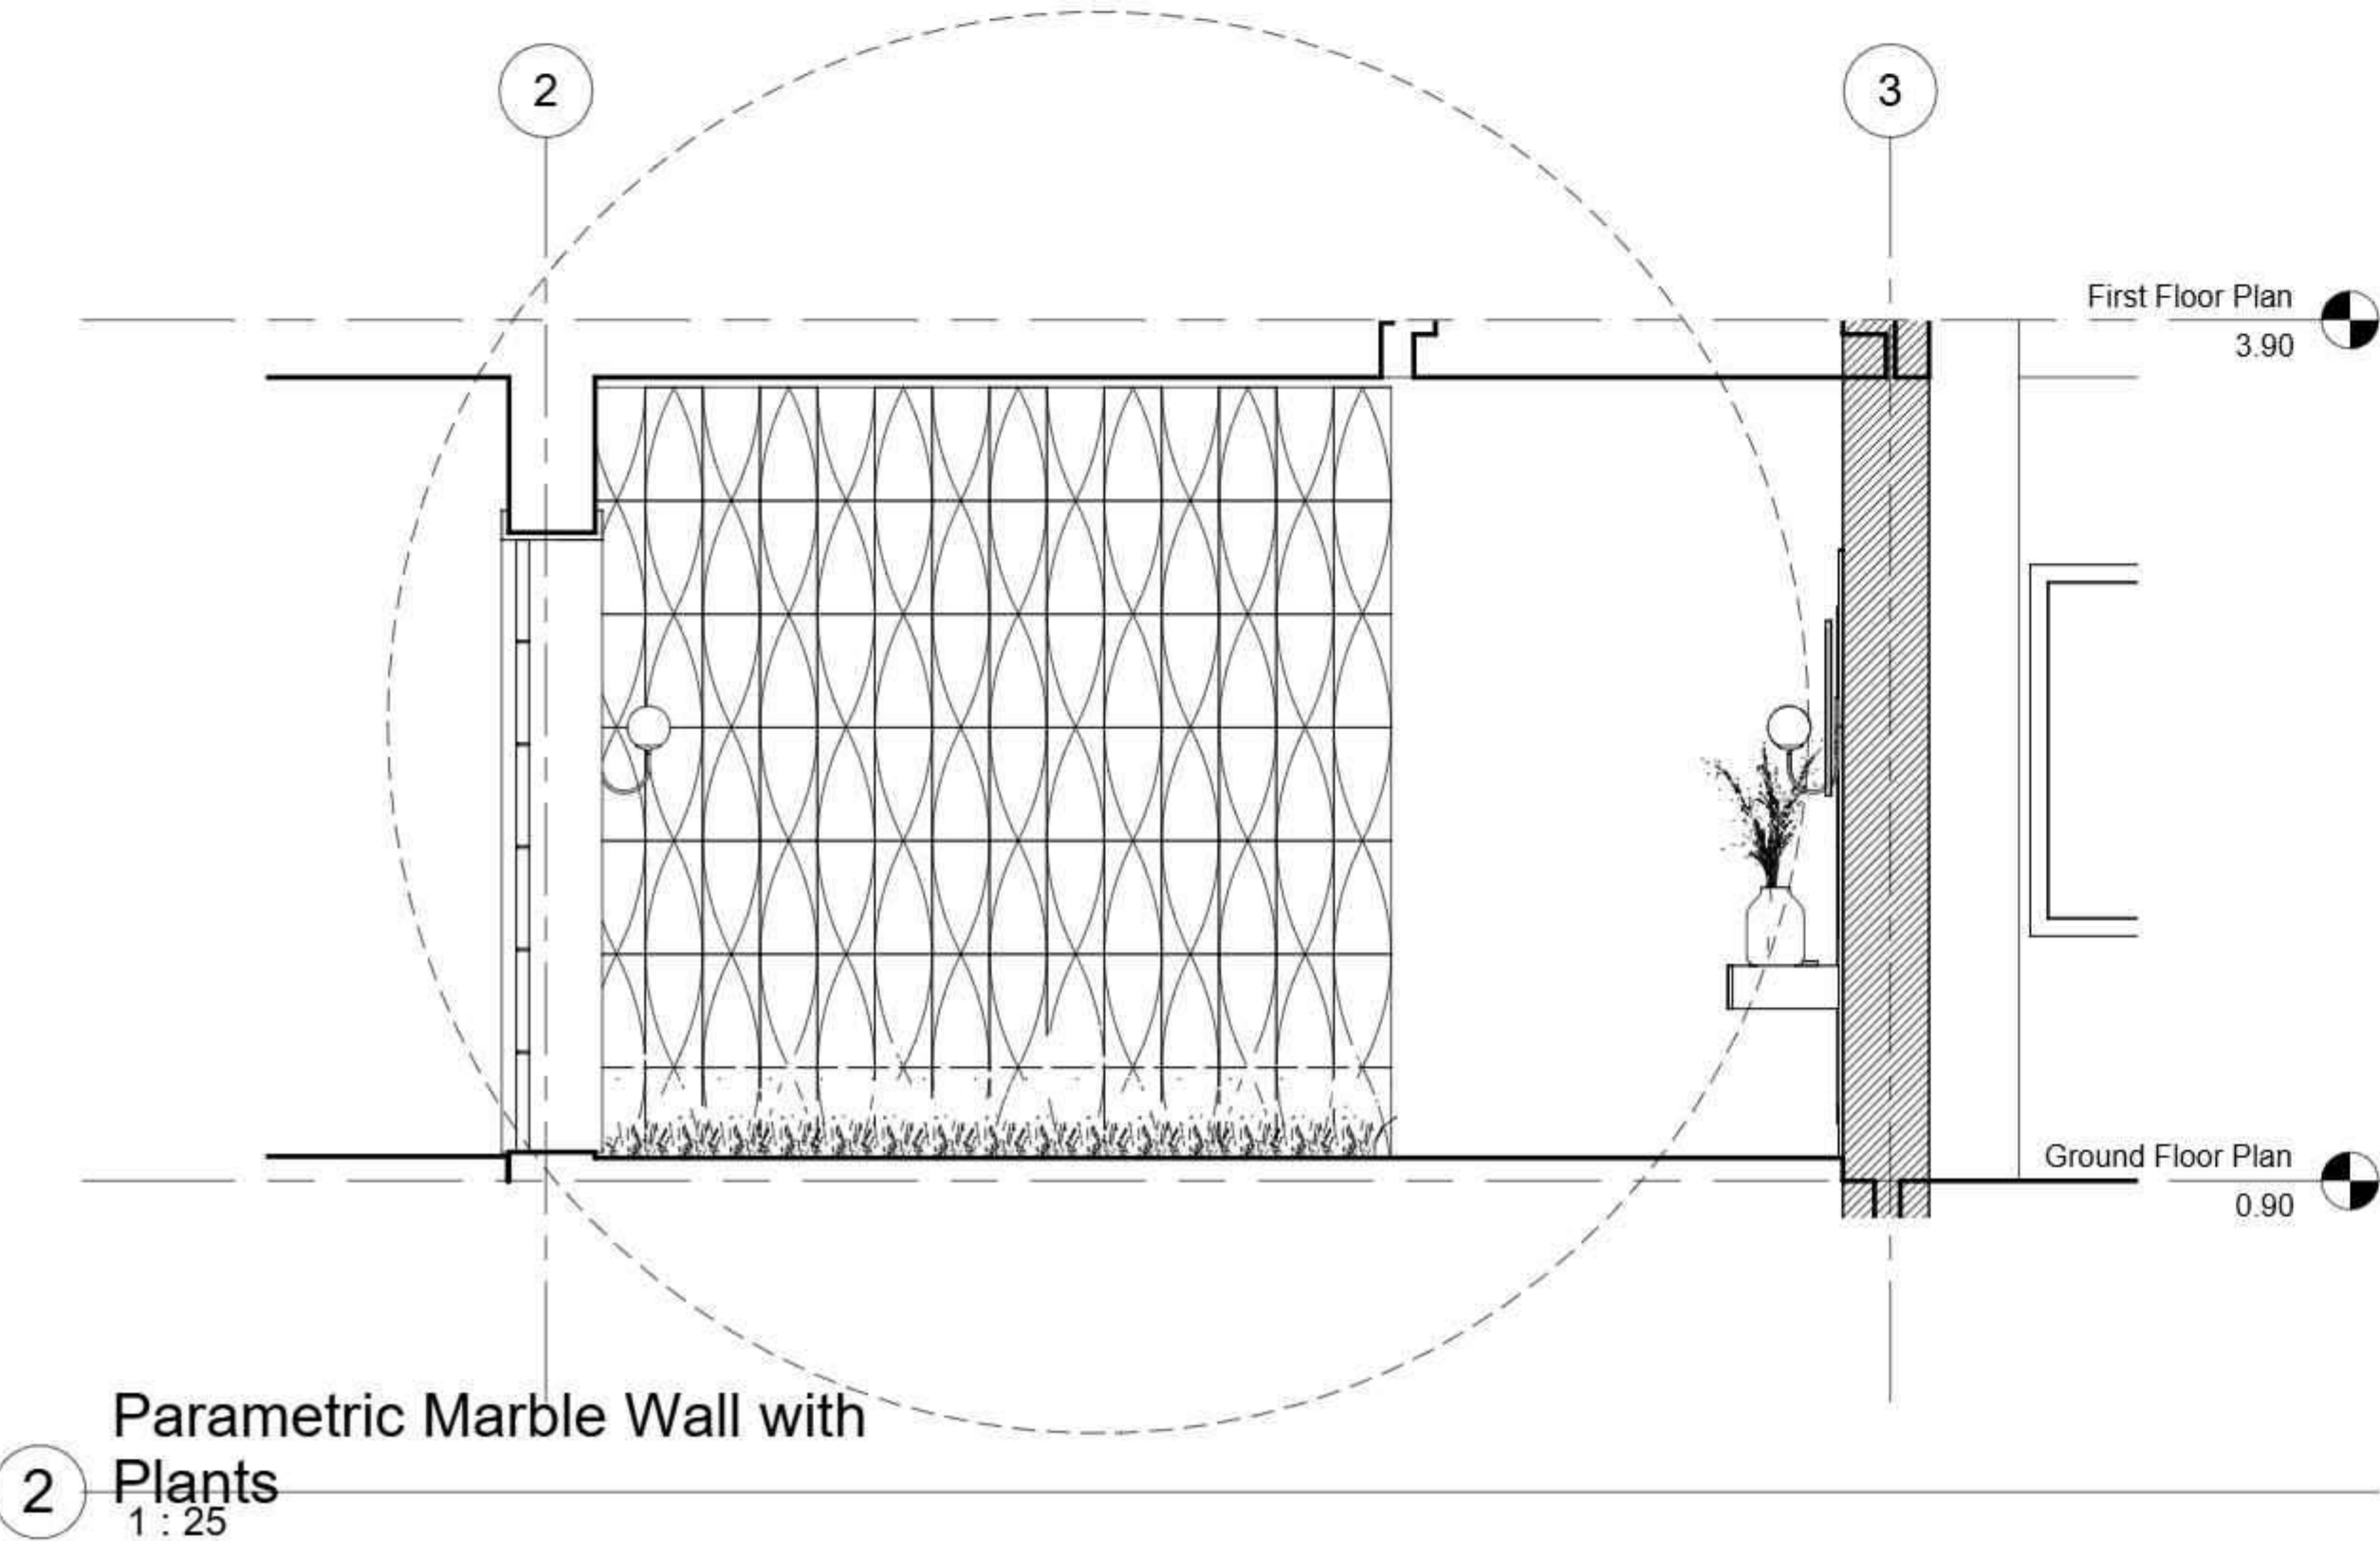

OWNER:

MSA UNIVERSITY
جامعة أكتوبر للعلوم الحديثة والآداب
UNIVERSITY of
GREENWICH
OCTOBER UNIVERSITY
FOR MODERN SCIENCES & ARTS
Architectural Engineering Department
Spring 2025

CLIENTS NAME:
Dr. Tarek Galal
Eng. Hend
Eng. Nermeen
Eng. Yousra

Student Name: Hadeel Zakaria
ID: 220009

PROJECT NAME:
APARTMENT BUILDING

SHEET NAME:

DETAILS

SHEET NO:
A405

SCALE:
1:-

DATE: 13-5-2025




GENERAL NOTES:

- ALL MATERIALS & WORK PRACTICES SHALL COMPLY WITH, BUT NOT LIMITED TO THE BUILDING REGULATION 2019, THE NATIONAL CONSTRUCTION CODE OF EGYPT UNLESS OTHERWISE SPECIFIED.

- ALL DIMENSIONS ARE IN METERS. IF IN DOUBT ASK, DO NOT SCALE.

- THESE DRAWINGS SHALL BE READ IN CONJUNCTION WITH ALL RELEVANT STRUCTURAL + ALL OTHER CONSULTANTS DRAWINGS/DETAILS & WITH ANY OTHER WRITTEN INSTRUCTIONS ISSUED IN THE COURSE OF THE CONTRACT.

- THESE DRAWINGS SHALL BE READ IN CONJUNCTION WITH ANY ENERGY RATING REPORT + SHALL BE CONSTRUCTED IN ACCORDANCE WITH THE STAMPED PLANS ENDORSED BY THE ACCREDITED THERMAL PERFORMANCE ASSESSOR WITHOUT ALTERATION

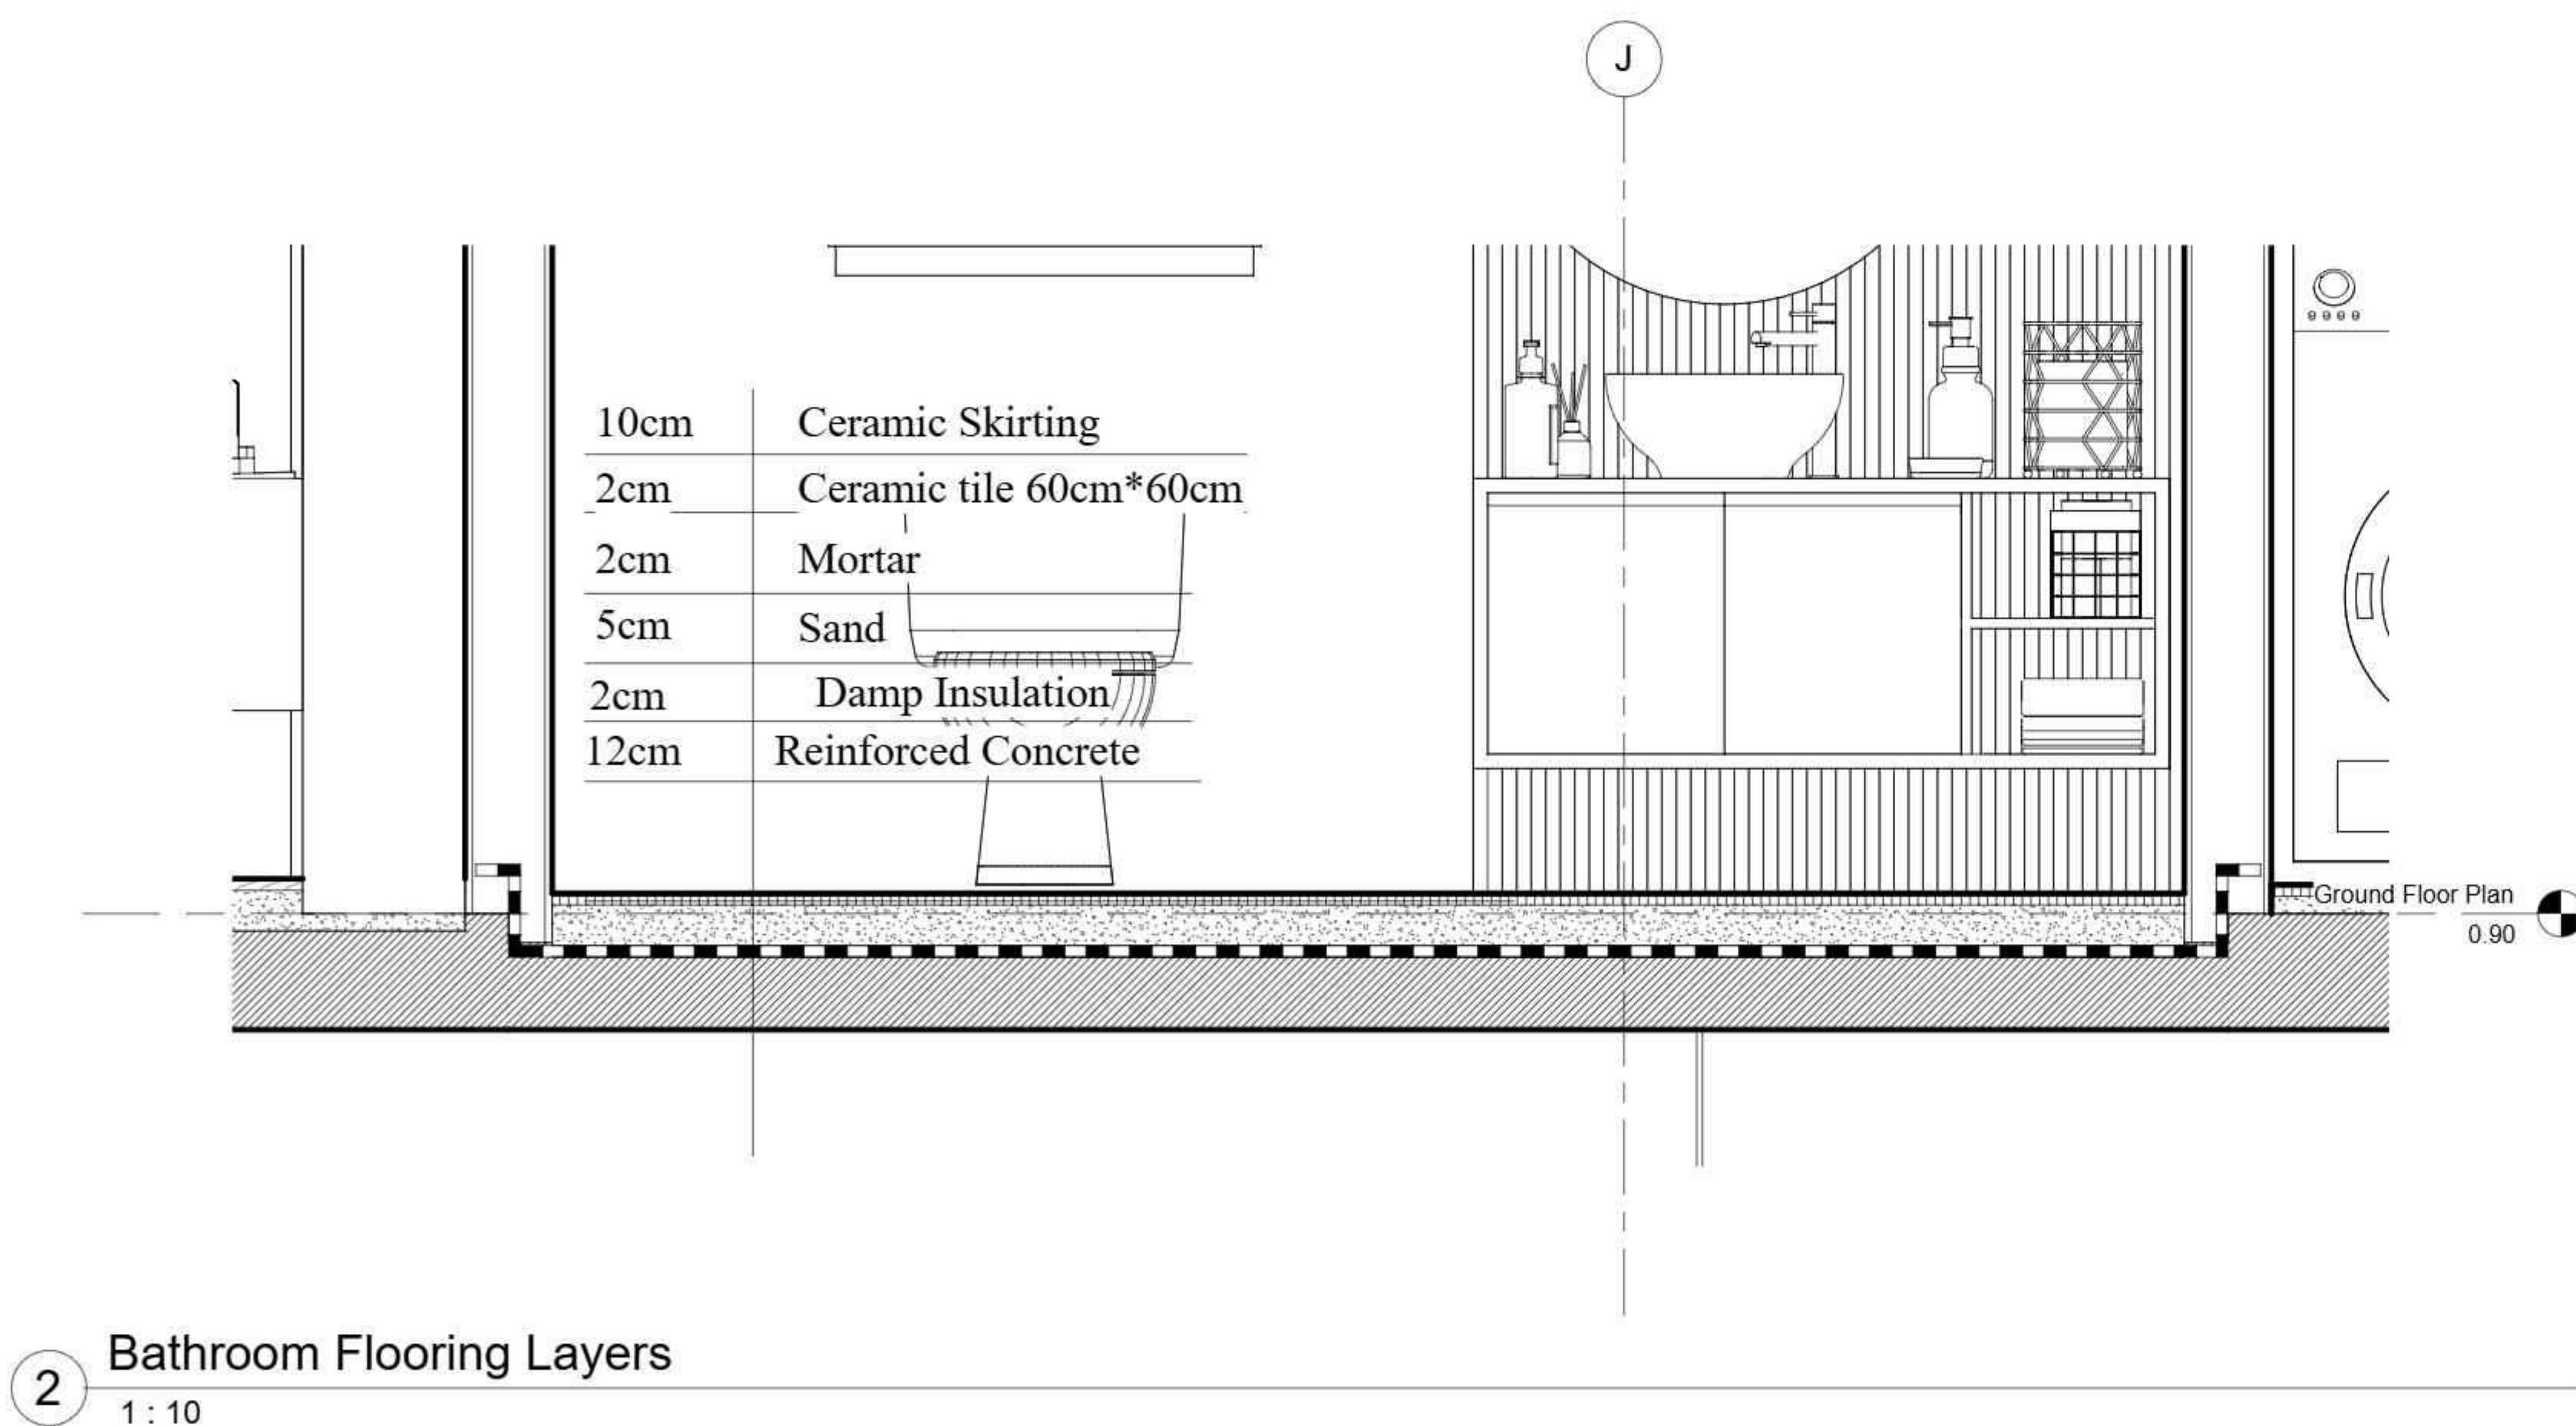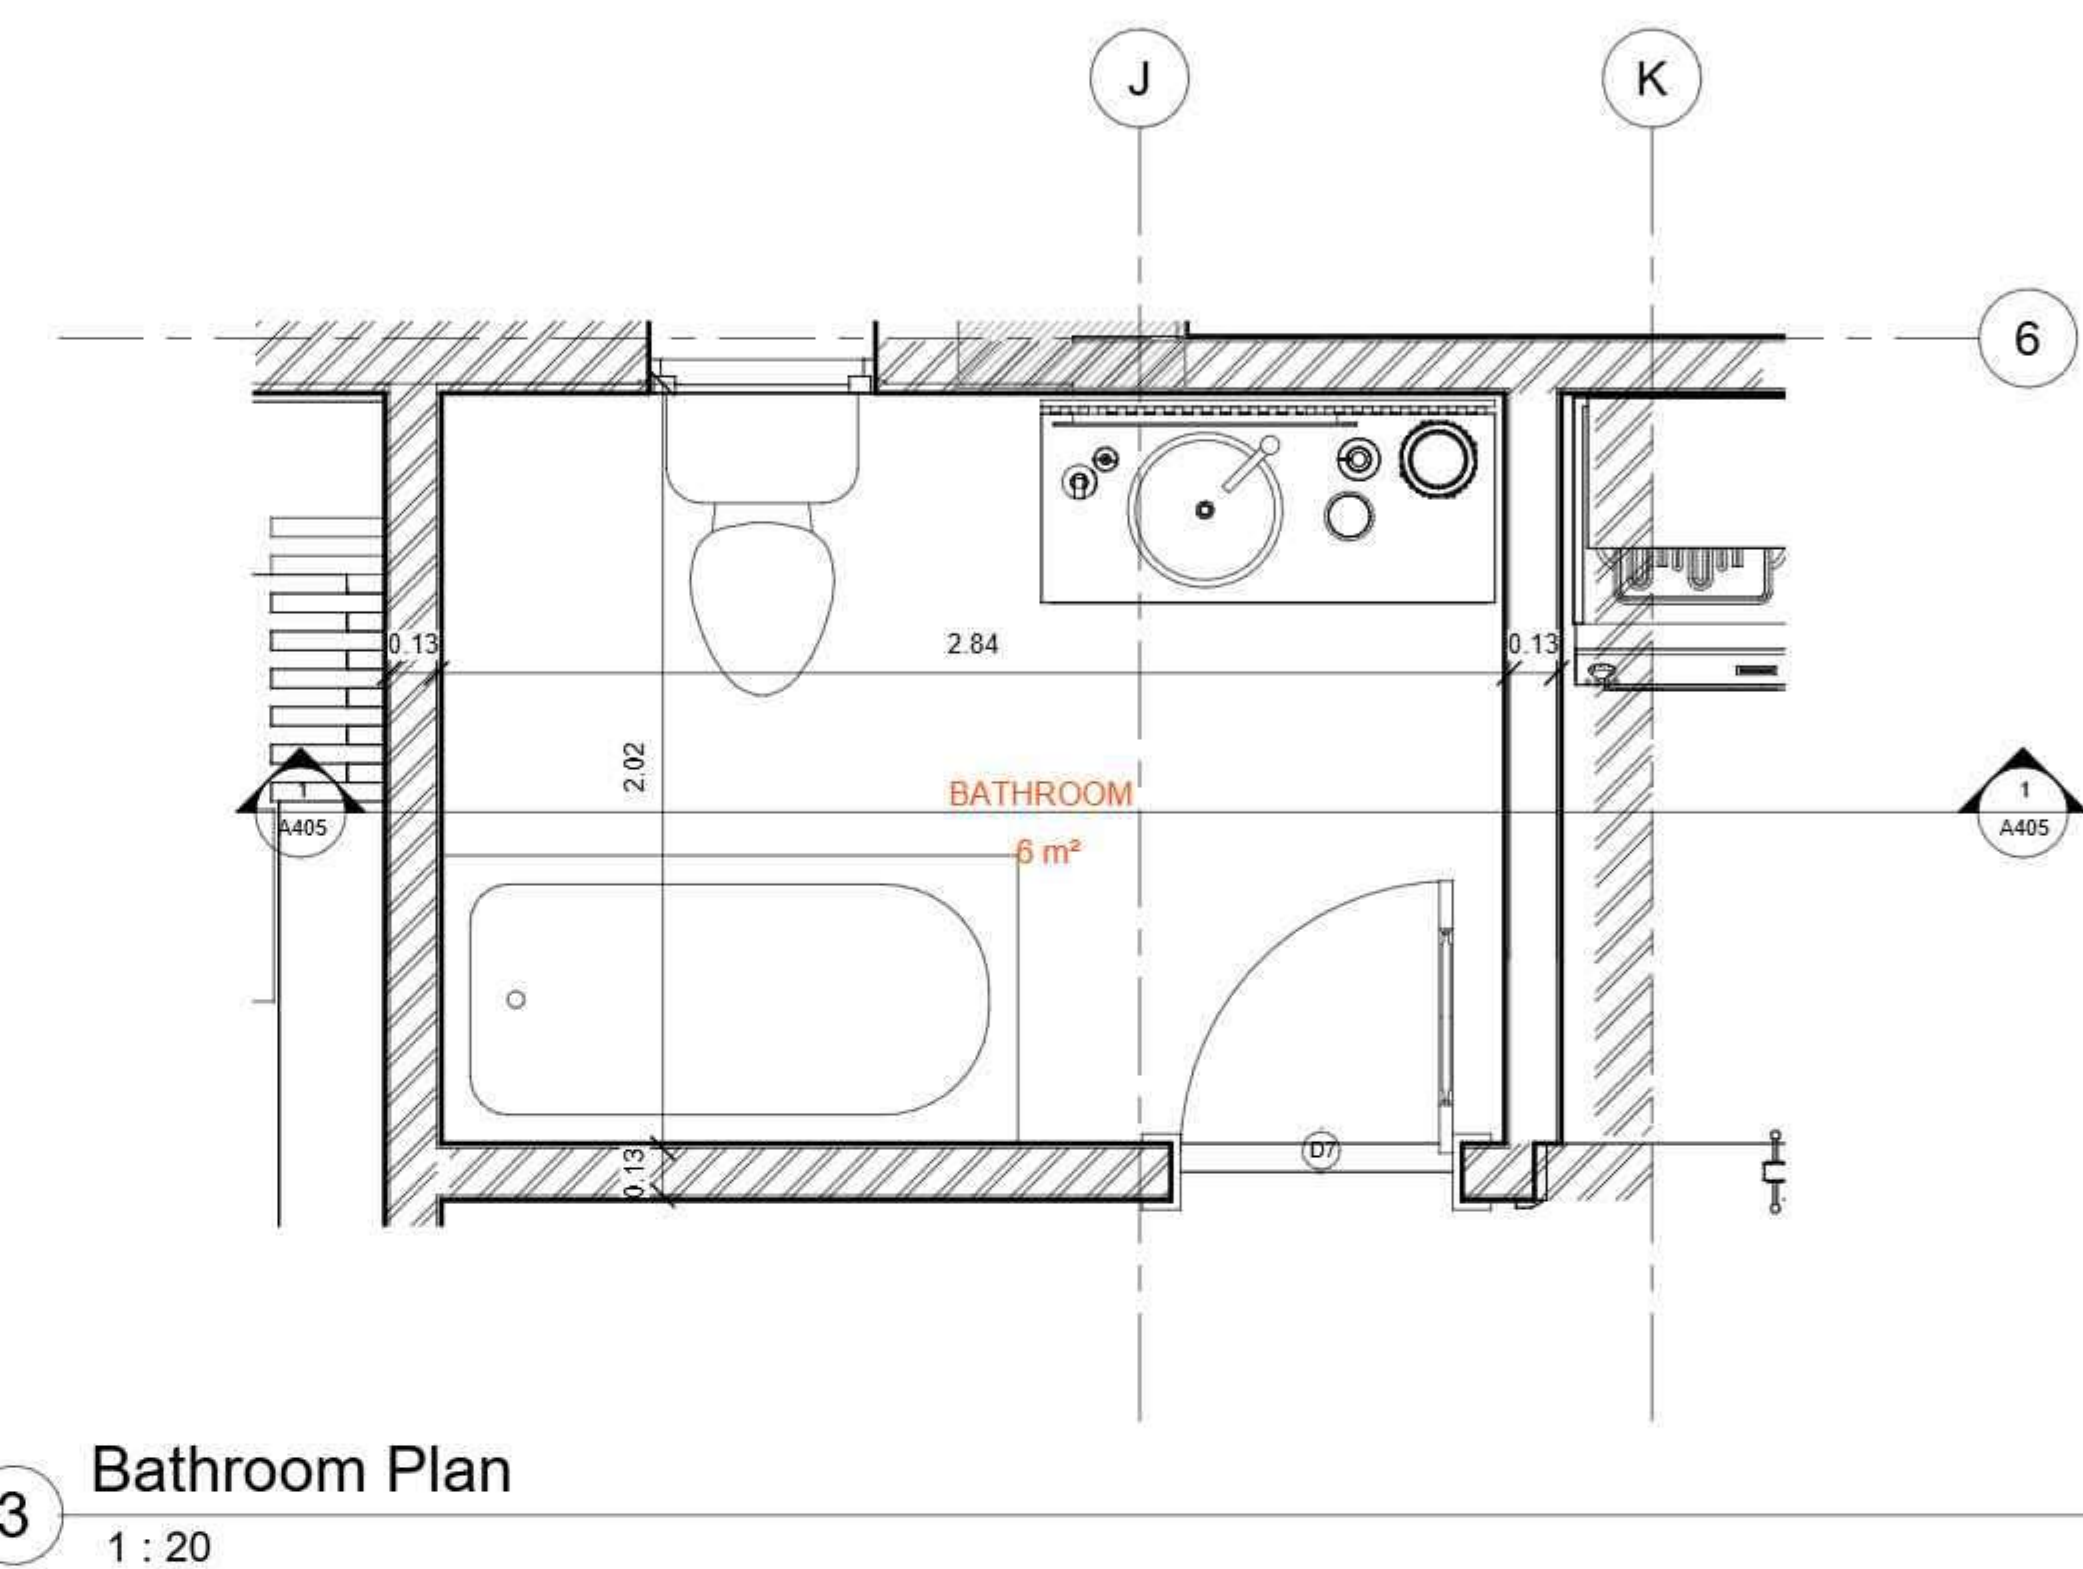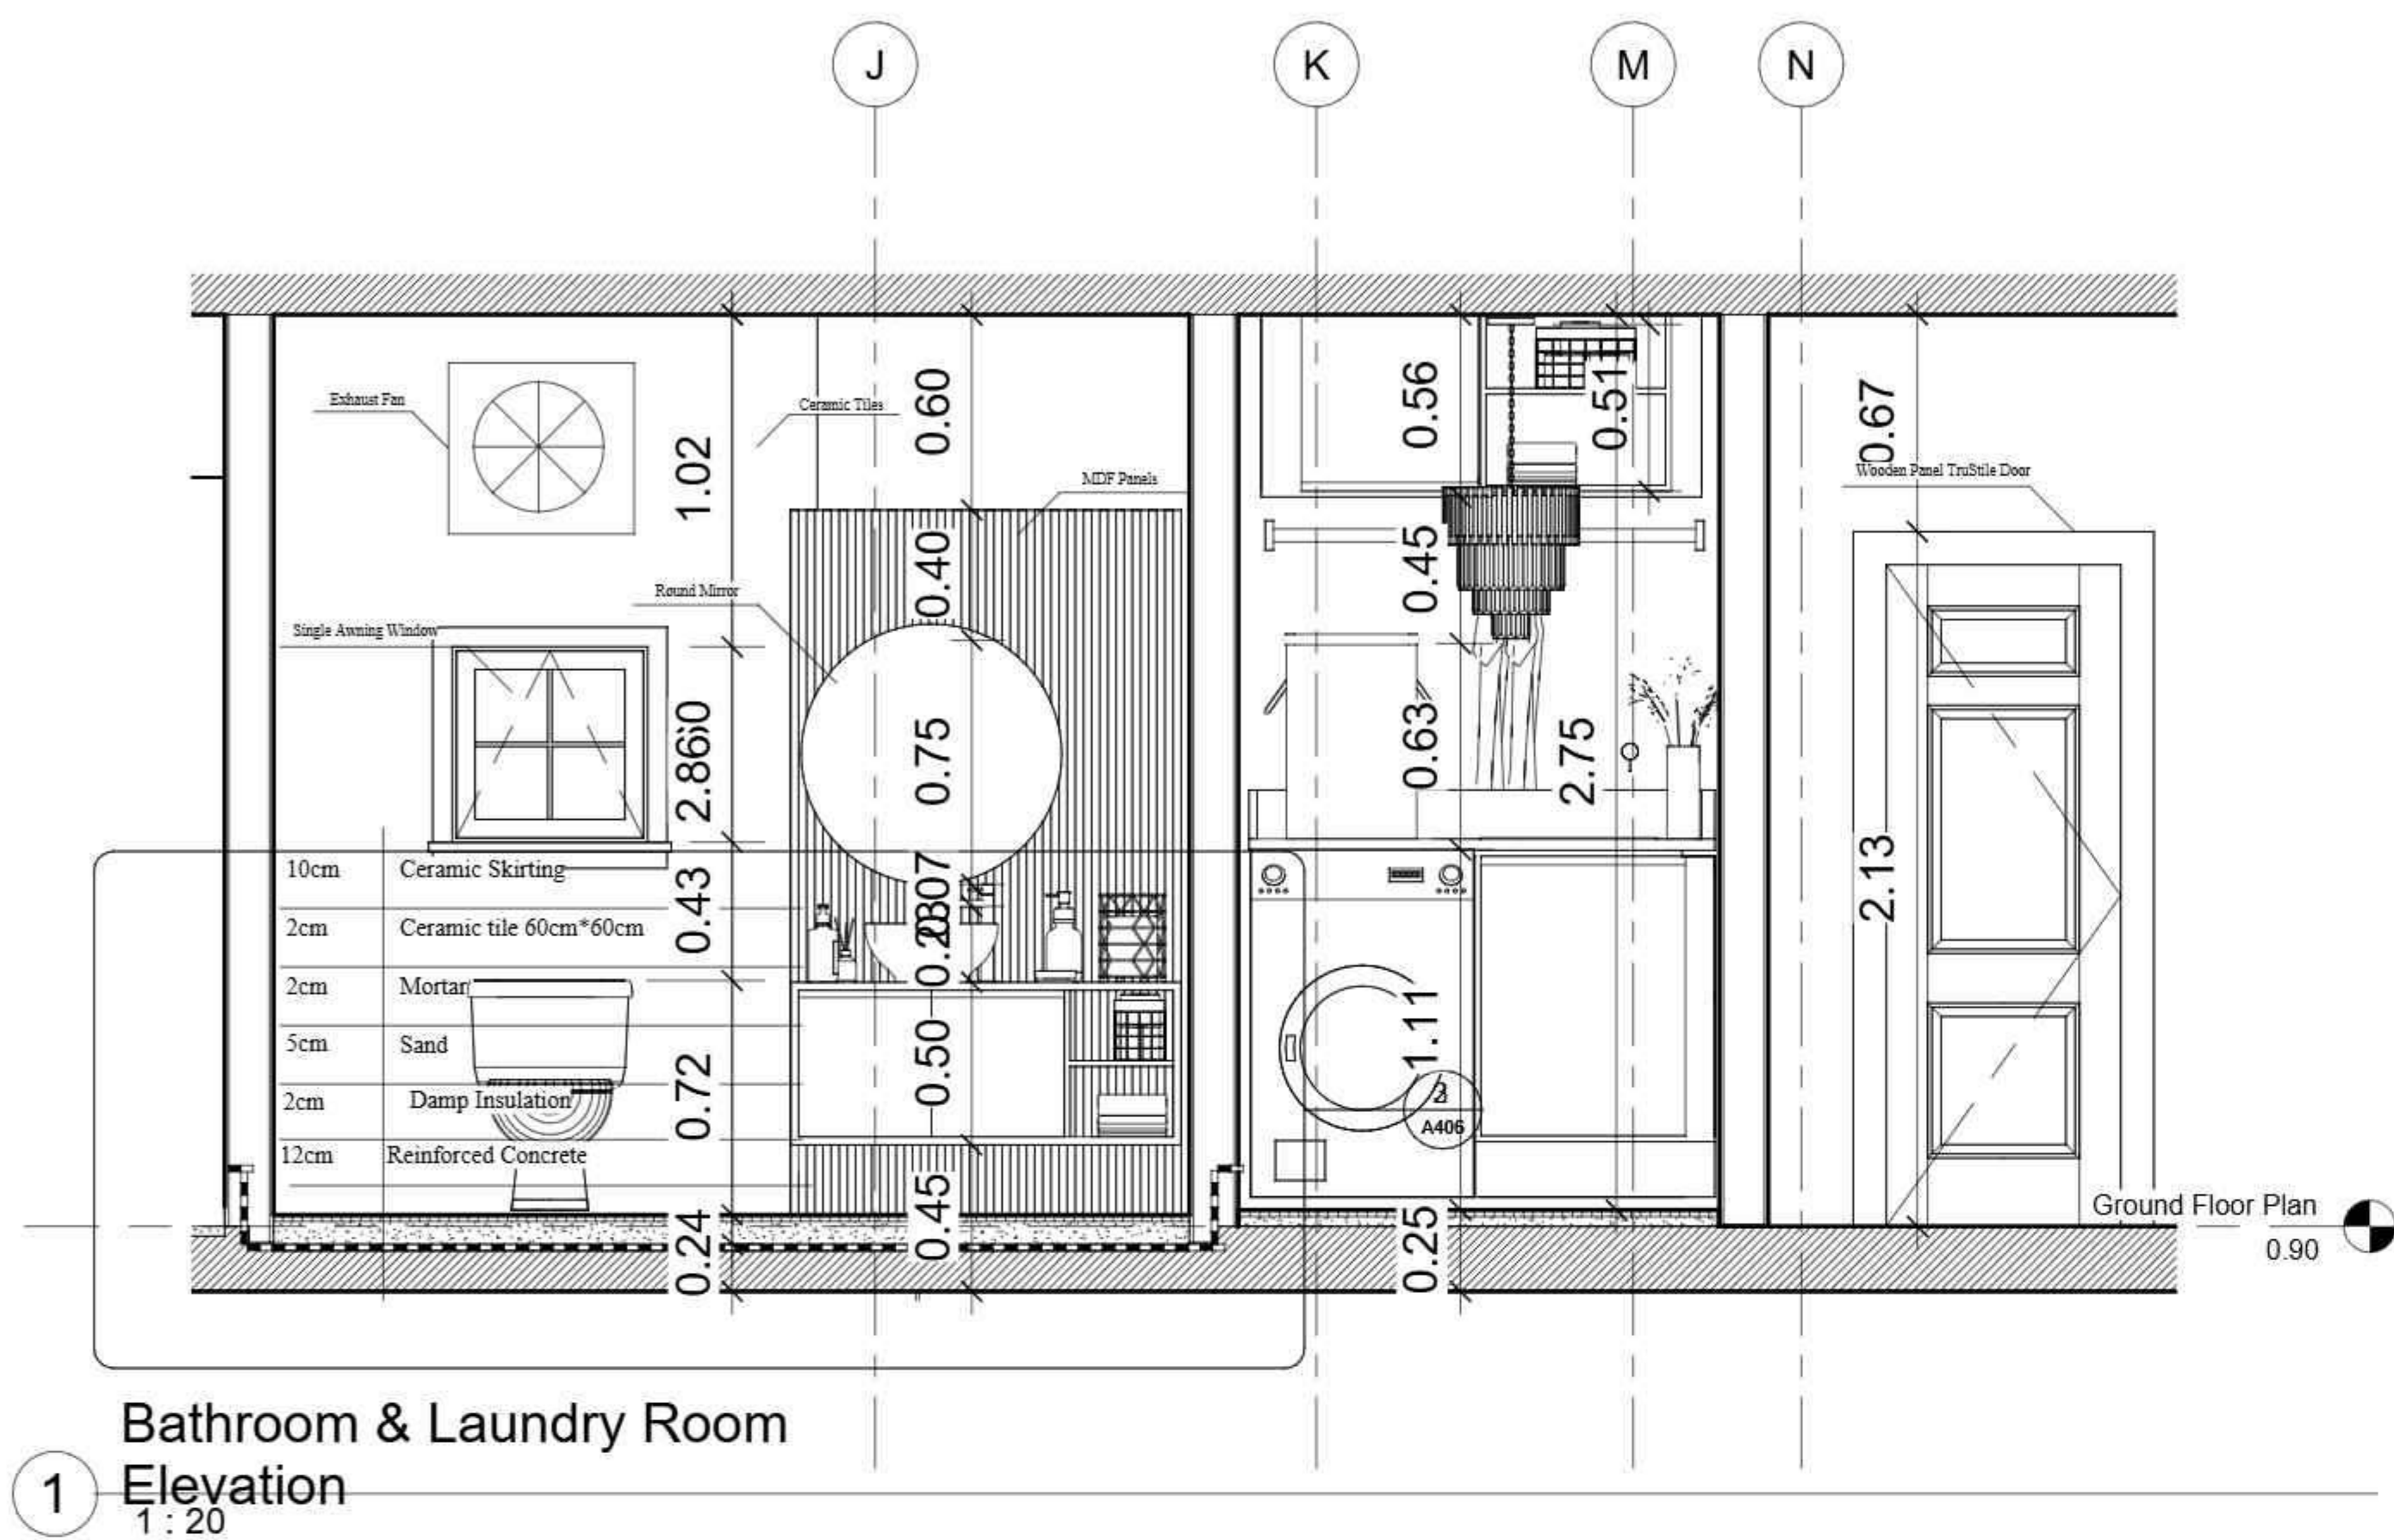

OWNER:



OCTOBER UNIVERSITY
FOR MODERN SCIENCES & ARTS
Architectural Engineering Department
Spring 2025

CLIENTS NAME:
Dr. Tarek Galal
Eng. Hend
Eng. Nermeen
Eng. Yousra

Student Name: Hadeel Zakaria
ID: 220009

PROJECT NAME:
APARTMENT BUILDING

SHEET NAME:

SHEET NO:

SCALE:

DATE: 13-5-2025

GENERAL NOTES:

- ALL MATERIALS & WORK PRACTICES SHALL COMPLY WITH, BUT NOT LIMITED TO THE BUILDING REGULATION 2019, THE NATIONAL CONSTRUCTION CODE of EGYPT UNLESS OTHERWISE SPECIFIED.

-ALL DIMENSIONS ARE IN METERS. IF IN DOUBT ASK, DO NOT SCALE.

-THESE DRAWINGS SHALL BE READ IN CONJUNCTION WITH ALL RELEVANT STRUCTURAL + ALL OTHER CONSULTANTS DRAWINGS/DETAILS & WITH ANY OTHER WRITTEN INSTRUCTIONS ISSUED IN THE COURSE OF THE CONTRACT.

- THESE DRAWINGS SHALL BE READ IN CONJUNCTION WITH ANY ENERGY RATING REPORT + SHALL BE CONSTRUCTED IN ACCORDANCE WITH THE STAMPED PLANS ENDORSED BY THE ACCREDITED THERMAL PERFORMANCE ASSESSOR WITHOUT ALTERATION



OWNER:



OCTOBER UNIVERSITY
FOR MODERN SCIENCES & ARTS
Architectural Engineering Department
Spring 2025

CLIENTS NAME:
Dr. Tarek Galal
Eng. Hend
Eng. Nermeen
Eng. Yousra


Student Name: Hadeel Zakaria
ID: 220009

PROJECT NAME:
APARTMENT BUILDING


SHEET NAME:
DETAILS

SHEET NO: A405
SCALE: 1:-


DATE: 13-5-2025

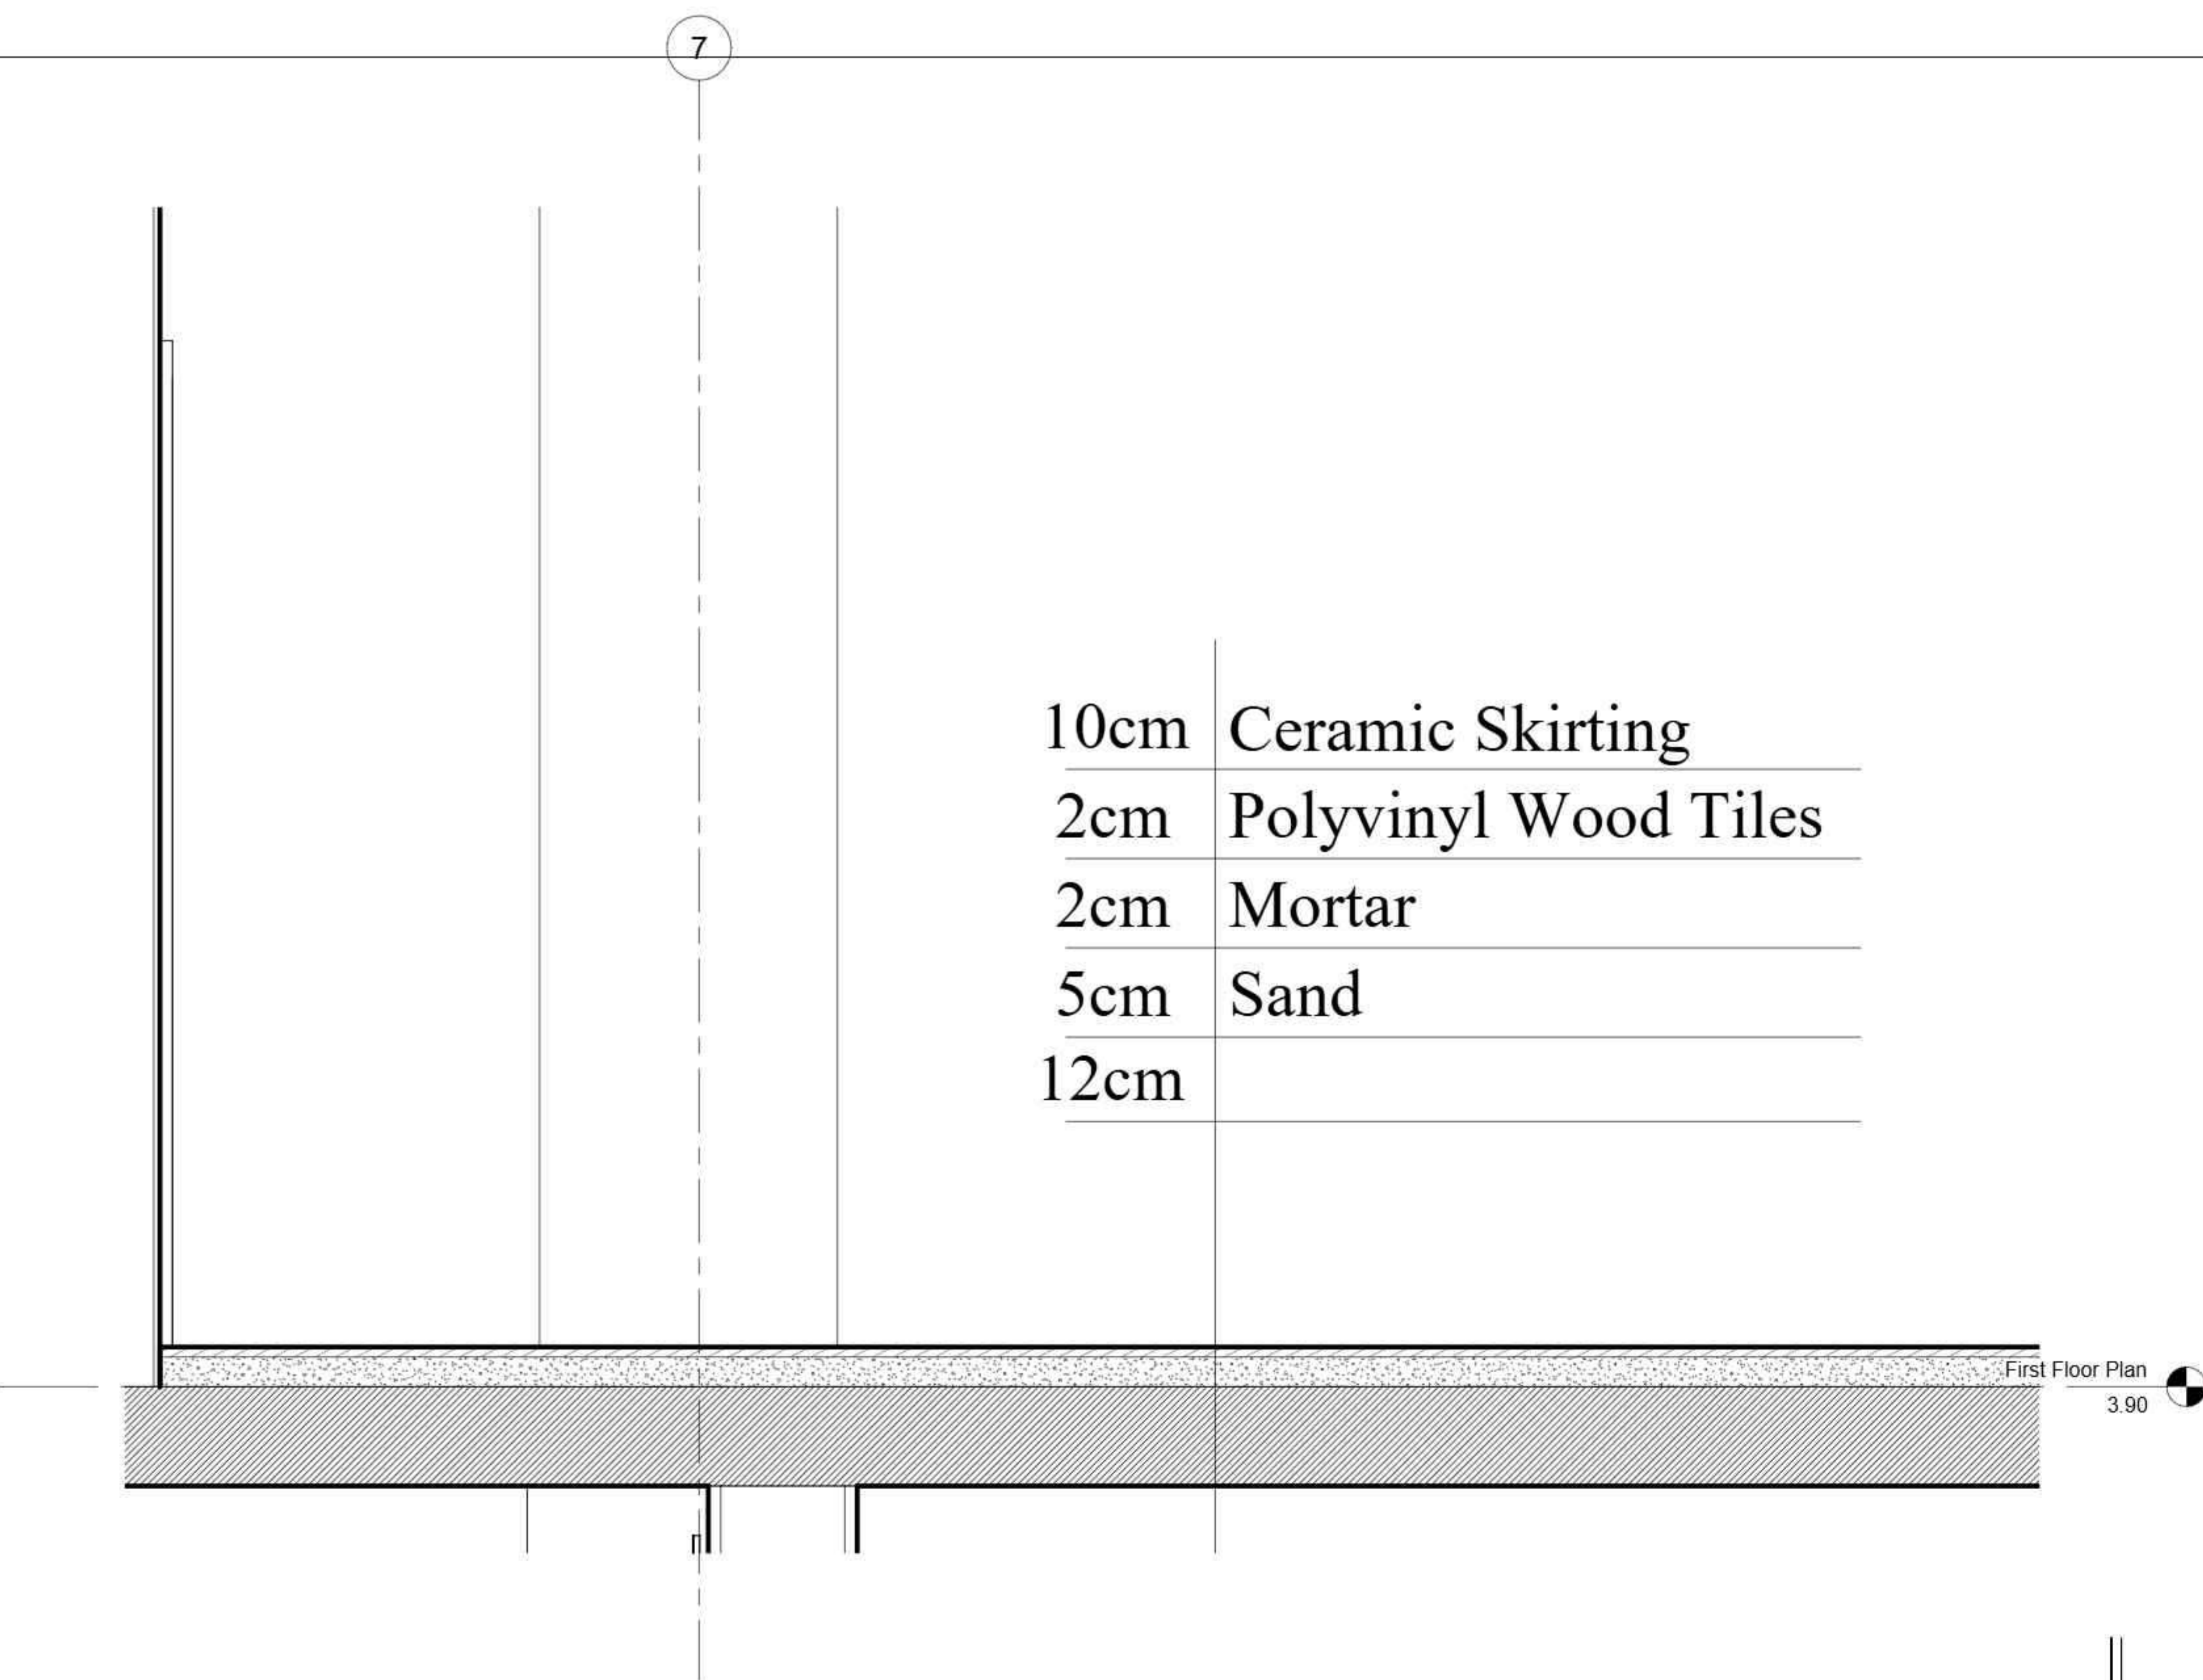

1 Typical Floor Layers
1 : 10

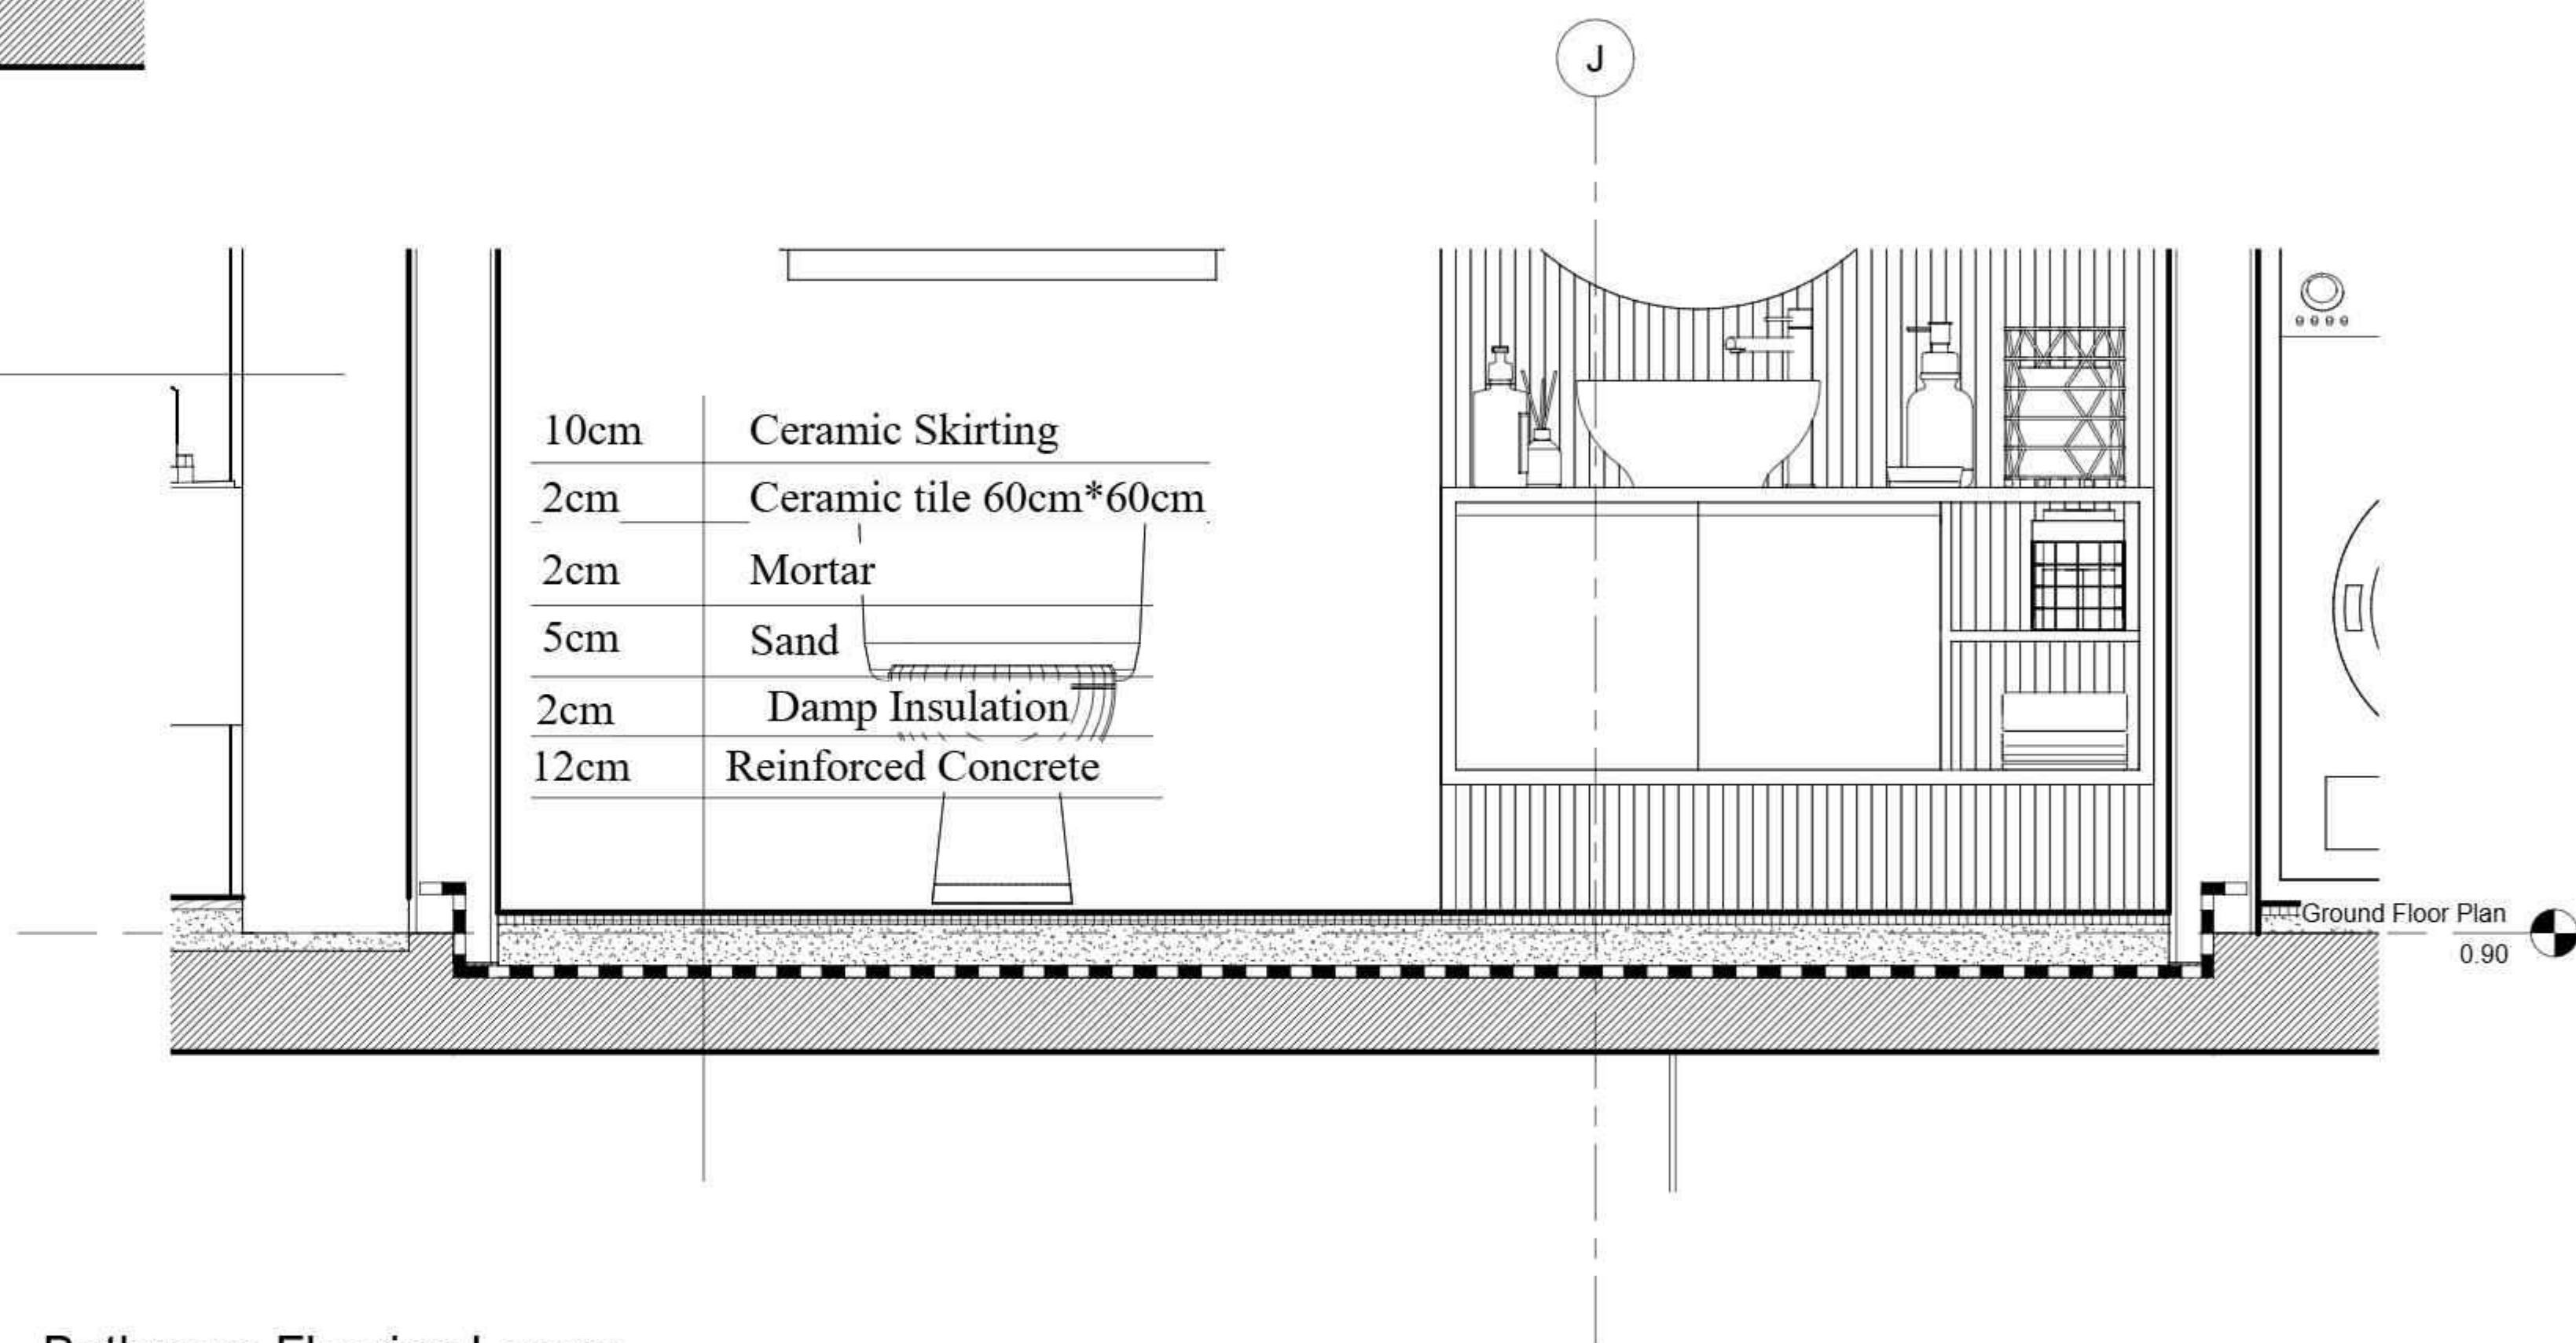

3 Bathroom Flooring Layers
Copy 1
1 : 10

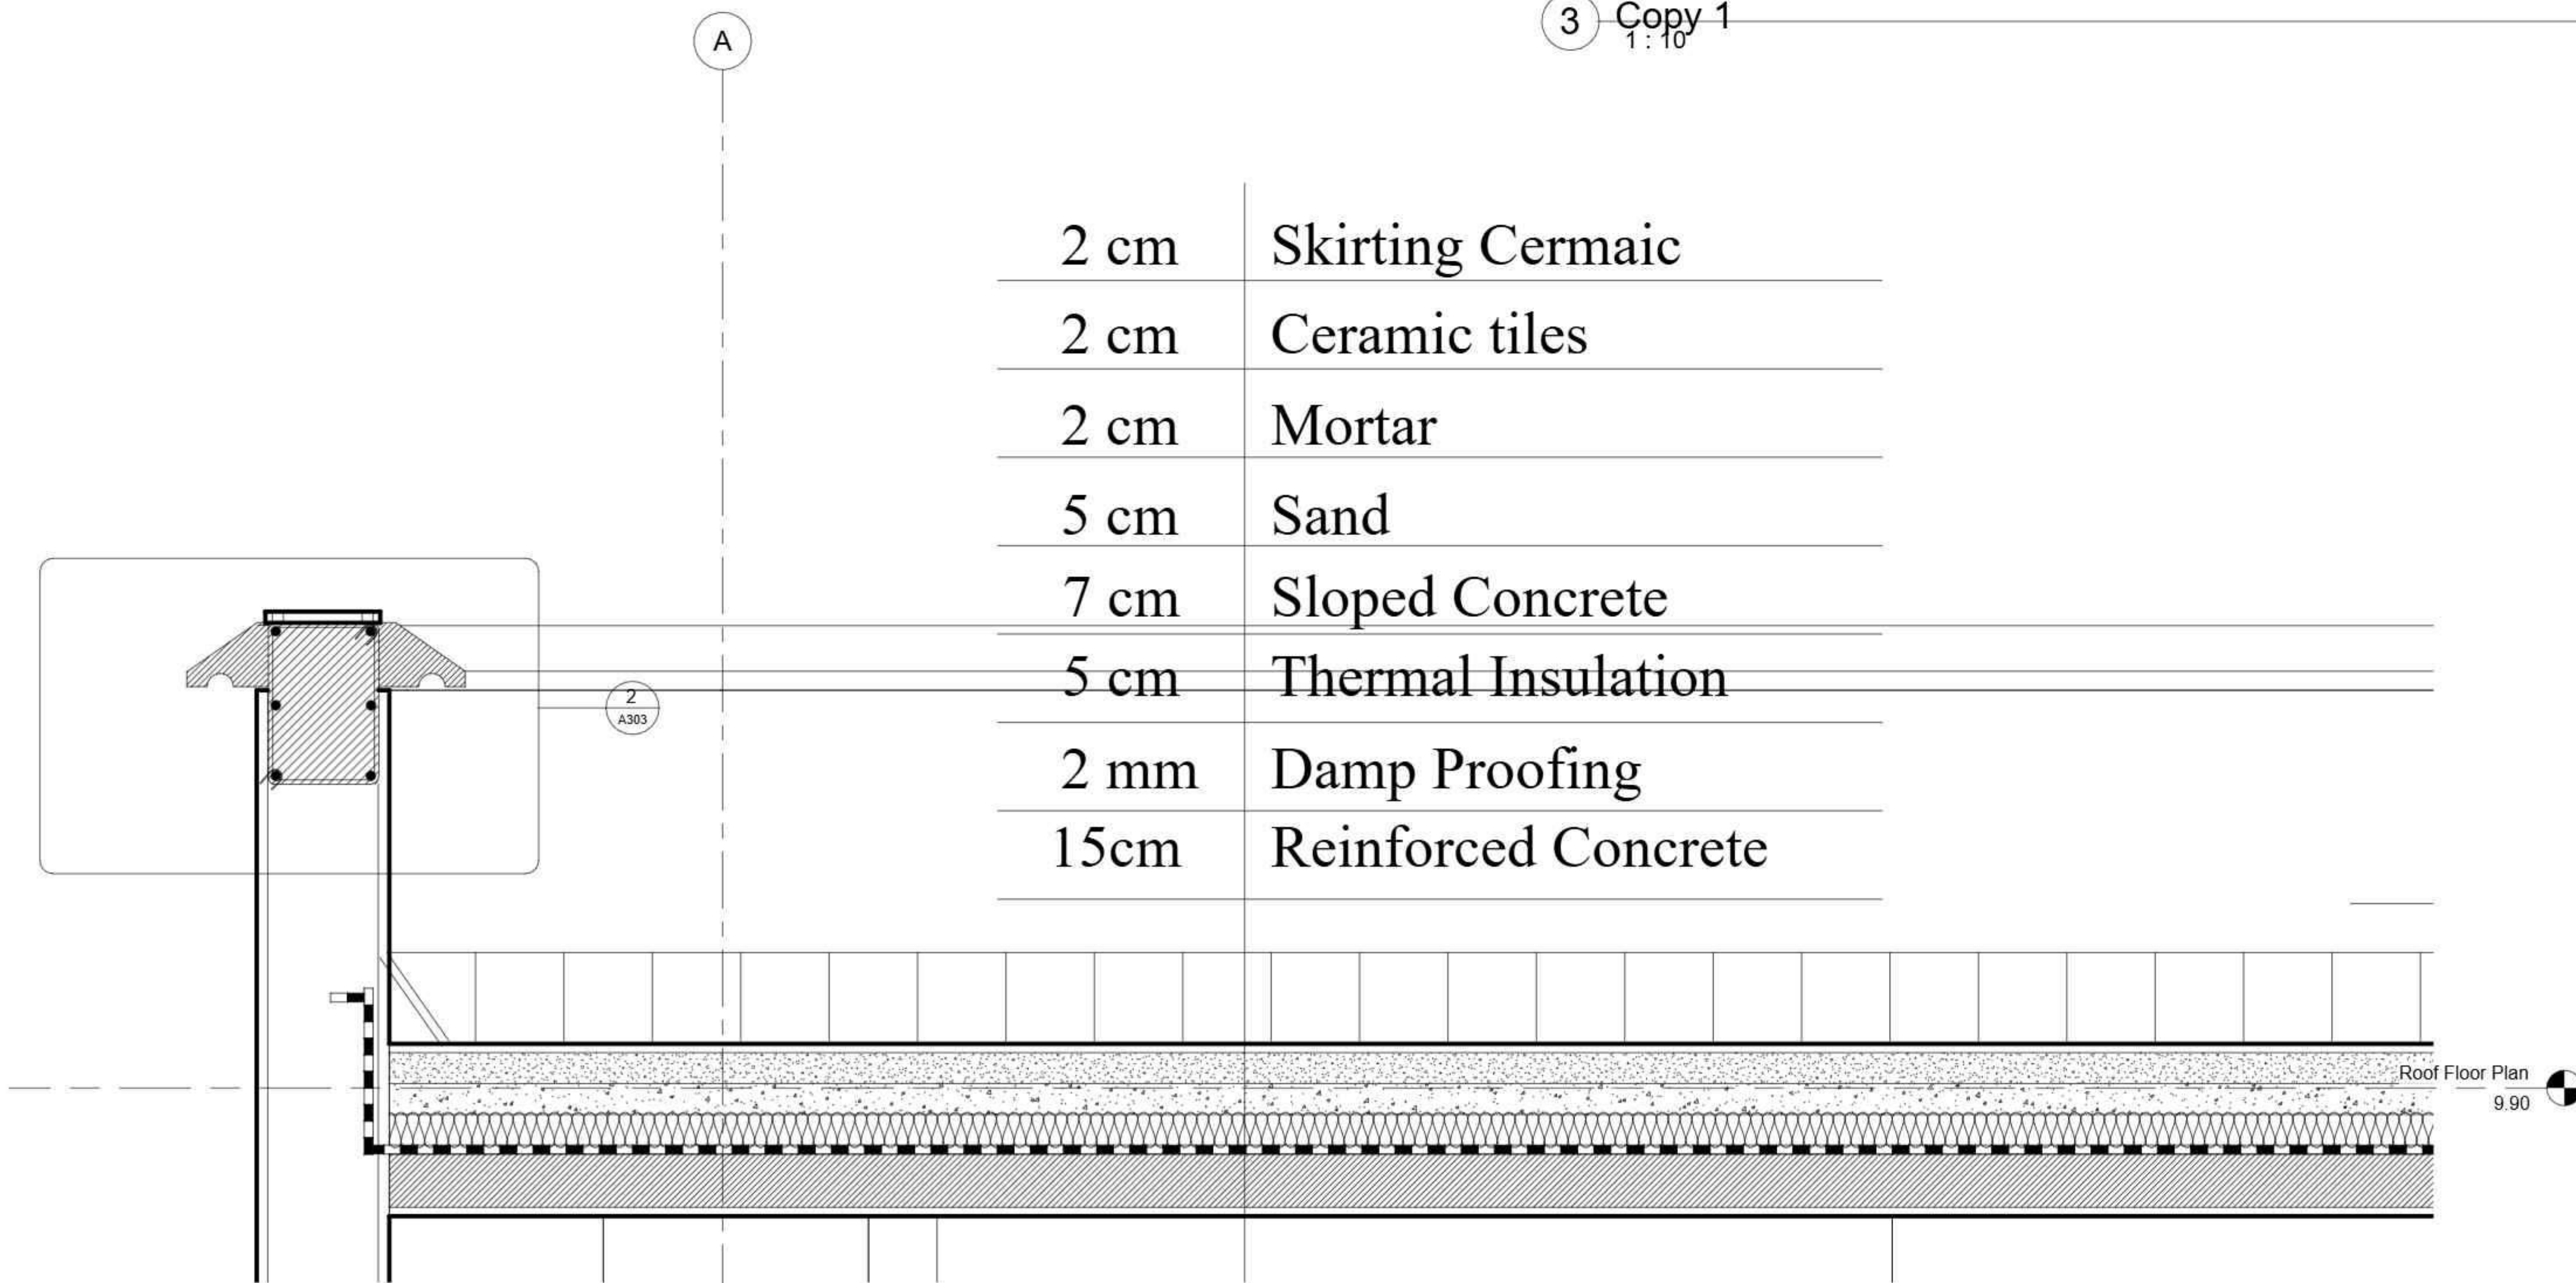

2 Roof Layers
1 : 10

GENERAL NOTES:

- ALL MATERIALS & WORK PRACTICES SHALL COMPLY WITH, BUT NOT LIMITED TO THE BUILDING REGULATION 2019, THE NATIONAL CONSTRUCTION CODE OF EGYPT UNLESS OTHERWISE SPECIFIED.

- ALL DIMENSIONS ARE IN METERS. IF IN DOUBT ASK, DO NOT SCALE.

- THESE DRAWINGS SHALL BE READ IN CONJUNCTION WITH ALL RELEVANT STRUCTURAL + ALL OTHER CONSULTANTS DRAWINGS/DETAILS & WITH ANY OTHER WRITTEN INSTRUCTIONS ISSUED IN THE COURSE OF THE CONTRACT.

- THESE DRAWINGS SHALL BE READ IN CONJUNCTION WITH ANY ENERGY RATING REPORT + SHALL BE CONSTRUCTED IN ACCORDANCE WITH THE STAMPED PLANS ENDORSED BY THE ACCREDITED THERMAL PERFORMANCE ASSESSOR WITHOUT ALTERATION



OWNER:

OCTOBER UNIVERSITY
FOR MODERN SCIENCES & ARTS
Architectural Engineering Department
Spring 2025

CLIENTS NAME:

Dr. Tarek Galal
Eng. Hend
Eng. Nermeen
Eng. Yousra

Student Name: Hadeel Zakaria
ID: 220009

PROJECT NAME:
APARTMENT BUILDING

SHEET NAME:

DOOR TYPES


SHEET NO:

A407


SCALE:

1:250

DATE: 13-5-2025

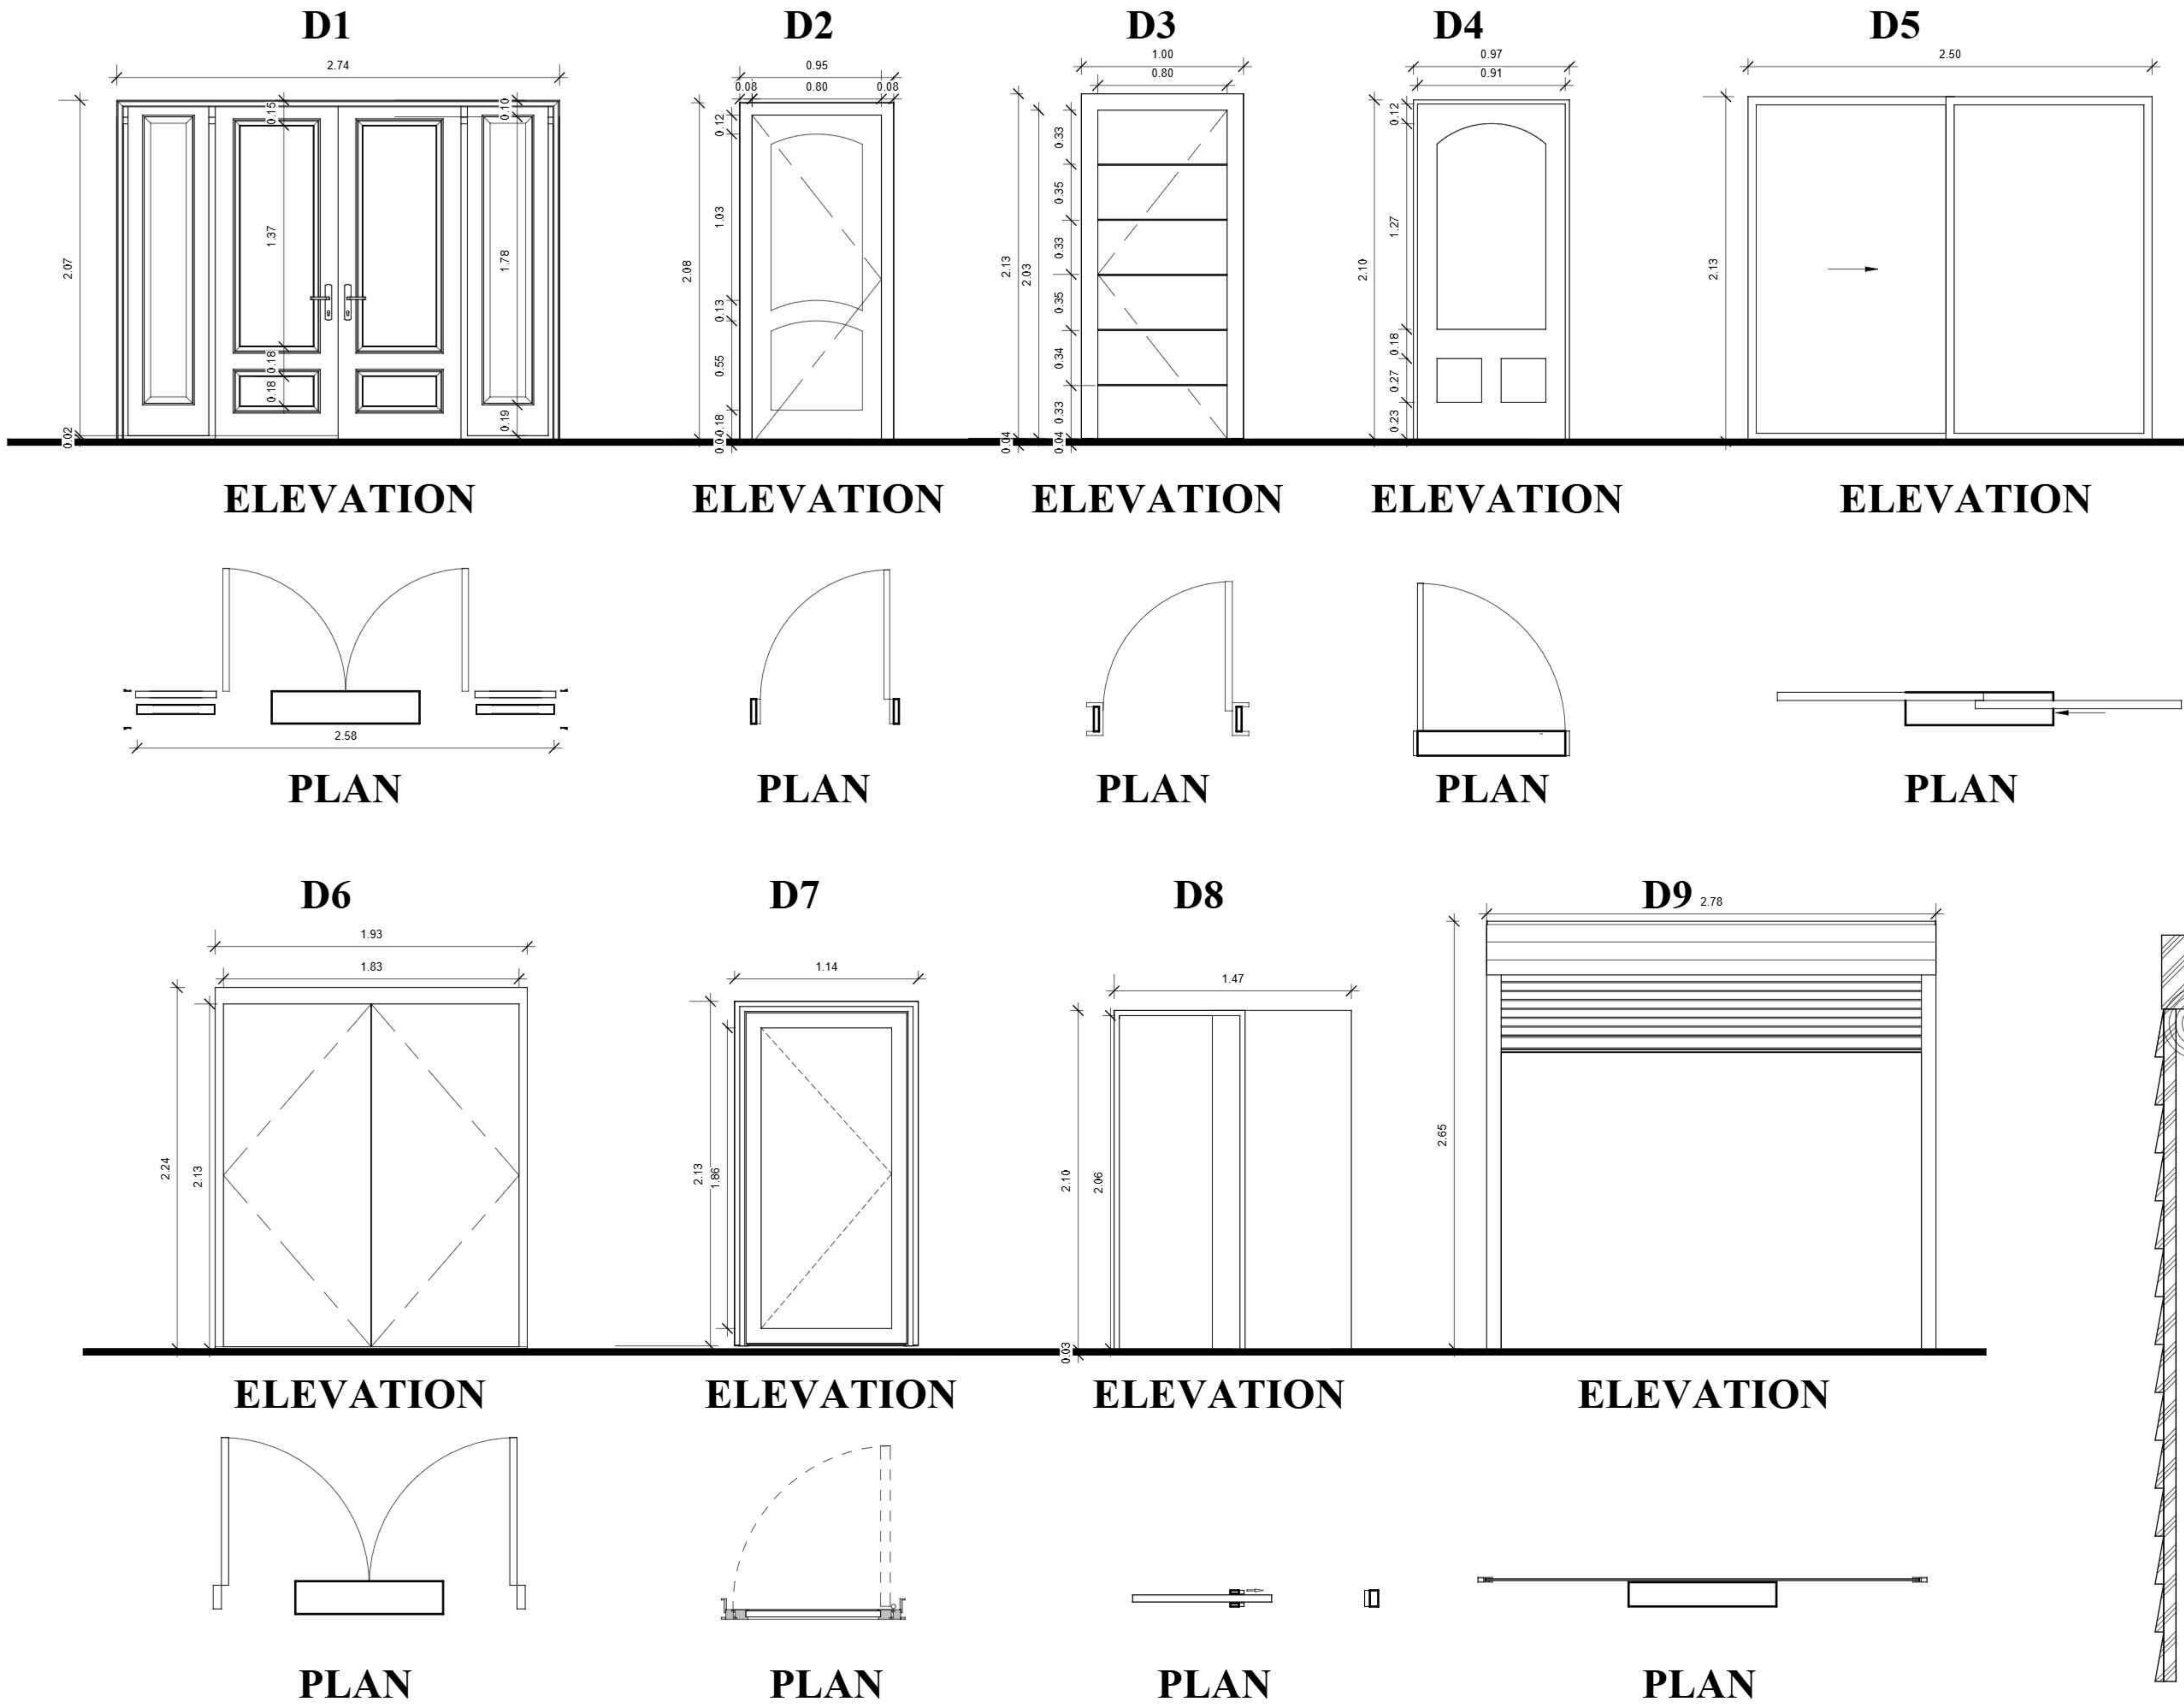


Mark		D1	D2	D3	D4	D5	D6	D7	D8	D9
Type		Double Panel	Single Door	Single Door	Single Glass Door	Double Door	Double Door	Single Door	Sliding Door	Coiling Door
Description		Steel Double Panel Door with Wooden Decorations	Wooden 2 Panel Door	Wooden Interior Door with Frames	Exterior Single Entry Half Arched Glass Door	Double Glass Sliding Door	Double Stainless & Plywood Exterior Door	Single Wooden Trustile Door	Sliding Pocket Wooden Door	Garage Door
Location	B.F				Guard Room		Building Entrance	Bathroom		Ramp
	G.F	Entrance	Bedrooms	Apartment Door	Small Terrace	Outdoor Garden		Bathroom	Toilets	
	F.F		Bedrooms	Apartment Door	Small Terrace	Main Terraces		Bathroom	Toilets Dressing Room	
	R.F							Services		

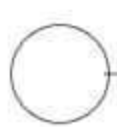

DOOR TYPES

1 : 20

GENERAL NOTES:
- ALL MATERIALS & WORK PRACTICES SHALL COMPLY WITH, BUT NOT LIMITED TO THE BUILDING REGULATION 2019, THE NATIONAL CONSTRUCTION CODE OF EGYPT UNLESS OTHERWISE SPECIFIED.
- ALL DIMENSIONS ARE IN METERS. IF IN DOUBT ASK, DO NOT SCALE.
- THESE DRAWINGS SHALL BE READ IN CONJUNCTION WITH ALL RELEVANT STRUCTURAL + ALL OTHER CONSULTANTS DRAWINGS/DETAILS & WITH ANY OTHER WRITTEN INSTRUCTIONS ISSUED IN THE COURSE OF THE CONTRACT.
- THESE DRAWINGS SHALL BE READ IN CONJUNCTION WITH ANY ENERGY RATING REPORT + SHALL BE CONSTRUCTED IN ACCORDANCE WITH THE STAMPED PLANS ENDORSED BY THE ACCREDITED THERMAL PERFORMANCE ASSESSOR WITHOUT ALTERATION

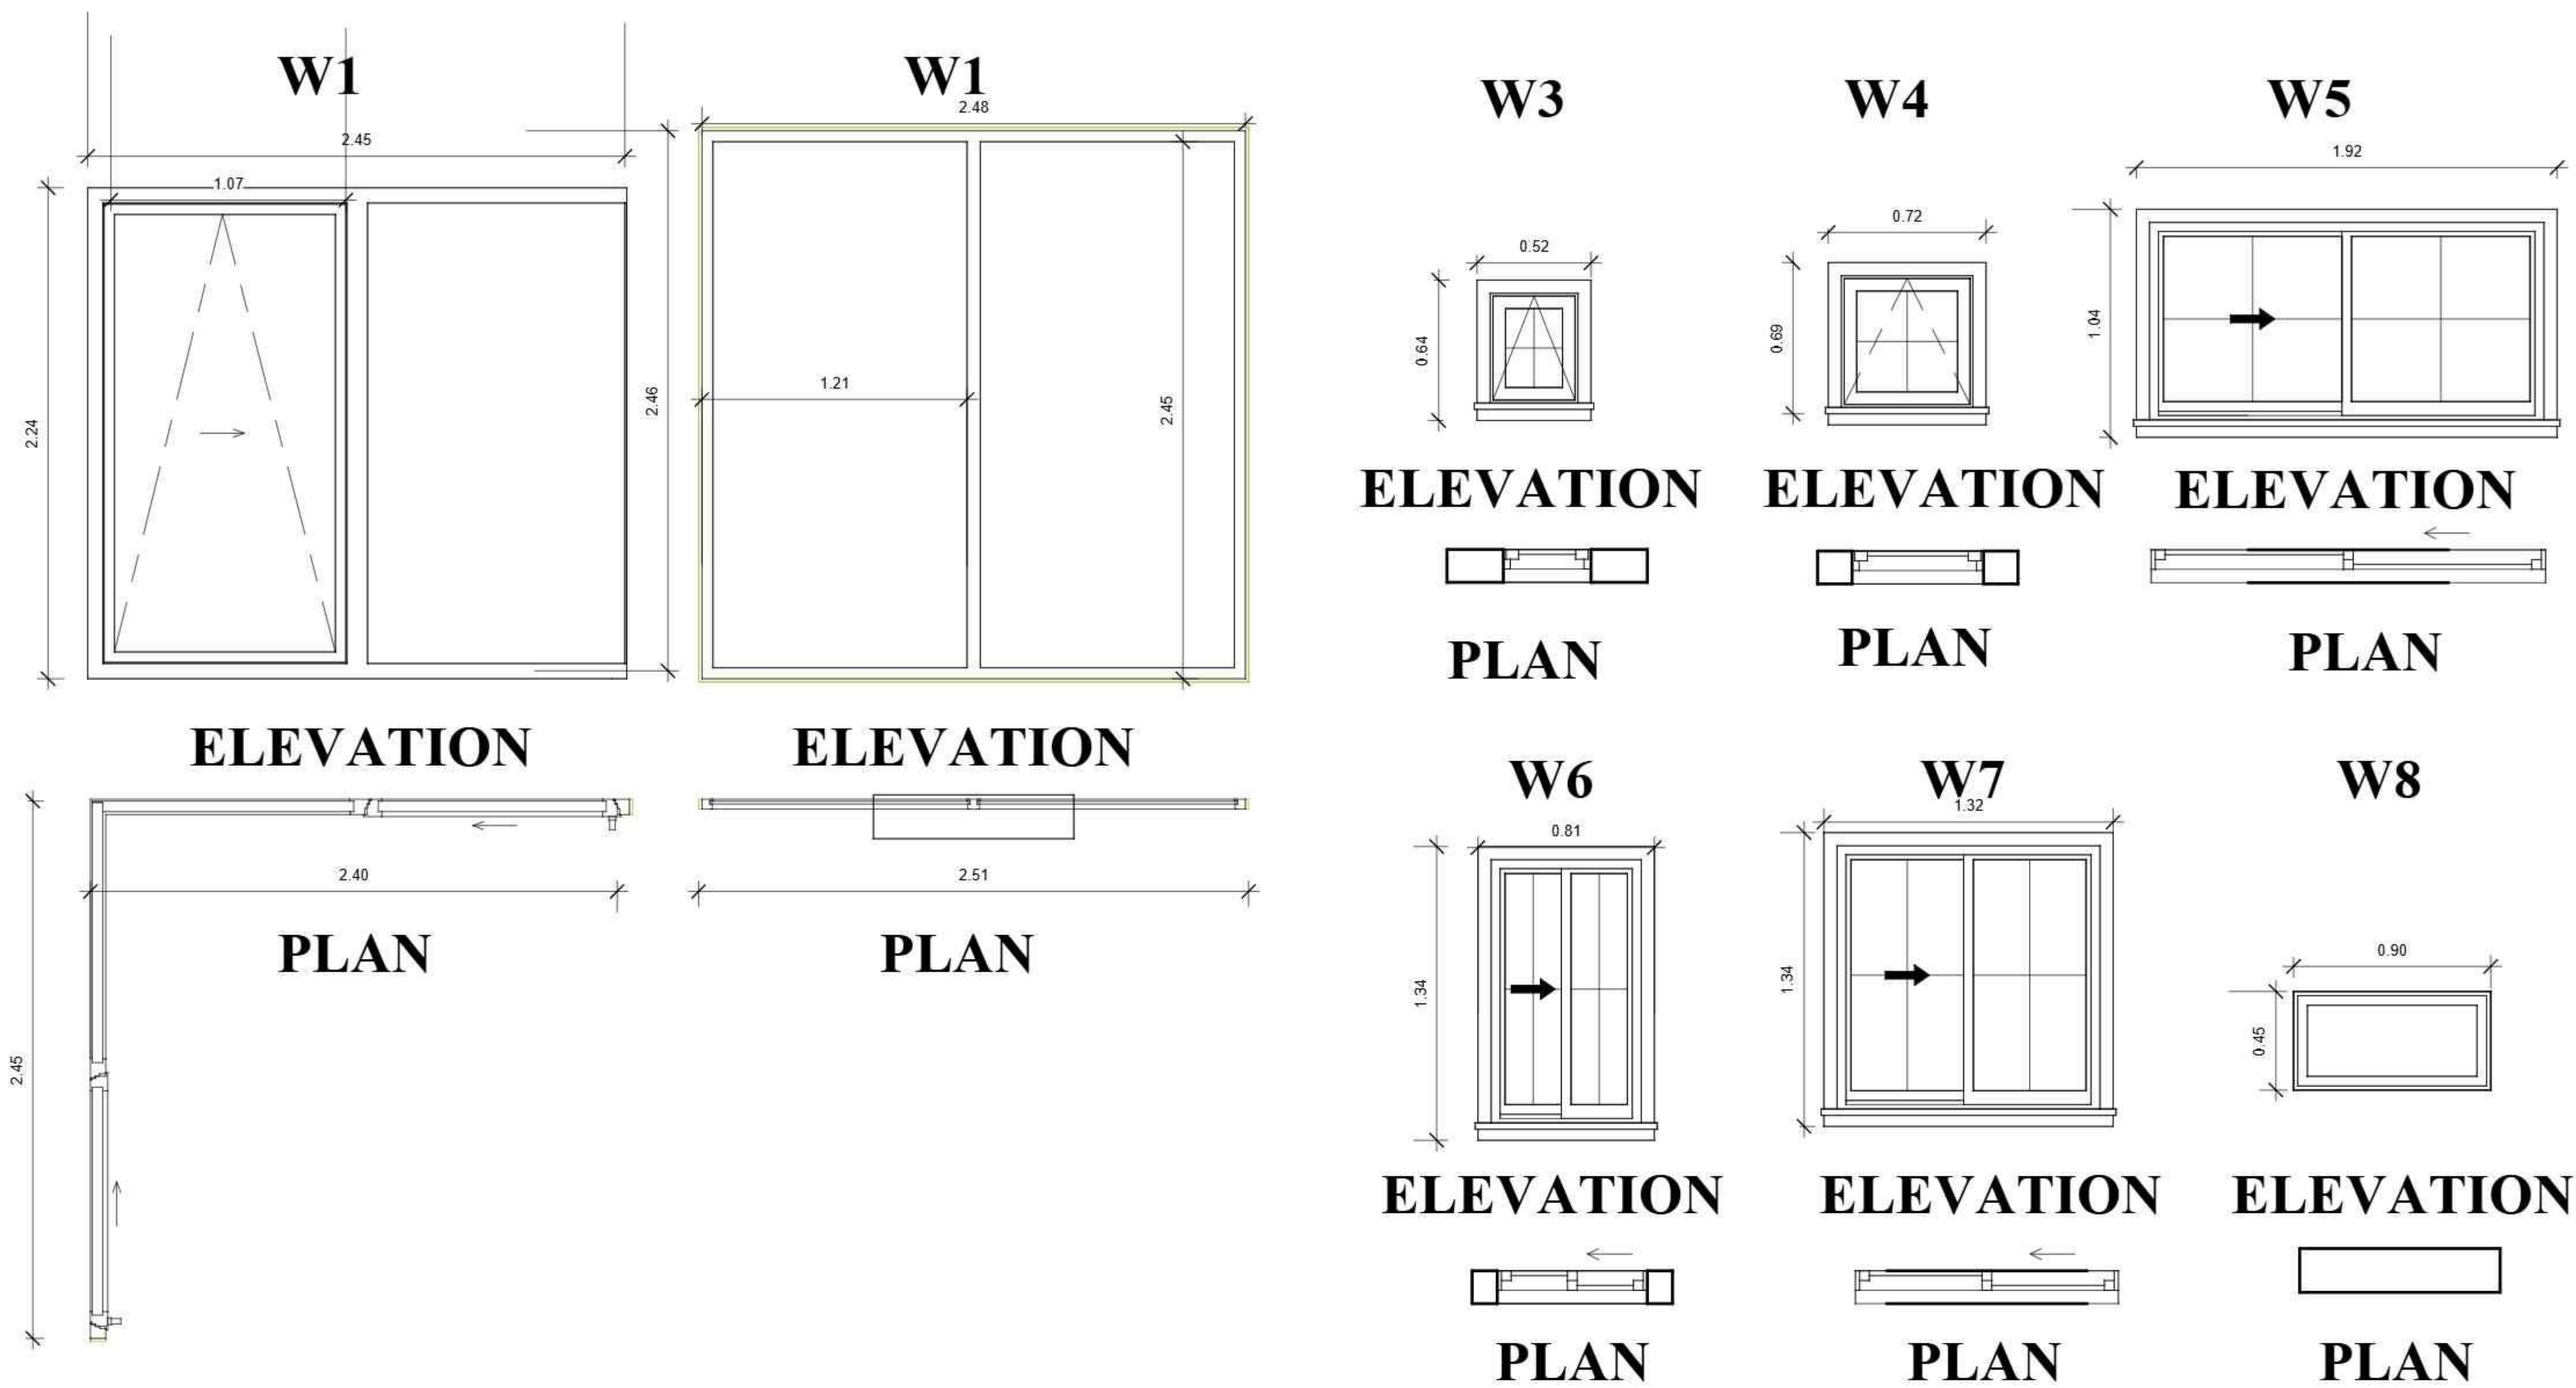

Mark		W1	W2	W3	W4	W5	W6	W7	W8
Type		Structural Corner Window	Double Fixed Panel	Single Window	Single Window	Double Window	Double Window	Double Window	Fixed Window
Description		Structural Corner Window With 4 Panels Window	Double Fixed Glass Window	Steel Awning Single Windows	Steel Awning Single Windows	Double Glass Sliding Window	Double Glass Sliding Window	Double Glass Sliding Window	Single Fixed Window
Location	B.F			Interior walls	Bathroom				
	G.F	Living Rooms	Bedrooms		Bathroom	Living Room	Kitchen		
	F.F		Bedrooms Living Room		Bathroom			Kitchen	
	R.F							Stairs	Upper Roof

WINDOW TYPES
1 : 20



OWNER:

CLIENTS NAME:
Dr. Tarek Galal
Eng. Hend
Eng. Nermeen
Eng. Yousra

Student Name: Hadeel Zakaria
ID: 220009

PROJECT NAME:
APARTMENT BUILDING

SHEET NAME:
WINDOWS TYPES

SHEET NO: A408
SCALE: 1:250

DATE: 13-5-2025

GENERAL NOTES:
- ALL MATERIALS & WORK PRACTICES SHALL COMPLY WITH, BUT NOT LIMITED TO THE BUILDING REGULATION 2019, THE NATIONAL CONSTRUCTION CODE OF EGYPT UNLESS OTHERWISE SPECIFIED.
- ALL DIMENSIONS ARE IN METERS. IF IN DOUBT ASK, DO NOT SCALE.
- THESE DRAWINGS SHALL BE READ IN CONJUNCTION WITH ALL RELEVANT STRUCTURAL + ALL OTHER CONSULTANTS DRAWINGS/DETAILS & WITH ANY OTHER WRITTEN INSTRUCTIONS ISSUED IN THE COURSE OF THE CONTRACT.
- THESE DRAWINGS SHALL BE READ IN CONJUNCTION WITH ANY ENERGY RATING REPORT + SHALL BE CONSTRUCTED IN ACCORDANCE WITH THE STAMPED PLANS ENDORSED BY THE ACCREDITED THERMAL PERFORMANCE ASSESSOR WITHOUT ALTERATION



OWNER:



OCTOBER UNIVERSITY
FOR MODERN SCIENCES & ARTS
Architectural Engineering Department
Spring 2025

CLIENTS NAME:
Dr. Tarek Galal
Eng. Hend
Eng. Nermeen
Eng. Yousra

Student Name: Hadeel Zakaria
ID: 220009

PROJECT NAME:
APARTMENT BUILDING

SHEET NAME:
BASEMENT PLAN

SHEET NO:
E101

SCALE:
1:50

DATE: 13-5-2025

Symbols	Description
	Main Distributor
	Secondary Distributor
	Single Gang Switch
	Double Gang Switch
	Single Socket
	Double Socket
	Bottom Single Socket
	Bottom Double Socket
	AC & Heater Switch
	Television Socket
	Internet Socket
	Single Floor Socket, Telephone
	Elevator Switch
	Floor Spot Light
	Wall Lamp
	Florescent Light
	Chandelier
	Fan Switch
	Fan
	AC
	Compressor
	Heater
	Bell

Electrical Symbols
1 : 100

Basement Floor Plan
(Electrical)
1 : 50

GENERAL NOTES:

- ALL MATERIALS & WORK PRACTICES SHALL COMPLY WITH, BUT NOT LIMITED TO THE BUILDING REGULATION 2019, THE NATIONAL CONSTRUCTION CODE OF EGYPT UNLESS OTHERWISE SPECIFIED.

- ALL DIMENSIONS ARE IN METERS. IF IN DOUBT ASK, DO NOT SCALE.

- THESE DRAWINGS SHALL BE READ IN CONJUNCTION WITH ALL RELEVANT STRUCTURAL + ALL OTHER CONSULTANTS DRAWINGS/DETAILS & WITH ANY OTHER WRITTEN INSTRUCTIONS ISSUED IN THE COURSE OF THE CONTRACT.

- THESE DRAWINGS SHALL BE READ IN CONJUNCTION WITH ANY ENERGY RATING REPORT + SHALL BE CONSTRUCTED IN ACCORDANCE WITH THE STAMPED PLANS ENDORSED BY THE ACCREDITED THERMAL PERFORMANCE ASSESSOR WITHOUT ALTERATION



OWNER:

CLIENTS NAME:

Dr. Tarek Galal
Eng. Hend
Eng. Nermeen
Eng. Yousra

Student Name: Hadeel Zakaria
ID: 220009

PROJECT NAME:
APARTMENT BUILDING

SHEET NAME:
GROUND FLOOR

SHEET NO:
E102

SCALE:
1:50

DATE: 13-5-2025



Course Info:
ASE 464
Working Drawings III

GENERAL NOTES:

- ALL MATERIALS & WORK PRACTICES SHALL COMPLY WITH, BUT NOT LIMITED TO THE BUILDING REGULATION 2019, THE NATIONAL CONSTRUCTION CODE OF EGYPT UNLESS OTHERWISE SPECIFIED.

- ALL DIMENSIONS ARE IN METERS. IF IN DOUBT ASK, DO NOT SCALE.

- THESE DRAWINGS SHALL BE READ IN CONJUNCTION WITH ALL RELEVANT STRUCTURAL + ALL OTHER CONSULTANTS DRAWINGS/DETAILS & WITH ANY OTHER WRITTEN INSTRUCTIONS ISSUED IN THE COURSE OF THE CONTRACT.

- THESE DRAWINGS SHALL BE READ IN CONJUNCTION WITH ANY ENERGY RATING REPORT + SHALL BE CONSTRUCTED IN ACCORDANCE WITH THE STAMPED PLANS ENDORSED BY THE ACCREDITED THERMAL PERFORMANCE ASSESSOR WITHOUT ALTERATION



OWNER:



OCTOBER UNIVERSITY
FOR MODERN SCIENCES & ARTS
Architectural Engineering Department
Spring 2025

CLIENTS NAME:

Dr. Tarek Galal
Eng. Hend
Eng. Nermeen
Eng. Yousra

Student Name: Hadeel Zakaria
ID: 220009

PROJECT NAME:
APARTMENT BUILDING

SHEET NAME:
FIRST FLOOR

SHEET NO: E103
SCALE: 1:50

DATE: 13-5-2025





Course Info:
ASE 464
Working Drawings III

GENERAL NOTES:
- ALL MATERIALS & WORK PRACTICES SHALL COMPLY WITH, BUT NOT LIMITED TO THE BUILDING REGULATION 2019, THE NATIONAL CONSTRUCTION CODE OF EGYPT UNLESS OTHERWISE SPECIFIED.
- ALL DIMENSIONS ARE IN METERS. IF IN DOUBT ASK, DO NOT SCALE.
- THESE DRAWINGS SHALL BE READ IN CONJUNCTION WITH ALL RELEVANT STRUCTURAL + ALL OTHER CONSULTANTS DRAWINGS/DETAILS & WITH ANY OTHER WRITTEN INSTRUCTIONS ISSUED IN THE COURSE OF THE CONTRACT.
- THESE DRAWINGS SHALL BE READ IN CONJUNCTION WITH ANY ENERGY RATING REPORT + SHALL BE CONSTRUCTED IN ACCORDANCE WITH THE STAMPED PLANS ENDORSED BY THE ACCREDITED THERMAL PERFORMANCE ASSESSOR WITHOUT ALTERATION



OWNER:



CLIENTS NAME:
Dr. Tarek Galal
Eng. Hend
Eng. Nermeen
Eng. Yousra


Student Name: Hadeel Zakaria
ID: 220009

PROJECT NAME:
APARTMENT BUILDING


SHEET NAME:
ROOF FLOOR

SHEET NO:	SCALE:
E104	1:50

DATE: 13-5-2025

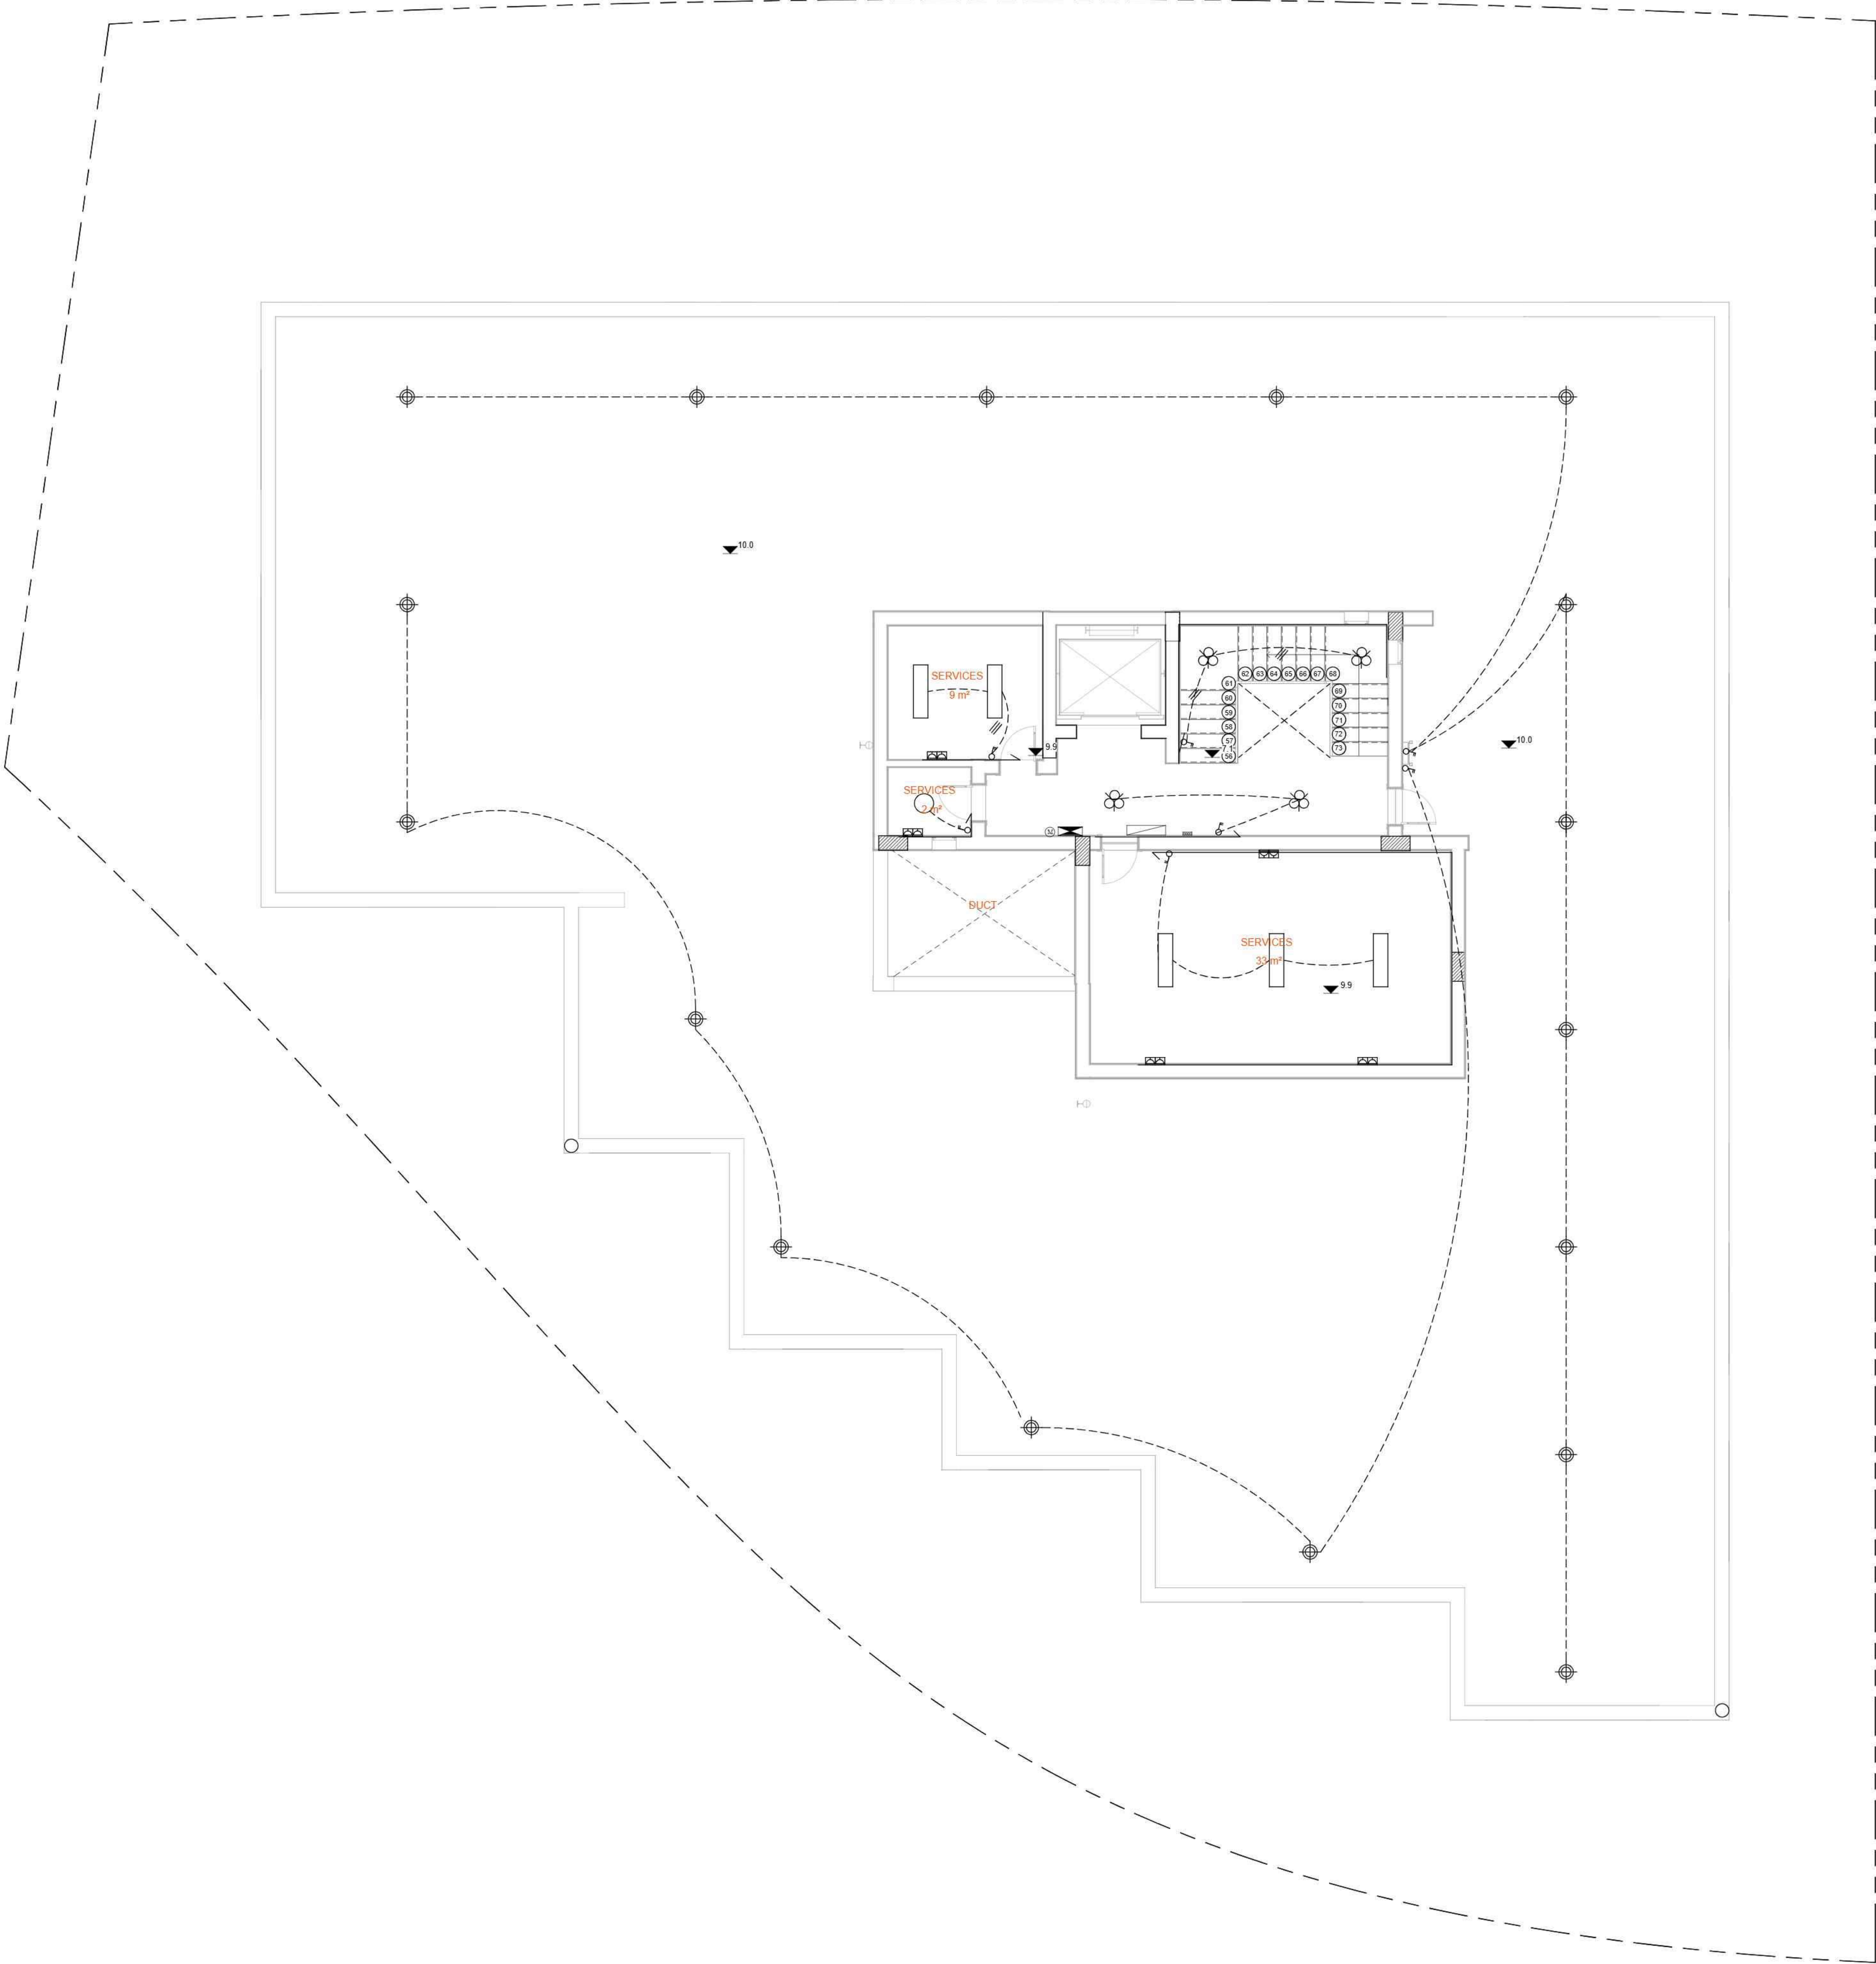

Symbols	Description
	Main Inspection Chamber 90cm*90cm
	Inspection Chamber 60cm*60cm
	Gully Trap 30cm*30cm
2' ○	2' dia Ventilation Stack
2.5' ○	2.5' dia Water Supply
3' ○	3' dia Waste Stack
4' ○	4' dia Soil Stack
1.5' ○	1.5' dia AC Stack
6'	6' dia Floor Drain
	Water Supply Flow Direction
HW 	Hot Water Direction
CW 	Cold Water Direction
	Air Conditionor
	Compressor
	Pump Machine

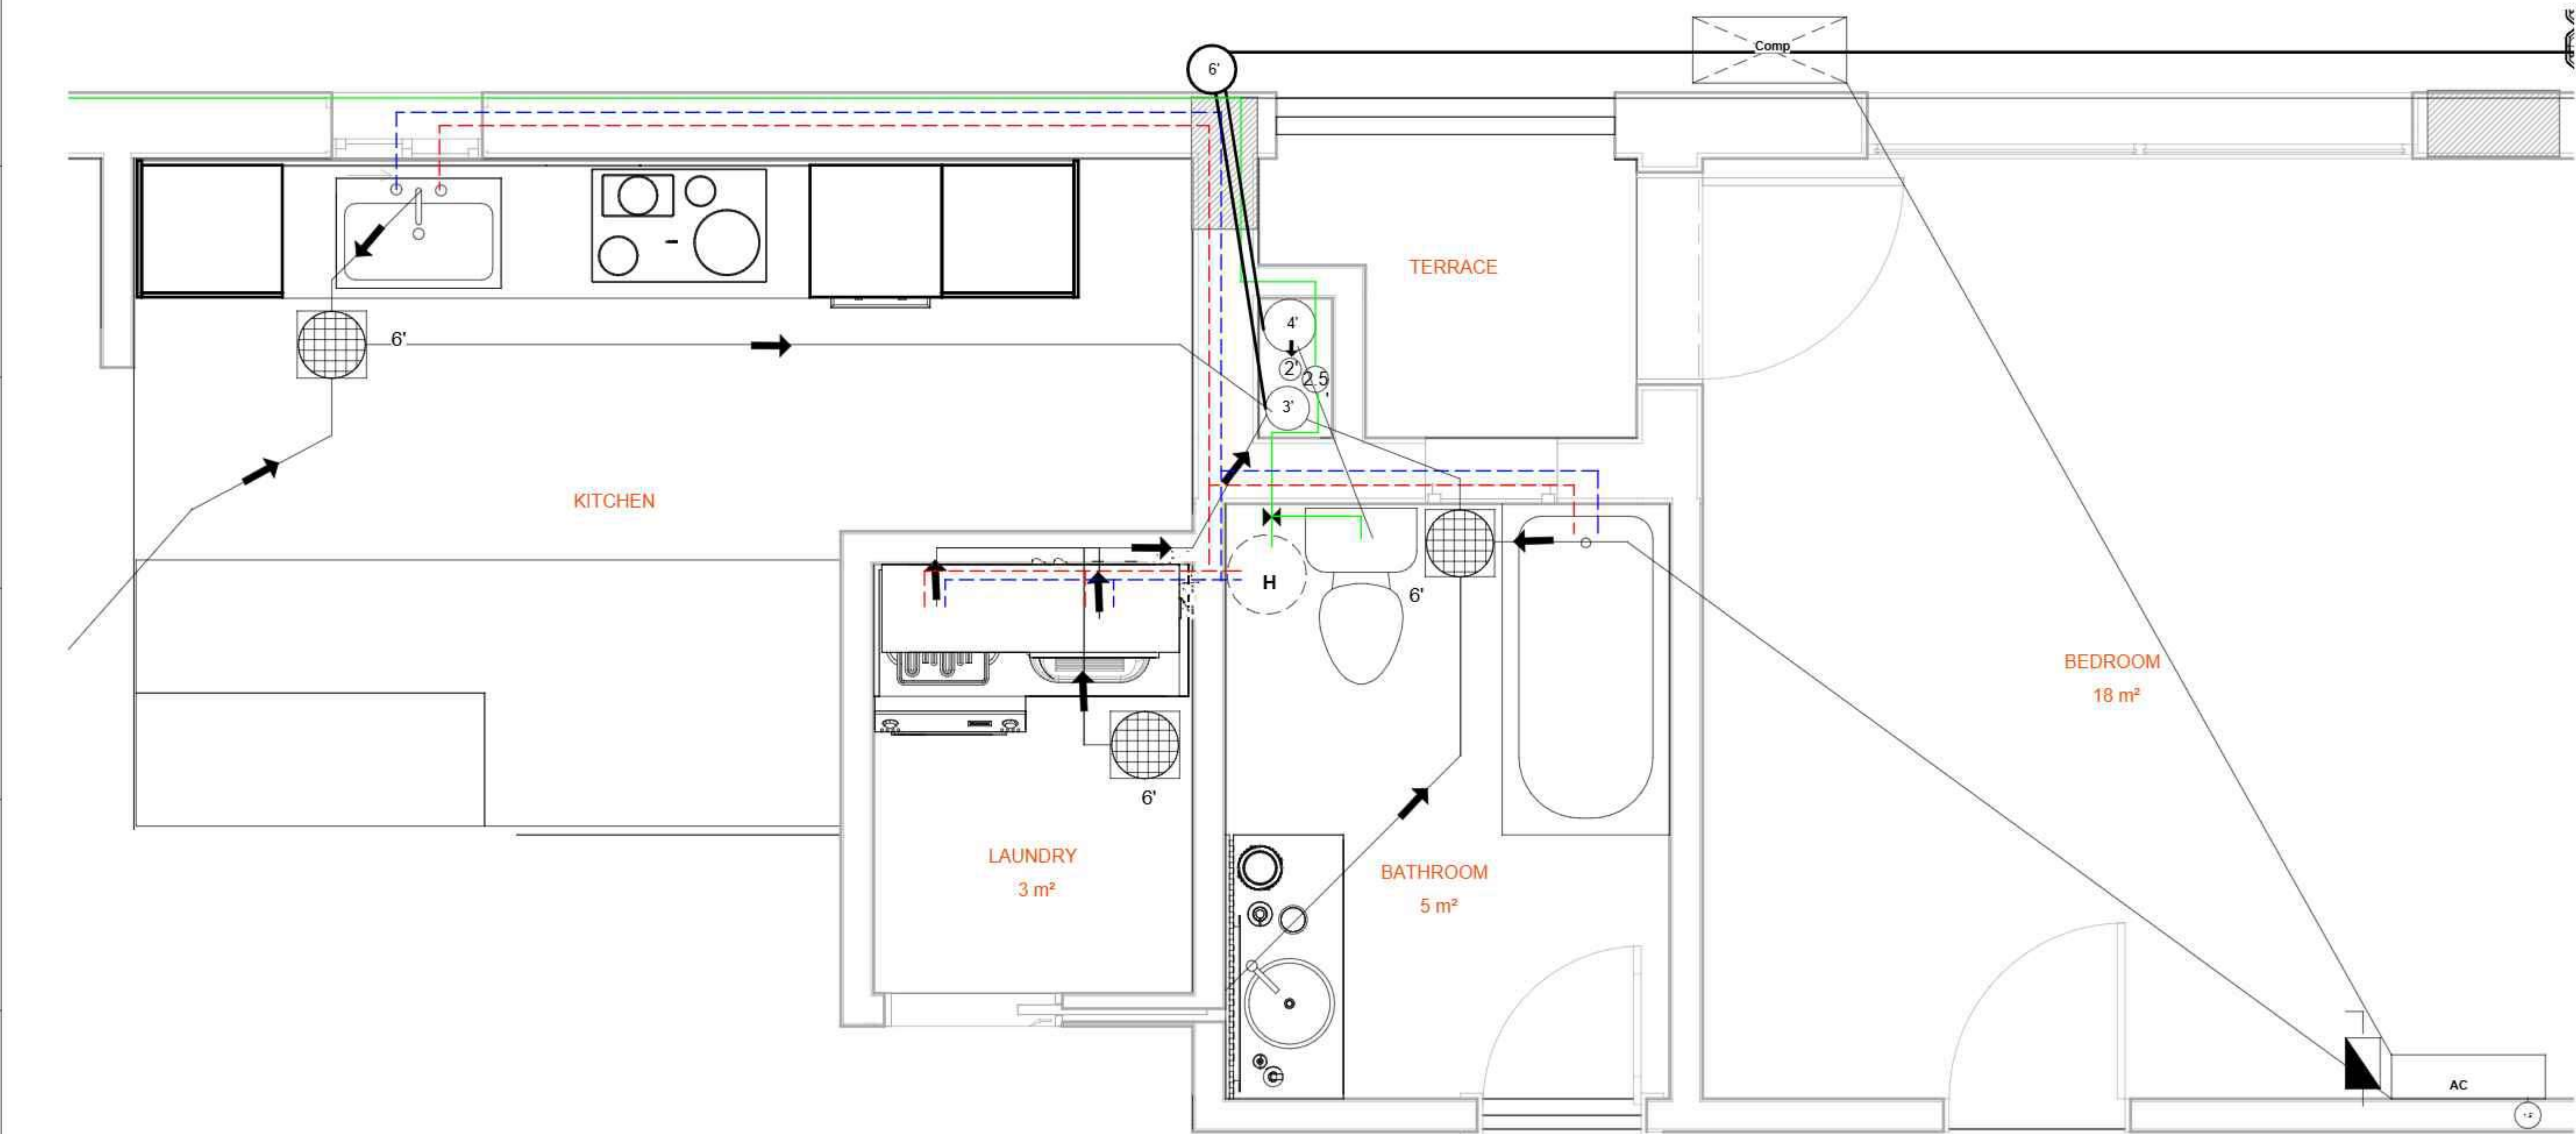

Ground Floor Plan
(Plumbing) - Callout 1
1 : 20

Plumbing Symbols
1 : 25



Course Info:
ASE 464
Working Drawings III

GENERAL NOTES:
- ALL MATERIALS & WORK PRACTICES SHALL COMPLY WITH, BUT NOT LIMITED TO THE BUILDING REGULATION 2019, THE NATIONAL CONSTRUCTION CODE of EGYPT UNLESS OTHERWISE SPECIFIED.
- ALL DIMENSIONS ARE IN METERS. IF IN DOUBT ASK, DO NOT SCALE.
- THESE DRAWINGS SHALL BE READ IN CONJUNCTION WITH ALL RELEVANT STRUCTURAL + ALL OTHER CONSULTANTS DRAWINGS/DETAILS & WITH ANY OTHER WRITTEN INSTRUCTIONS ISSUED IN THE COURSE OF THE CONTRACT.
- THESE DRAWINGS SHALL BE READ IN CONJUNCTION WITH ANY ENERGY RATING REPORT + SHALL BE CONSTRUCTED IN ACCORDANCE WITH THE STAMPED PLANS ENDORSED BY THE ACCREDITED THERMAL PERFORMANCE ASSESSOR WITHOUT ALTERATION



OWNER:

MSA UNIVERSITY
جامعة أكتوبر للعلوم الحديثة والآداب
UNIVERSITY of GREENWICH
OCTOBER UNIVERSITY
FOR MODERN SCIENCES & ARTS
Architectural Engineering Department
Spring 2025

CLIENTS NAME:
Dr. Tarek Galal
Eng. Hend
Eng. Nermeen
Eng. Yousra


Student Name: Hadeel Zakaria
ID: 220009

PROJECT NAME:
APARTMENT BUILDING

SHEET NAME:
PLUMBING DETAIL

SHEET NO: P100
SCALE: 1:20

DATE: 13-5-2025

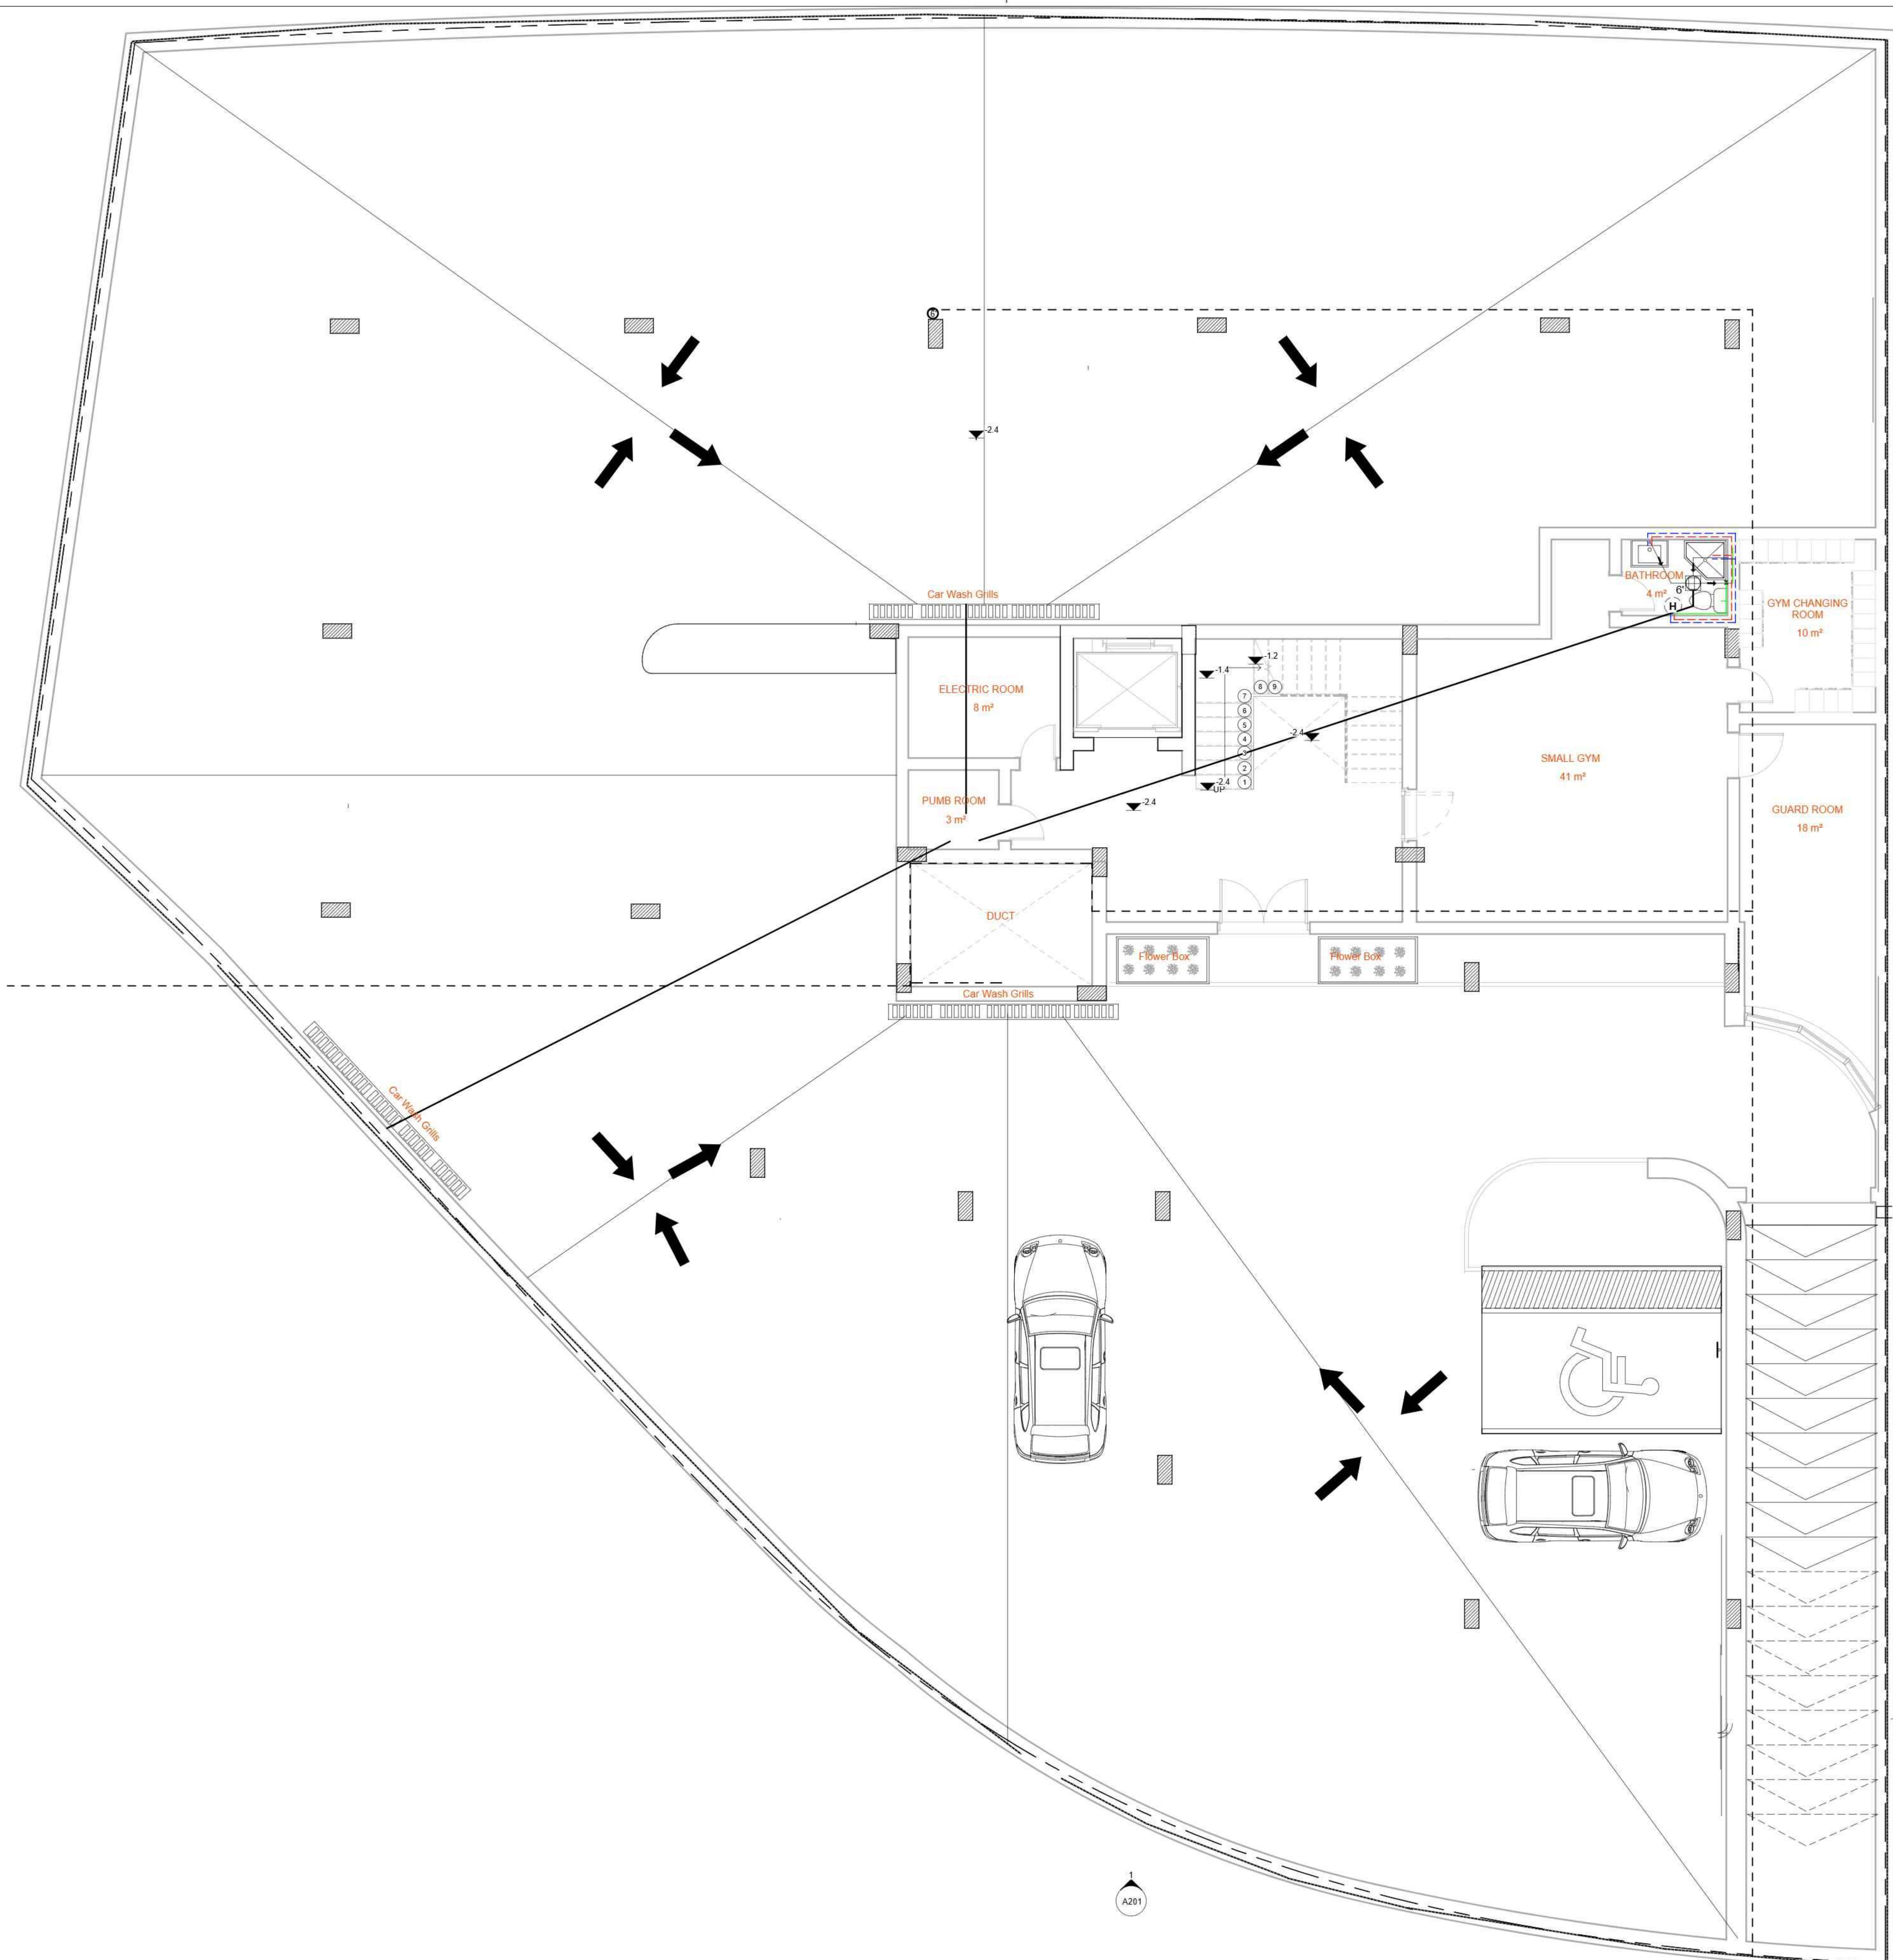

Course Info:
ASE 464
Working Drawings III

GENERAL NOTES:
- ALL MATERIALS & WORK PRACTICES SHALL COMPLY WITH, BUT NOT LIMITED TO THE BUILDING REGULATION 2019, THE NATIONAL CONSTRUCTION CODE OF EGYPT UNLESS OTHERWISE SPECIFIED.
- ALL DIMENSIONS ARE IN METERS. IF IN DOUBT ASK, DO NOT SCALE.
- THESE DRAWINGS SHALL BE READ IN CONJUNCTION WITH ALL RELEVANT STRUCTURAL + ALL OTHER CONSULTANTS DRAWINGS/DETAILS & WITH ANY OTHER WRITTEN INSTRUCTIONS ISSUED IN THE COURSE OF THE CONTRACT.
- THESE DRAWINGS SHALL BE READ IN CONJUNCTION WITH ANY ENERGY RATING REPORT + SHALL BE CONSTRUCTED IN ACCORDANCE WITH THE STAMPED PLANS ENDORSED BY THE ACCREDITED THERMAL PERFORMANCE ASSESSOR WITHOUT ALTERATION



OWNER:
 MSA UNIVERSITY
جامعة أكتوبر للعلوم الحديثة والآداب
 UNIVERSITY of GREENWICH
OCTOBER UNIVERSITY
FOR MODERN SCIENCES & ARTS
Architectural Engineering Department
Spring 2025

CLIENTS NAME:
Dr. Tarek Galal
Eng. Hend
Eng. Nermeen
Eng. Yousra

Student Name: Hadeel Zakaria
ID: 220009

PROJECT NAME:
APARTMENT BUILDING

SHEET NAME:
BASEMENT FLOOR

SHEET NO:	SCALE:
P101	1:50
DATE: 13-5-2025	

Course Info:

ASE 464

Working Drawings III

GENERAL NOTES:

- ALL MATERIALS & WORK PRACTICES SHALL COMPLY WITH, BUT NOT LIMITED TO THE BUILDING REGULATION 2019, THE NATIONAL CONSTRUCTION CODE OF EGYPT UNLESS OTHERWISE SPECIFIED.

- ALL DIMENSIONS ARE IN METERS. IF IN DOUBT ASK, DO NOT SCALE.

- THESE DRAWINGS SHALL BE READ IN CONJUNCTION WITH ALL RELEVANT STRUCTURAL + ALL OTHER CONSULTANTS DRAWINGS/DETAILS & WITH ANY OTHER WRITTEN INSTRUCTIONS ISSUED IN THE COURSE OF THE CONTRACT.

- THESE DRAWINGS SHALL BE READ IN CONJUNCTION WITH ANY ENERGY RATING REPORT + SHALL BE CONSTRUCTED IN ACCORDANCE WITH THE STAMPED PLANS ENDORSED BY THE ACCREDITED THERMAL PERFORMANCE ASSESSOR WITHOUT ALTERATION



OWNER:



OCTOBER UNIVERSITY
FOR MODERN SCIENCES & ARTS
Architectural Engineering Department
Spring 2025

CLIENTS NAME:

Dr. Tarek Galal
Eng. Hend
Eng. Nermeen
Eng. Yousra

Student Name: Hadeel Zakaria

ID: 220009

PROJECT NAME:
APARTMENT BUILDING

SHEET NAME:

GROUND FLOOR:
PLUMBING & HVAC

SHEET NO:

P102

SCALE:

1:50

DATE: 13-5-2025

Course Info:
ASE 464
Working Drawings III

GENERAL NOTES:
- ALL MATERIALS & WORK PRACTICES SHALL COMPLY WITH, BUT NOT LIMITED TO THE BUILDING REGULATION 2019, THE NATIONAL CONSTRUCTION CODE OF EGYPT UNLESS OTHERWISE SPECIFIED.
- ALL DIMENSIONS ARE IN METERS. IF IN DOUBT ASK, DO NOT SCALE.
- THESE DRAWINGS SHALL BE READ IN CONJUNCTION WITH ALL RELEVANT STRUCTURAL + ALL OTHER CONSULTANTS DRAWINGS/DETAILS & WITH ANY OTHER WRITTEN INSTRUCTIONS ISSUED IN THE COURSE OF THE CONTRACT.
- THESE DRAWINGS SHALL BE READ IN CONJUNCTION WITH ANY ENERGY RATING REPORT + SHALL BE CONSTRUCTED IN ACCORDANCE WITH THE STAMPED PLANS ENDORSED BY THE ACCREDITED THERMAL PERFORMANCE ASSESSOR WITHOUT ALTERATION



OWNER:



OCTOBER UNIVERSITY
FOR MODERN SCIENCES & ARTS
Architectural Engineering Department
Spring 2025

CLIENTS NAME:
Dr. Tarek Galal
Eng. Hend
Eng. Nermeen
Eng. Yousra

Student Name: Hadeel Zakaria
ID: 220009

PROJECT NAME:
APARTMENT BUILDING

SHEET NAME:
GROUND FLOOR:
WATER SUPPLY

SHEET NO: P102
SCALE: 1:50

DATE: 13-5-2025



Ground Floor Plan (Water Supply)
1:50

Course Info:
ASE 464
Working Drawings III

GENERAL NOTES:

- ALL MATERIALS & WORK PRACTICES SHALL COMPLY WITH, BUT NOT LIMITED TO THE BUILDING REGULATION 2019, THE NATIONAL CONSTRUCTION CODE OF EGYPT UNLESS OTHERWISE SPECIFIED.

- ALL DIMENSIONS ARE IN METERS. IF IN DOUBT ASK, DO NOT SCALE.

- THESE DRAWINGS SHALL BE READ IN CONJUNCTION WITH ALL RELEVANT STRUCTURAL + ALL OTHER CONSULTANTS DRAWINGS/DETAILS & WITH ANY OTHER WRITTEN INSTRUCTIONS ISSUED IN THE COURSE OF THE CONTRACT.

- THESE DRAWINGS SHALL BE READ IN CONJUNCTION WITH ANY ENERGY RATING REPORT + SHALL BE CONSTRUCTED IN ACCORDANCE WITH THE STAMPED PLANS ENDORSED BY THE ACCREDITED THERMAL PERFORMANCE ASSESSOR WITHOUT ALTERATION



OWNER:



OCTOBER UNIVERSITY
FOR MODERN SCIENCES & ARTS
Architectural Engineering Department
Spring 2025

CLIENTS NAME:

Dr. Tarek Galal
Eng. Hend
Eng. Nermeen
Eng. Yousra

Student Name: Hadeel Zakaria


ID: 220009

PROJECT NAME:
APARTMENT BUILDING

SHEET NAME:
GROUND FLOOR:
WATER SUPPLY

SHEET NO: P102 SCALE: 1:50

DATE: 13-5-2025

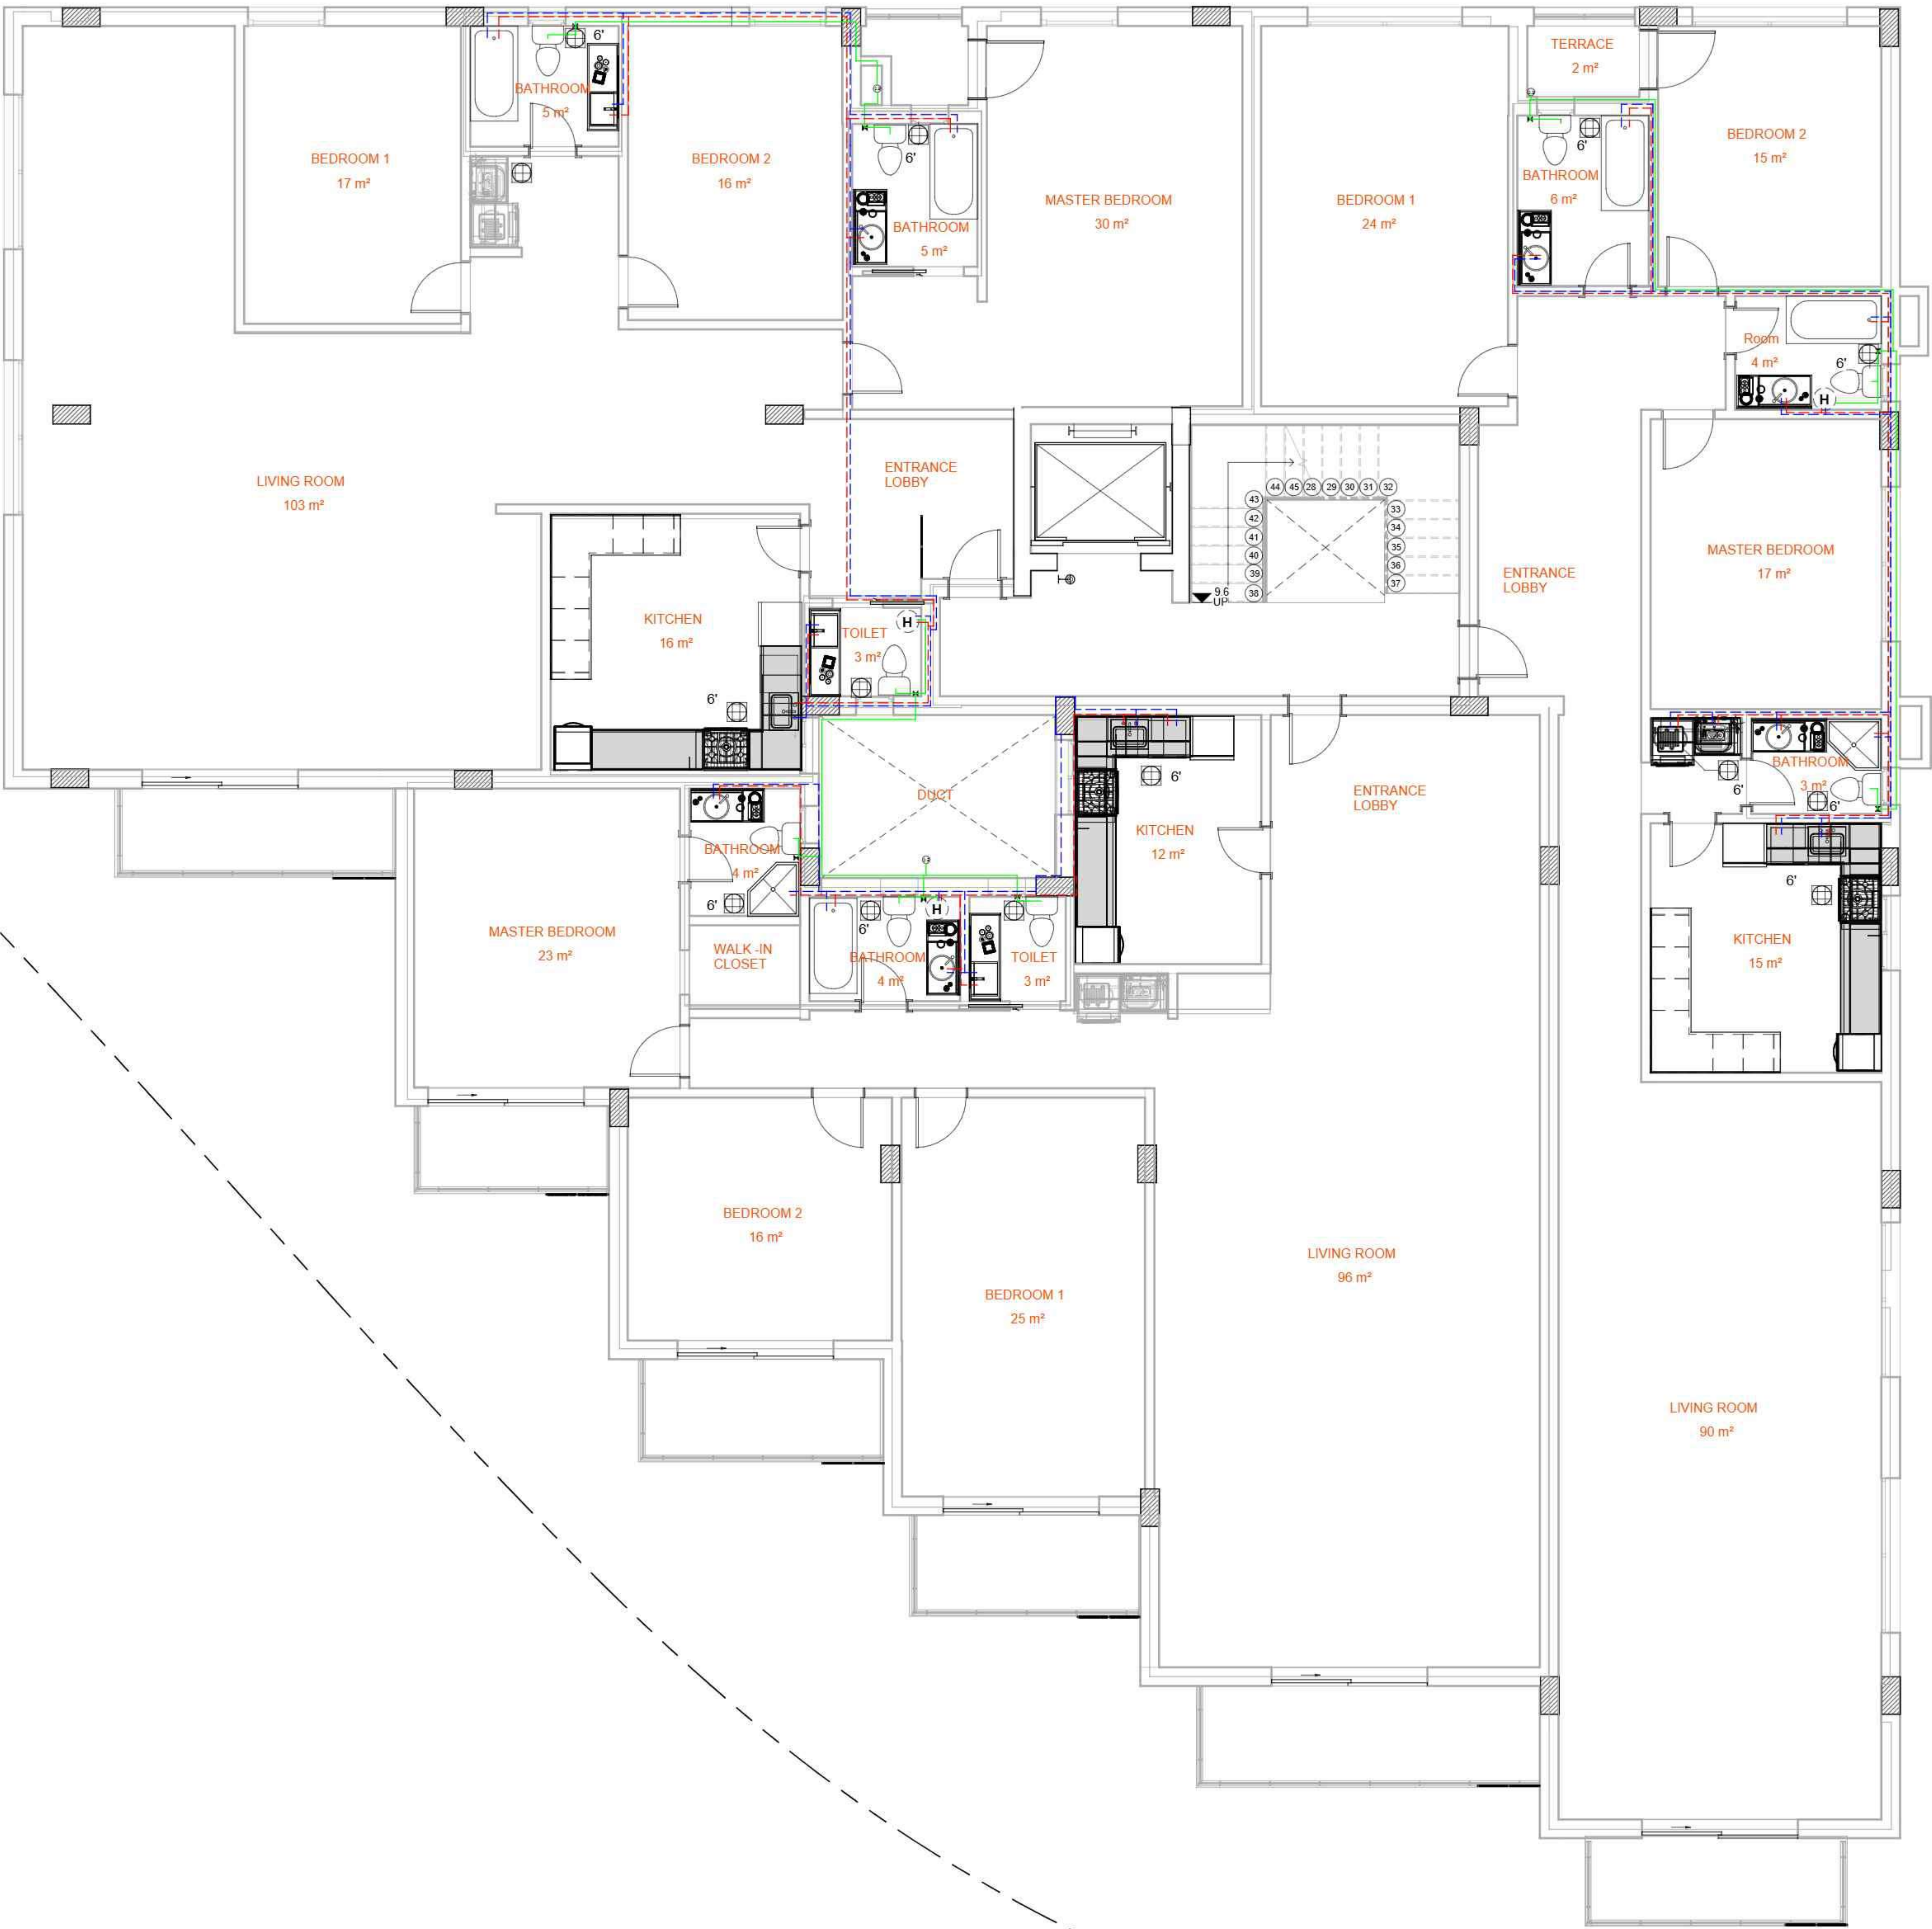

Course Info:
ASE 464
Working Drawings III

GENERAL NOTES:

- ALL MATERIALS & WORK PRACTICES SHALL COMPLY WITH, BUT NOT LIMITED TO THE BUILDING REGULATION 2019, THE NATIONAL CONSTRUCTION CODE OF EGYPT UNLESS OTHERWISE SPECIFIED.

- ALL DIMENSIONS ARE IN METERS. IF IN DOUBT ASK, DO NOT SCALE.

- THESE DRAWINGS SHALL BE READ IN CONJUNCTION WITH ALL RELEVANT STRUCTURAL + ALL OTHER CONSULTANTS DRAWINGS/DETAILS & WITH ANY OTHER WRITTEN INSTRUCTIONS ISSUED IN THE COURSE OF THE CONTRACT.

- THESE DRAWINGS SHALL BE READ IN CONJUNCTION WITH ANY ENERGY RATING REPORT + SHALL BE CONSTRUCTED IN ACCORDANCE WITH THE STAMPED PLANS ENDORSED BY THE ACCREDITED THERMAL PERFORMANCE ASSESSOR WITHOUT ALTERATION



OWNER:



OCTOBER UNIVERSITY
FOR MODERN SCIENCES & ARTS
Architectural Engineering Department
Spring 2025

CLIENTS NAME:

Dr. Tarek Galal
Eng. Hend
Eng. Nermeen
Eng. Yousra

Student Name: Hadeel Zakaria


ID: 220009

PROJECT NAME:
APARTMENT BUILDING

SHEET NAME:
FIRST FLOOR:
PLUMBING & HVAC

SHEET NO: P103 SCALE: 1:50

DATE: 13-5-2025

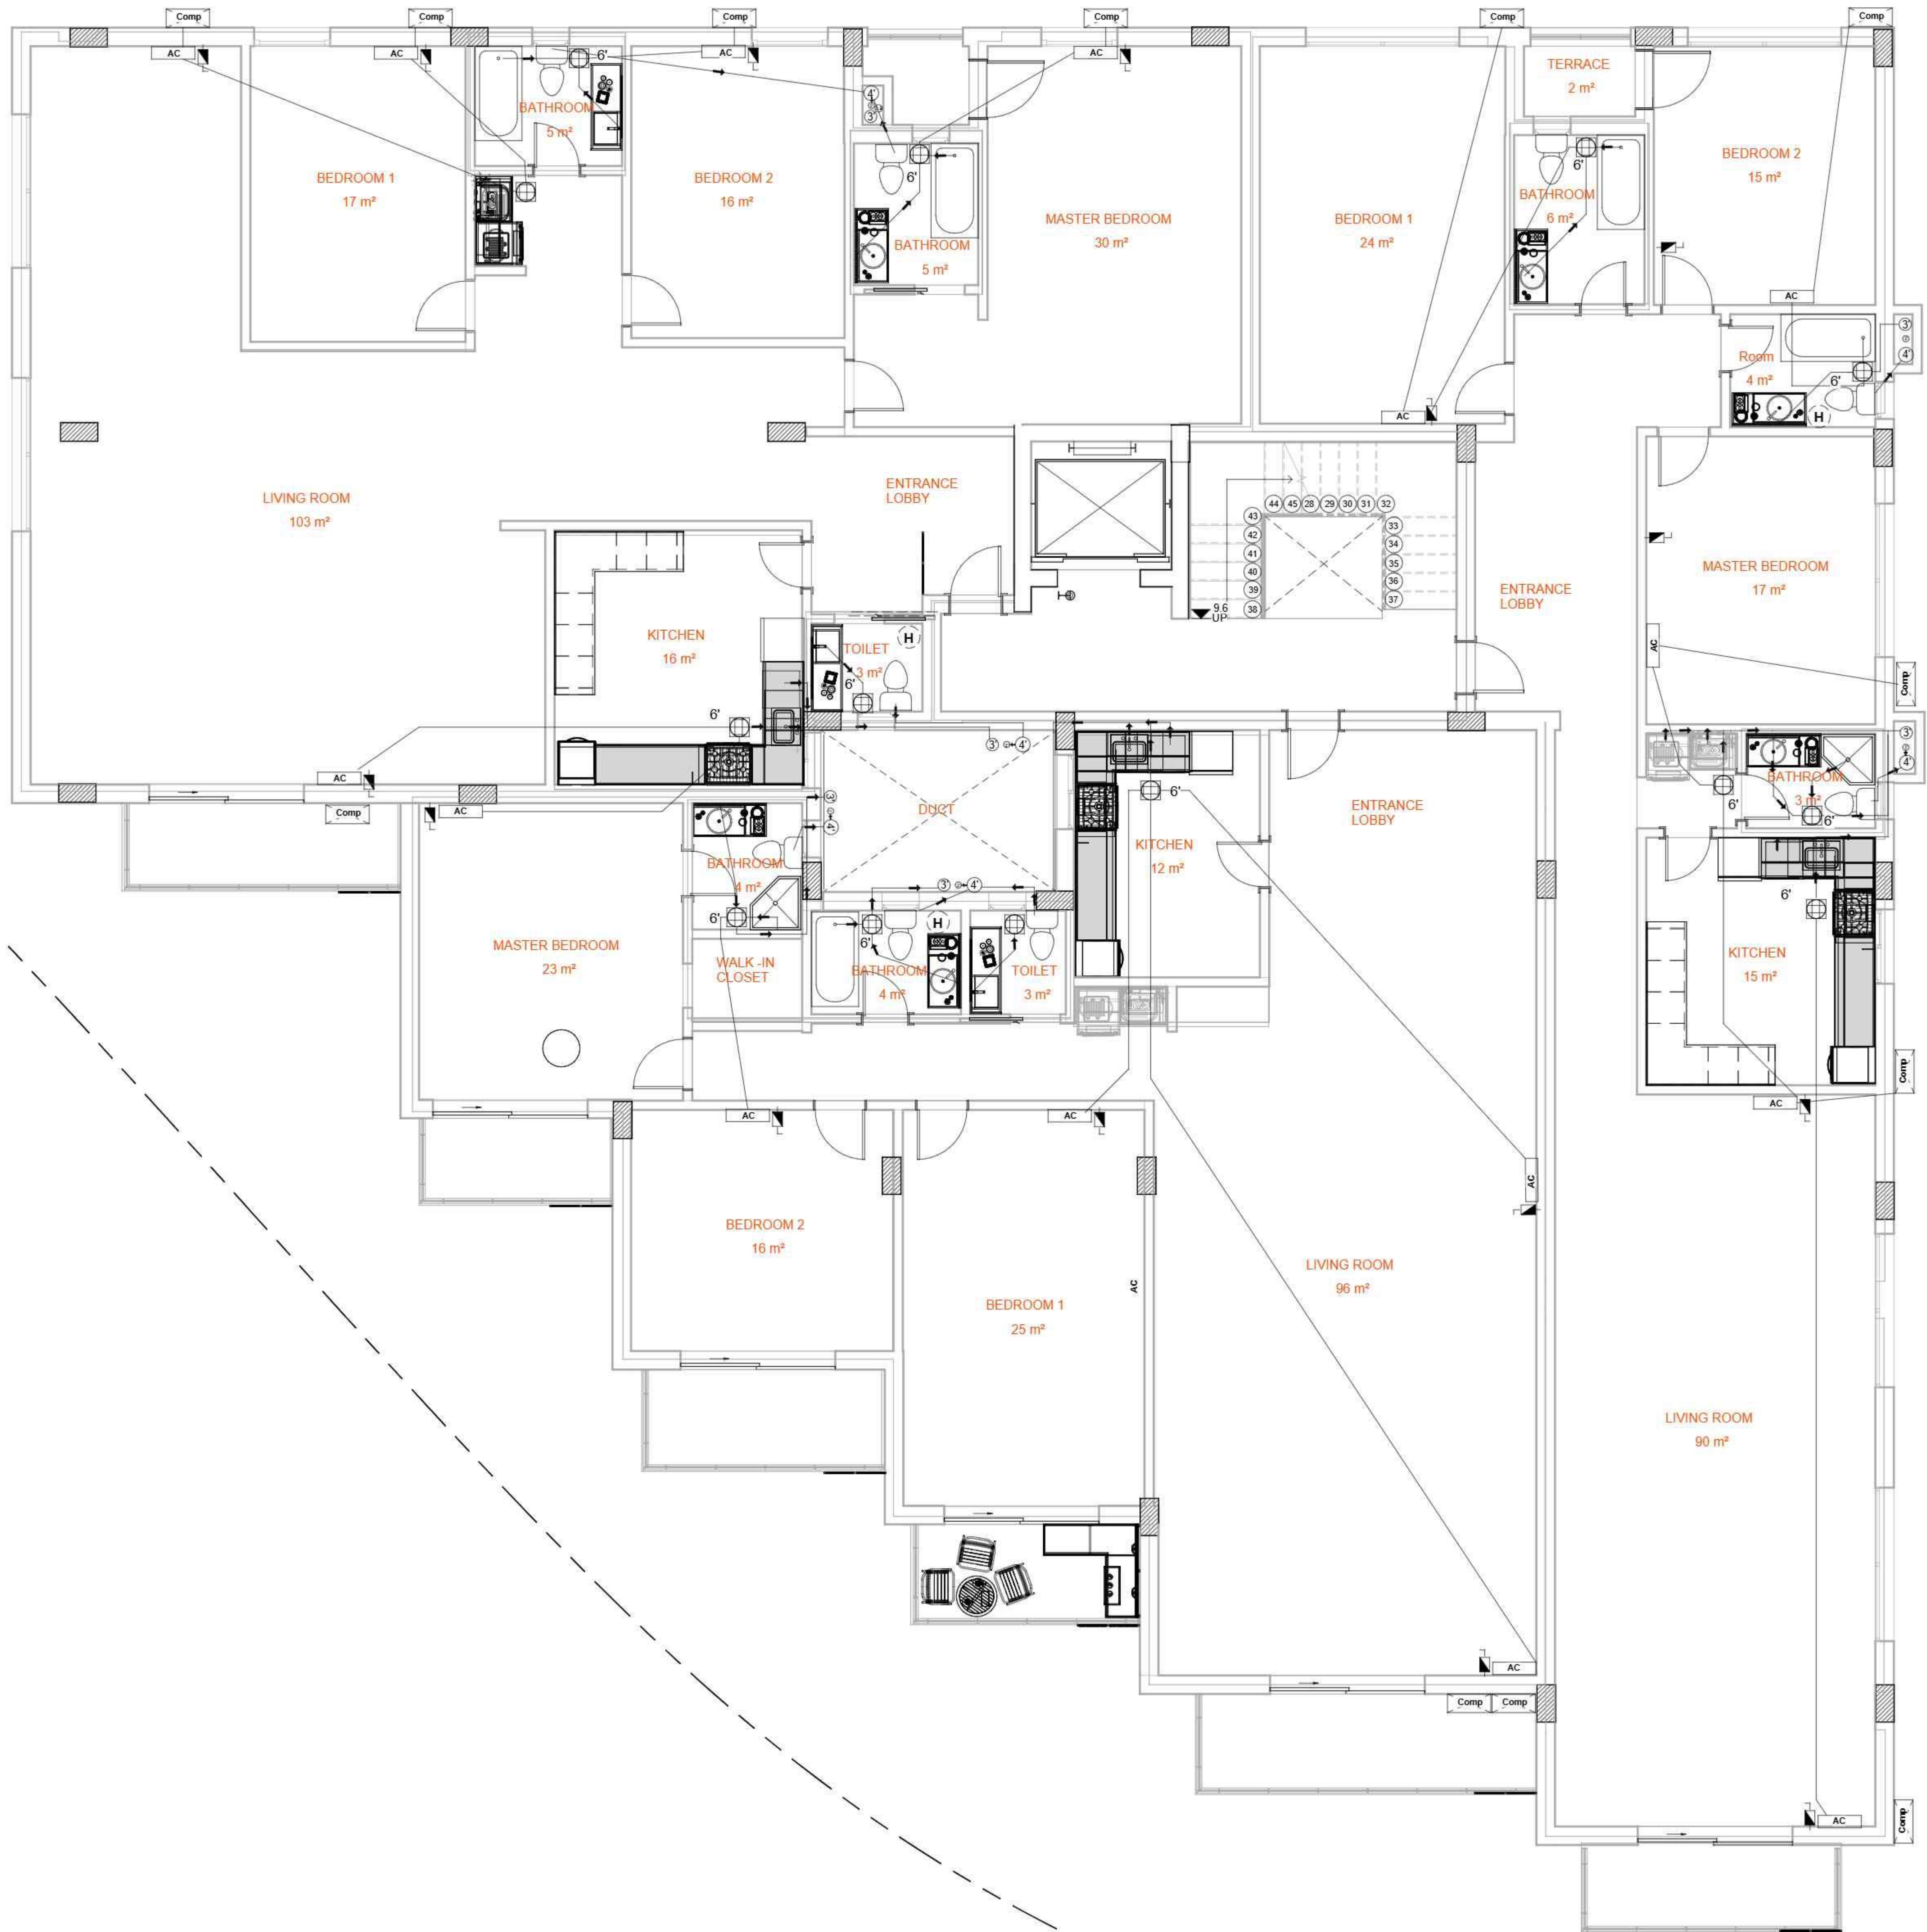



OWNER:

CLIENTS NAME:
Dr. Tarek Galal
Eng. Hend
Eng. Nermeen
Eng. Yousra

Student Name: Hadeel Zakaria
ID: 220009


PROJECT NAME:
APARTMENT BUILDING

SHEET NAME:

SHEET NO:

SCALE:

DATE: 13-5-2025

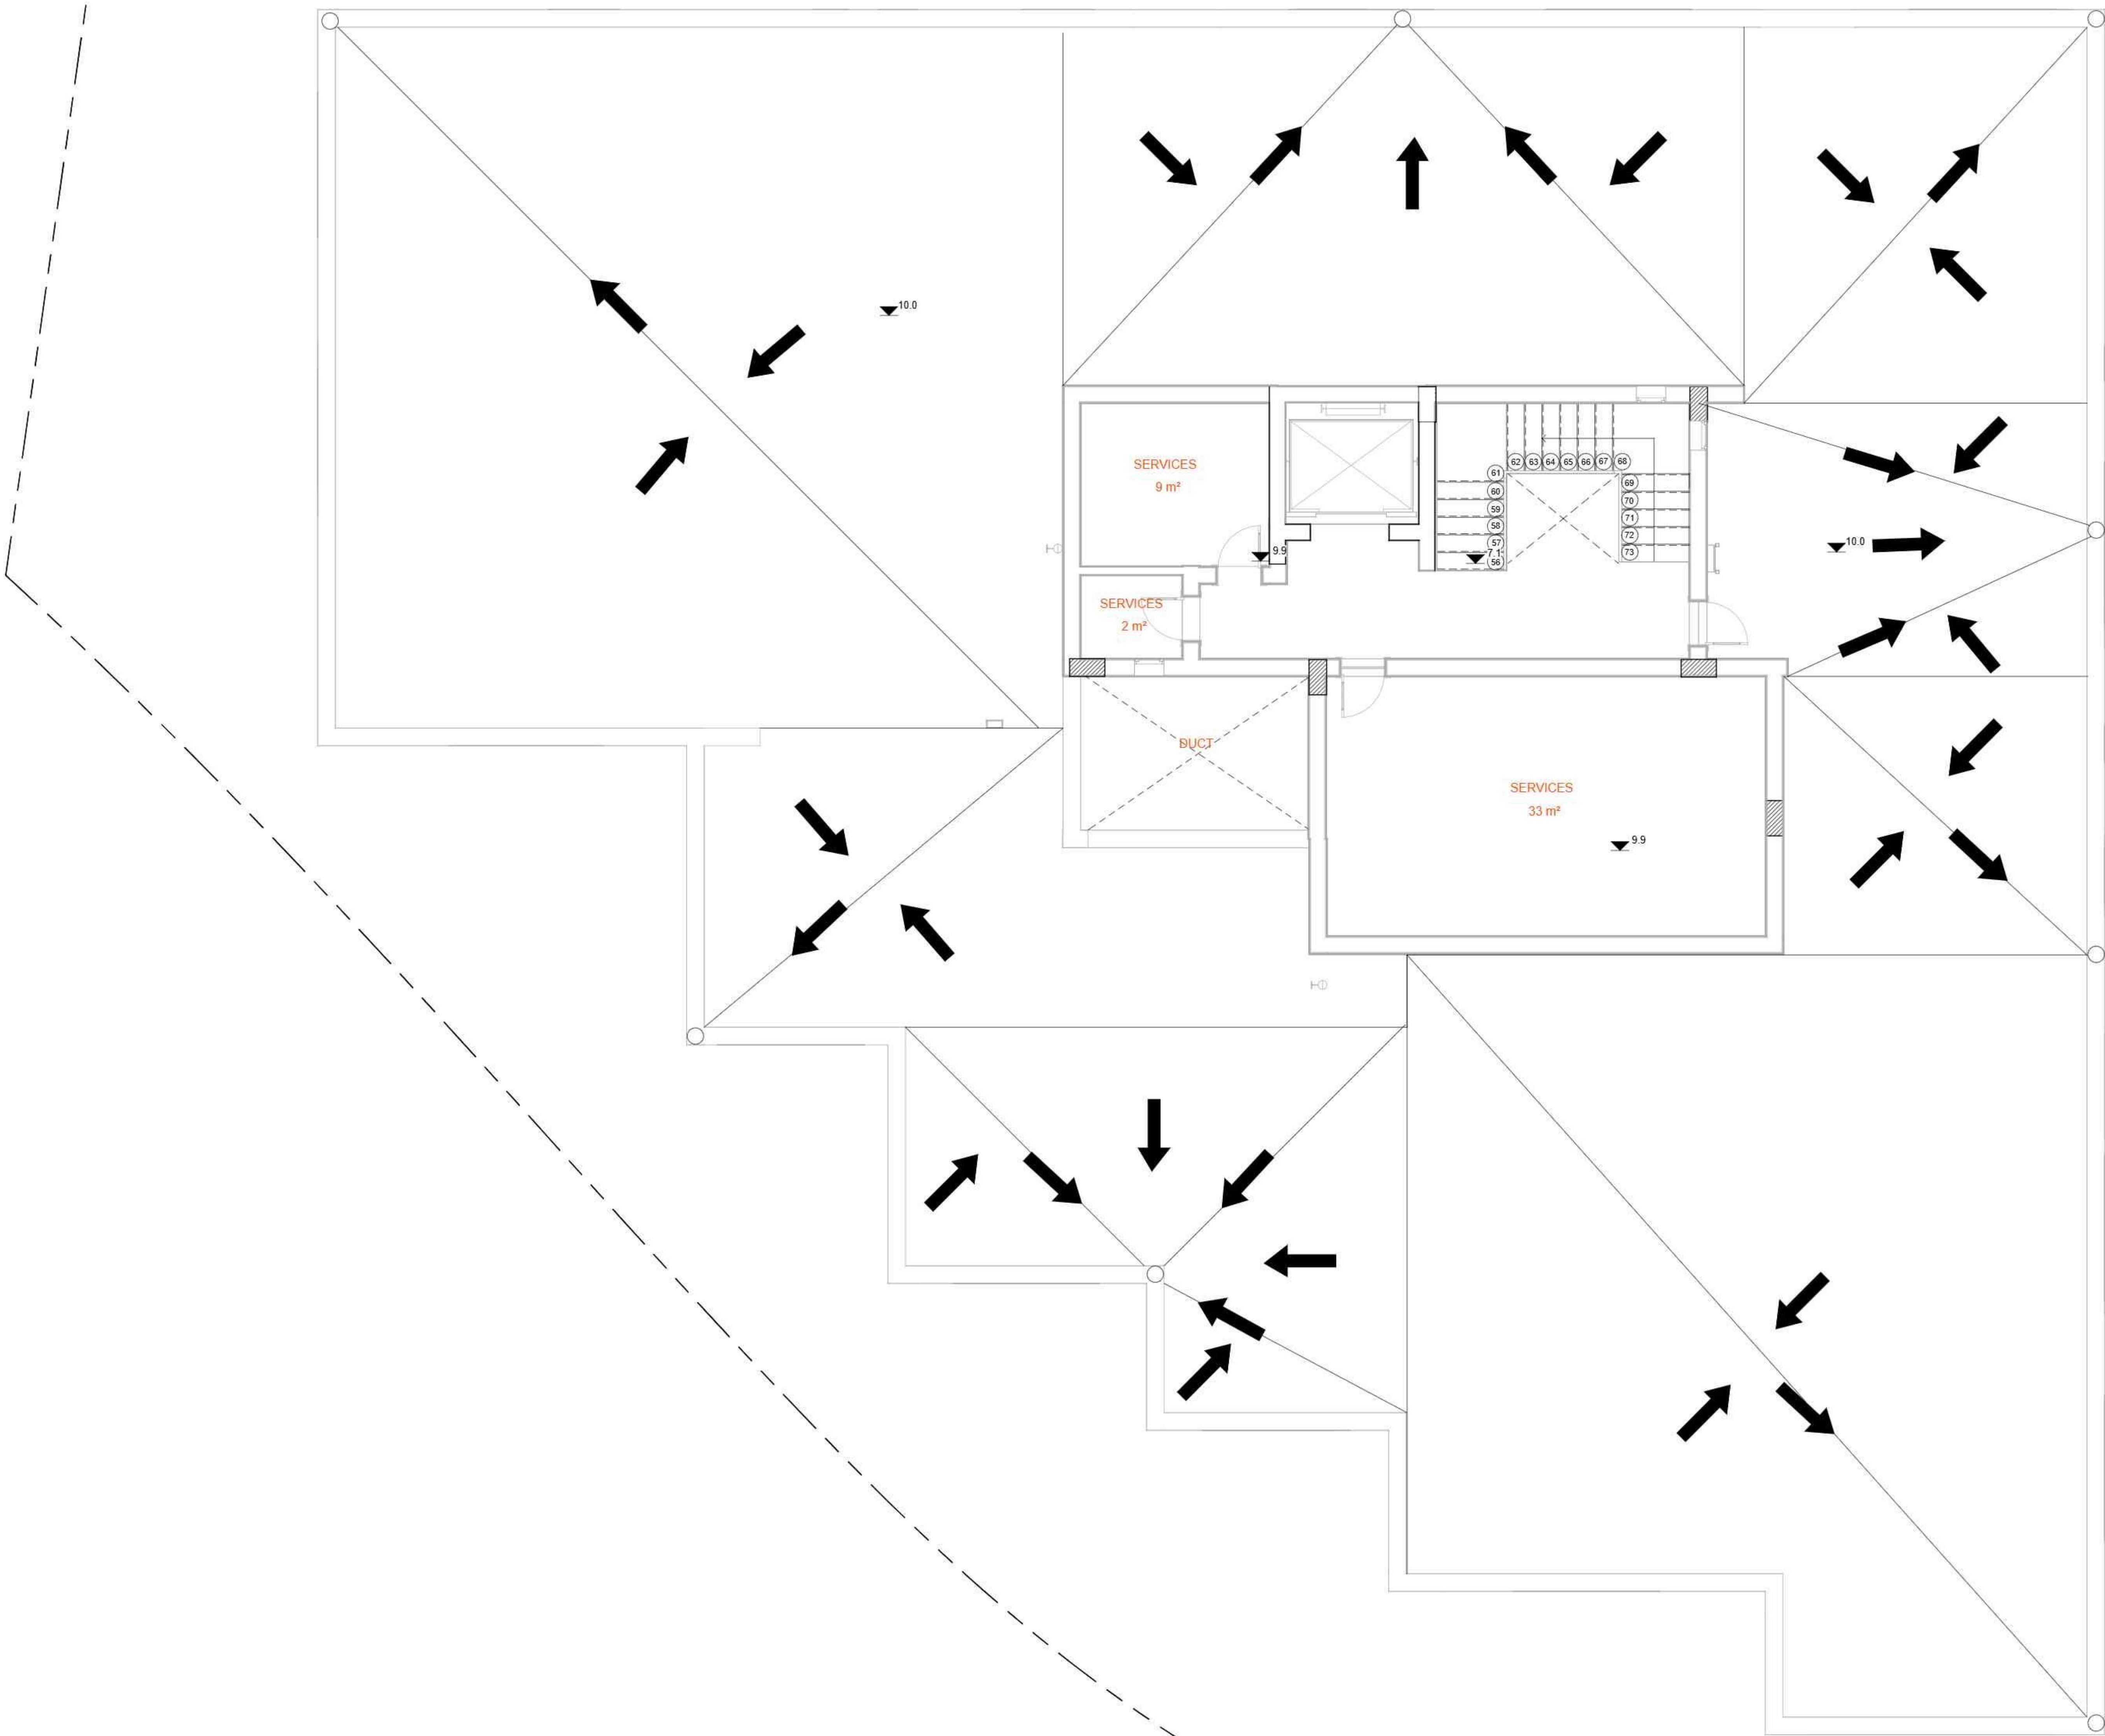



Course Info: 
ASE 464
Working Drawings III

GENERAL NOTES:
- ALL MATERIALS & WORK PRACTICES SHALL COMPLY WITH, BUT NOT LIMITED TO THE BUILDING REGULATION 2019, THE NATIONAL CONSTRUCTION CODE of EGYPT UNLESS OTHERWISE SPECIFIED.
- ALL DIMENSIONS ARE IN METERS. IF IN DOUBT ASK, DO NOT SCALE.
Plumbing: Upper
- THESE DRAWINGS SHALL BE READ IN CONJUNCTION WITH ALL RELEVANT STRUCTURAL + ALL OTHER CONSULTANTS DRAWINGS/DETAILS & WITH ANY OTHER WRITTEN INSTRUCTIONS ISSUED IN THE COURSE OF THE CONTRACT.
P105
- THESE DRAWINGS SHALL BE READ IN CONJUNCTION WITH ANY ENERGY RATING REPORT + SHALL BE CONSTRUCTED IN ACCORDANCE WITH THE STAMPED PLANS ENDORSED BY THE ACCREDITED THERMAL PERFORMANCE ASSESSOR WITHOUT ALTERATION



OWNER:



CLIENTS NAME:
Dr. Tarek Galal
Eng. Hend
Eng. Nermeen
Eng. Yousra


Student Name: Hadeel Zakaria
ID: 220009

PROJECT NAME:
APARTMENT BUILDING

SHEET NAME:

SHEET NO:	SCALE:
-----------	--------

DATE: 13-5-2025

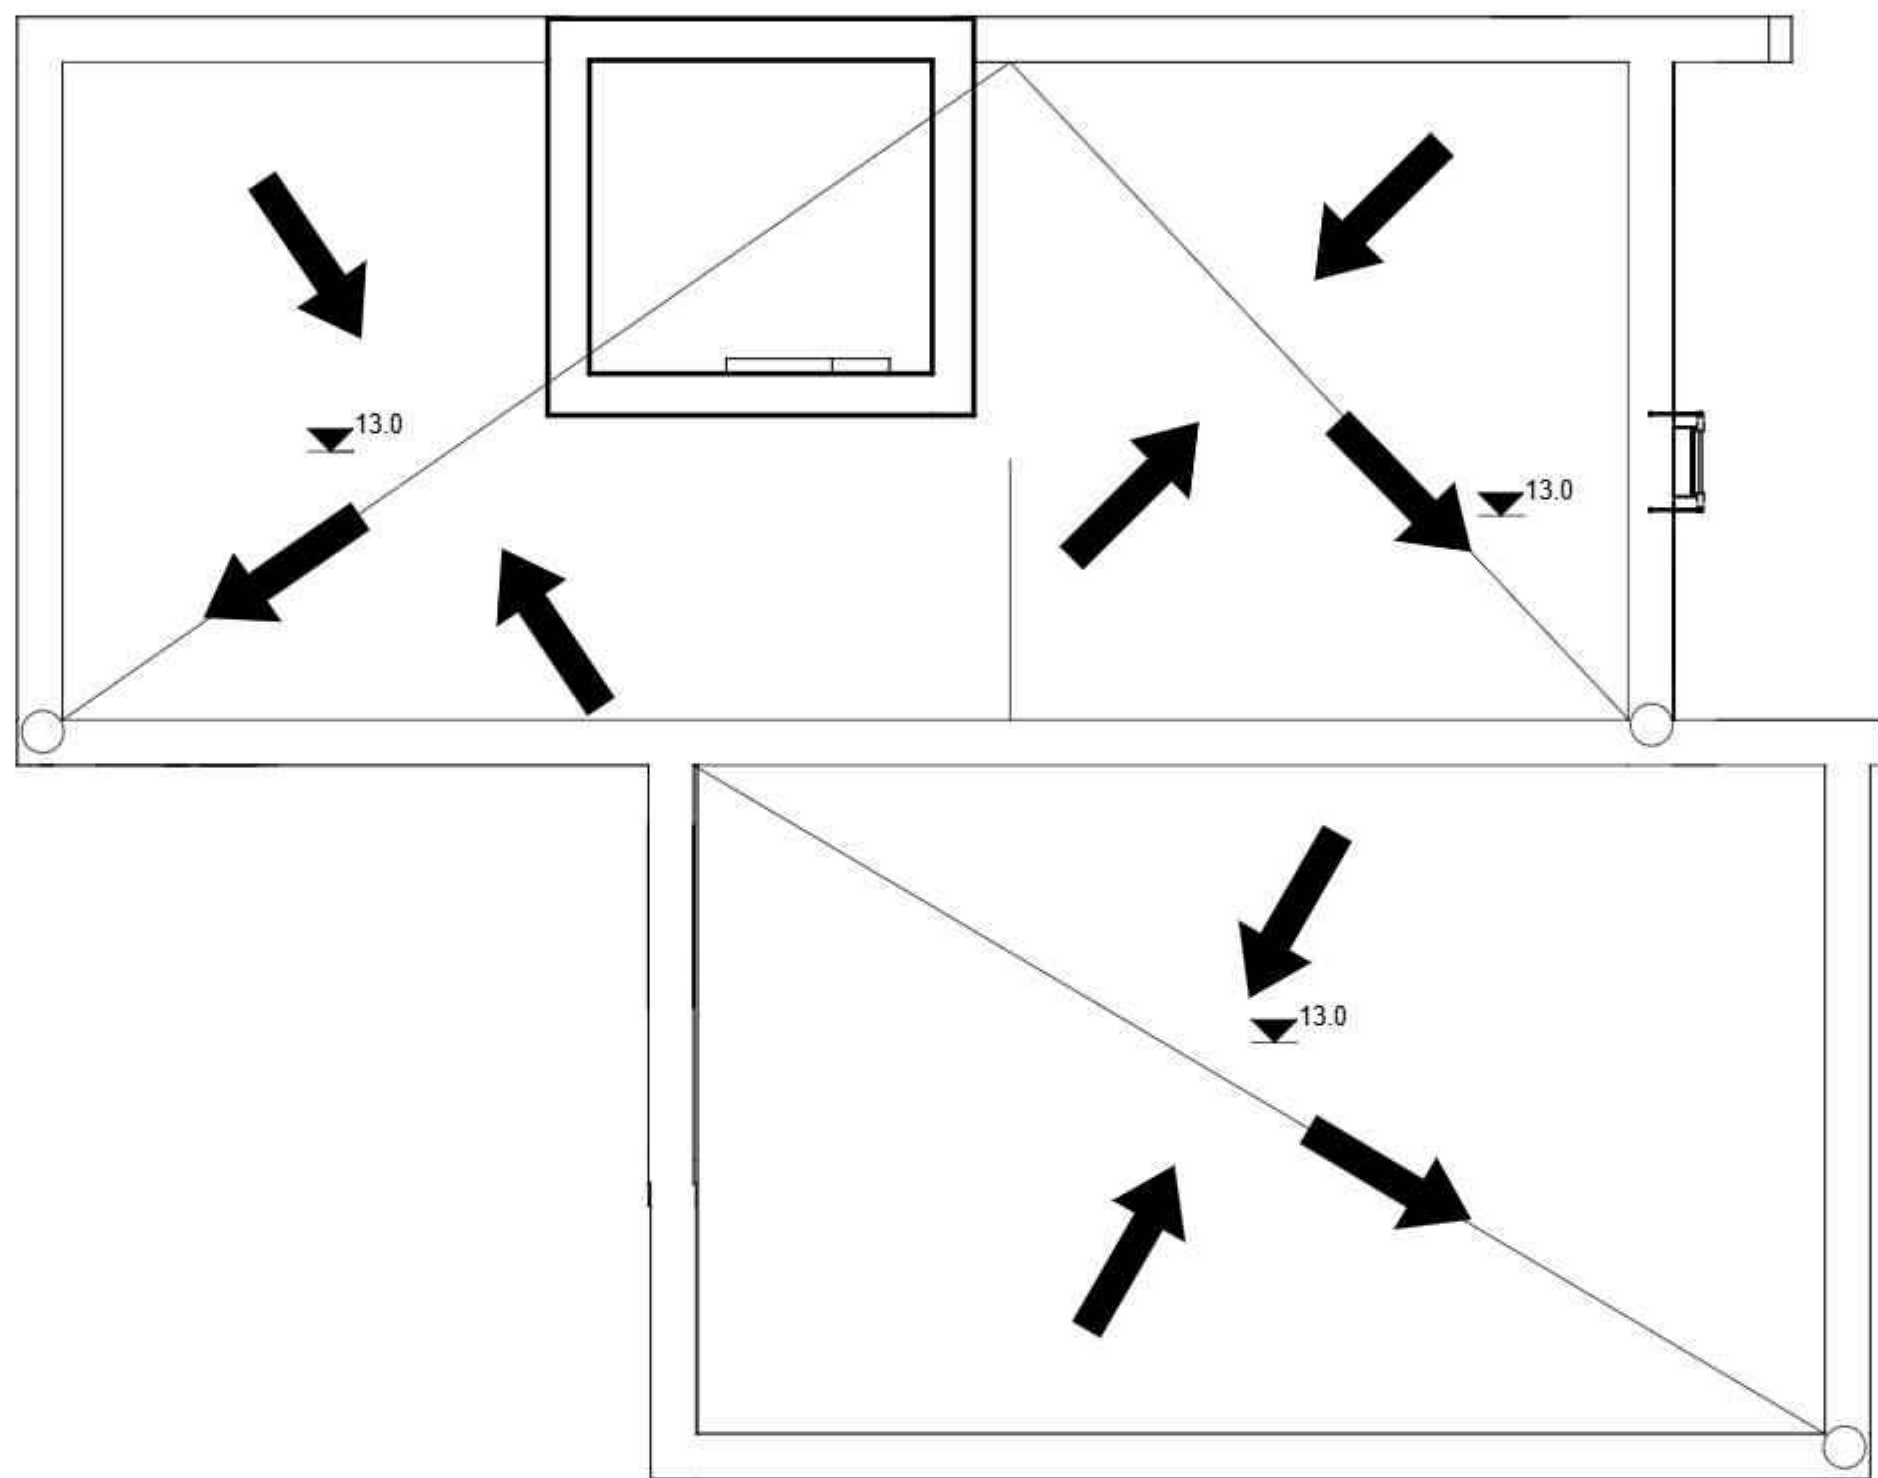



Course Info: 
ASE 464
Working Drawings III

GENERAL NOTES:

- ALL MATERIALS & WORK PRACTICES SHALL COMPLY WITH, BUT NOT LIMITED TO THE BUILDING REGULATION 2019, THE NATIONAL CONSTRUCTION CODE OF EGYPT UNLESS OTHERWISE SPECIFIED.

- ALL DIMENSIONS ARE IN METERS. IF IN DOUBT ASK, DO NOT SCALE.

- THESE DRAWINGS SHALL BE READ IN CONJUNCTION WITH ALL RELEVANT STRUCTURAL + ALL OTHER CONSULTANTS DRAWINGS/DETAILS & WITH ANY OTHER WRITTEN INSTRUCTIONS ISSUED IN THE COURSE OF THE CONTRACT.

- THESE DRAWINGS SHALL BE READ IN CONJUNCTION WITH ANY ENERGY RATING REPORT + SHALL BE CONSTRUCTED IN ACCORDANCE WITH THE STAMPED PLANS ENDORSED BY THE ACCREDITED THERMAL PERFORMANCE ASSESSOR WITHOUT ALTERATION



OWNER:



OCTOBER UNIVERSITY
FOR MODERN SCIENCES & ARTS
Architectural Engineering Department
Spring 2025

CLIENTS NAME:

Dr. Tarek Galal
Eng. Hend
Eng. Nermeen
Eng. Yousra

Student Name: Hadeel Zakaria
ID: 220009

PROJECT NAME:
APARTMENT BUILDING

SHEET NAME:

SHEET NO:

SCALE:

DATE: 13-5-2025